

THE WEYLANDAI BUILDING

NEW CORPORATE HEADQUARTERS - BID SET

4400 Bluestem Parkway, Austin, TX

SHEET INDEX

G-001	COVER SHEET
A-101	FLOOR PLANS - DOOR TAGS
A-601	DOOR SCHEDULE
08 71 00	DOOR HARDWARE (PROJECT MANUAL)

WeylandAI Sample Architects (fictional)

THE WEYLANDAI BUILDING

NEW CORPORATE HEADQUARTERS
4400 Bluestem Parkway, Austin, TX


PROJECT NO. WAI-2026-01
BID SET 2026-10-09

COVER SHEET

SHEET


G-001

SAMPLE PROJECT - NOT A REAL BUILDING

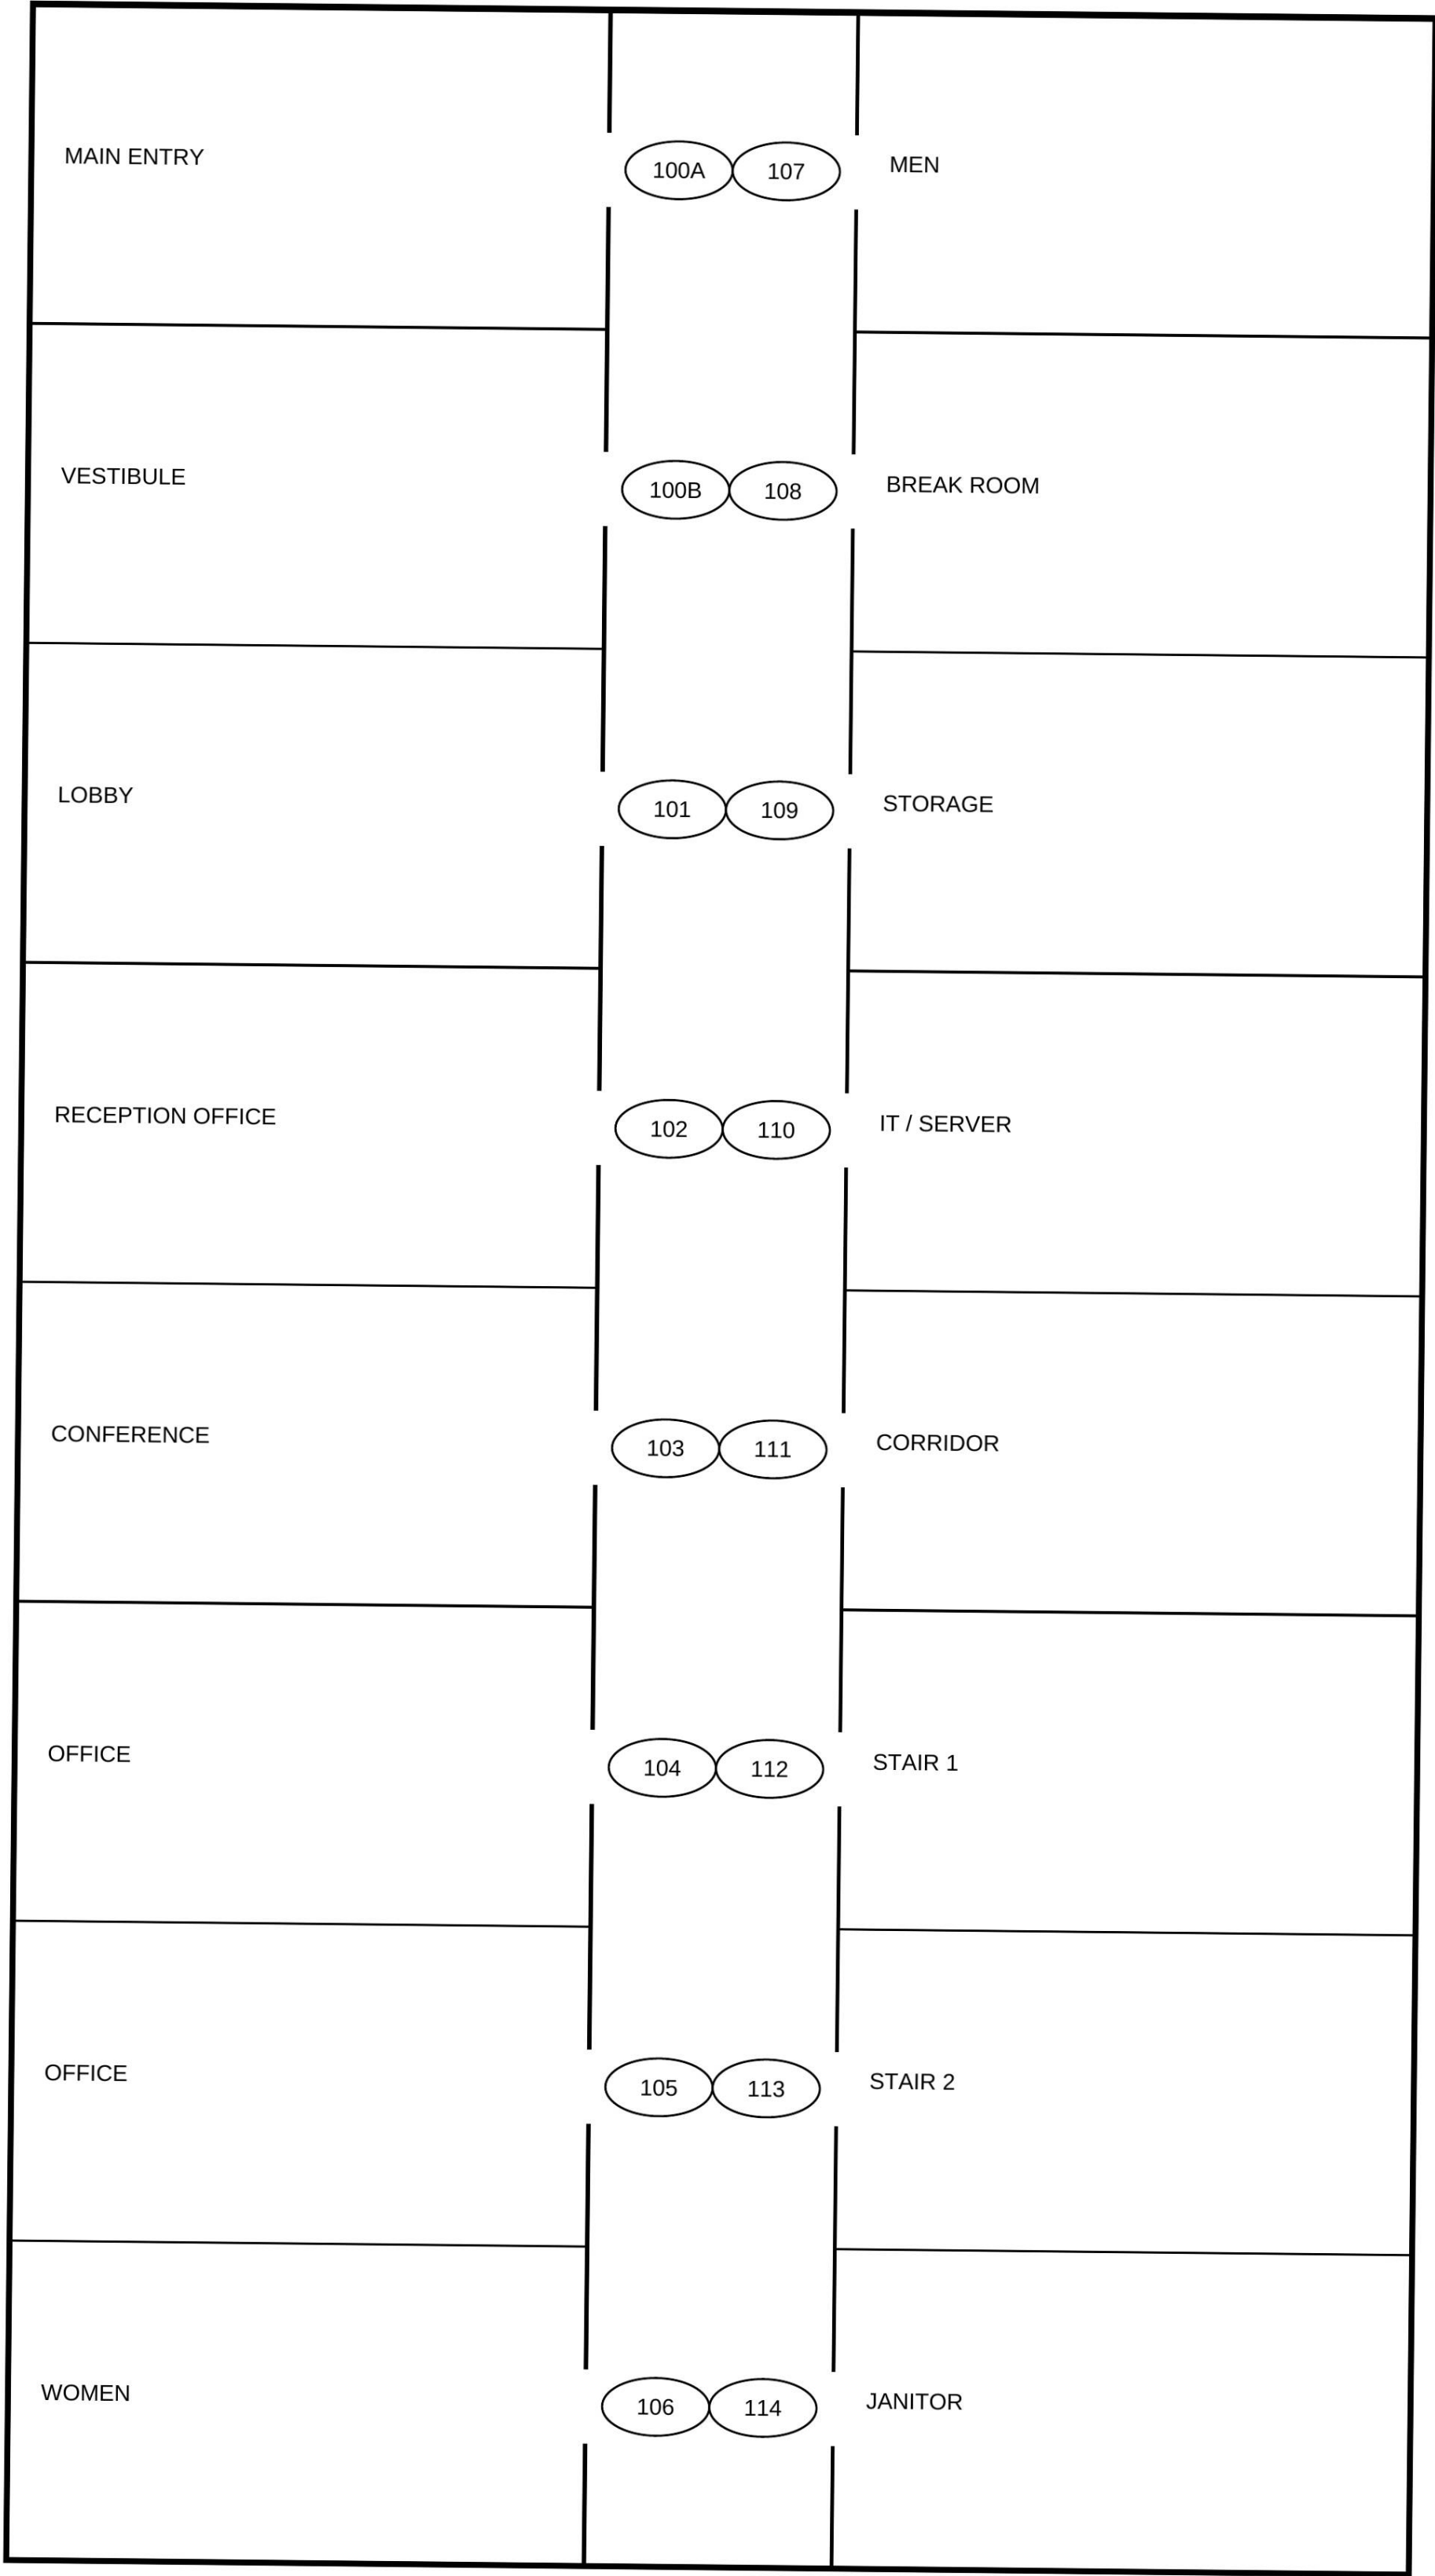


FIRST FLOOR PLAN

SCALE: 1/8" = 1'-0"

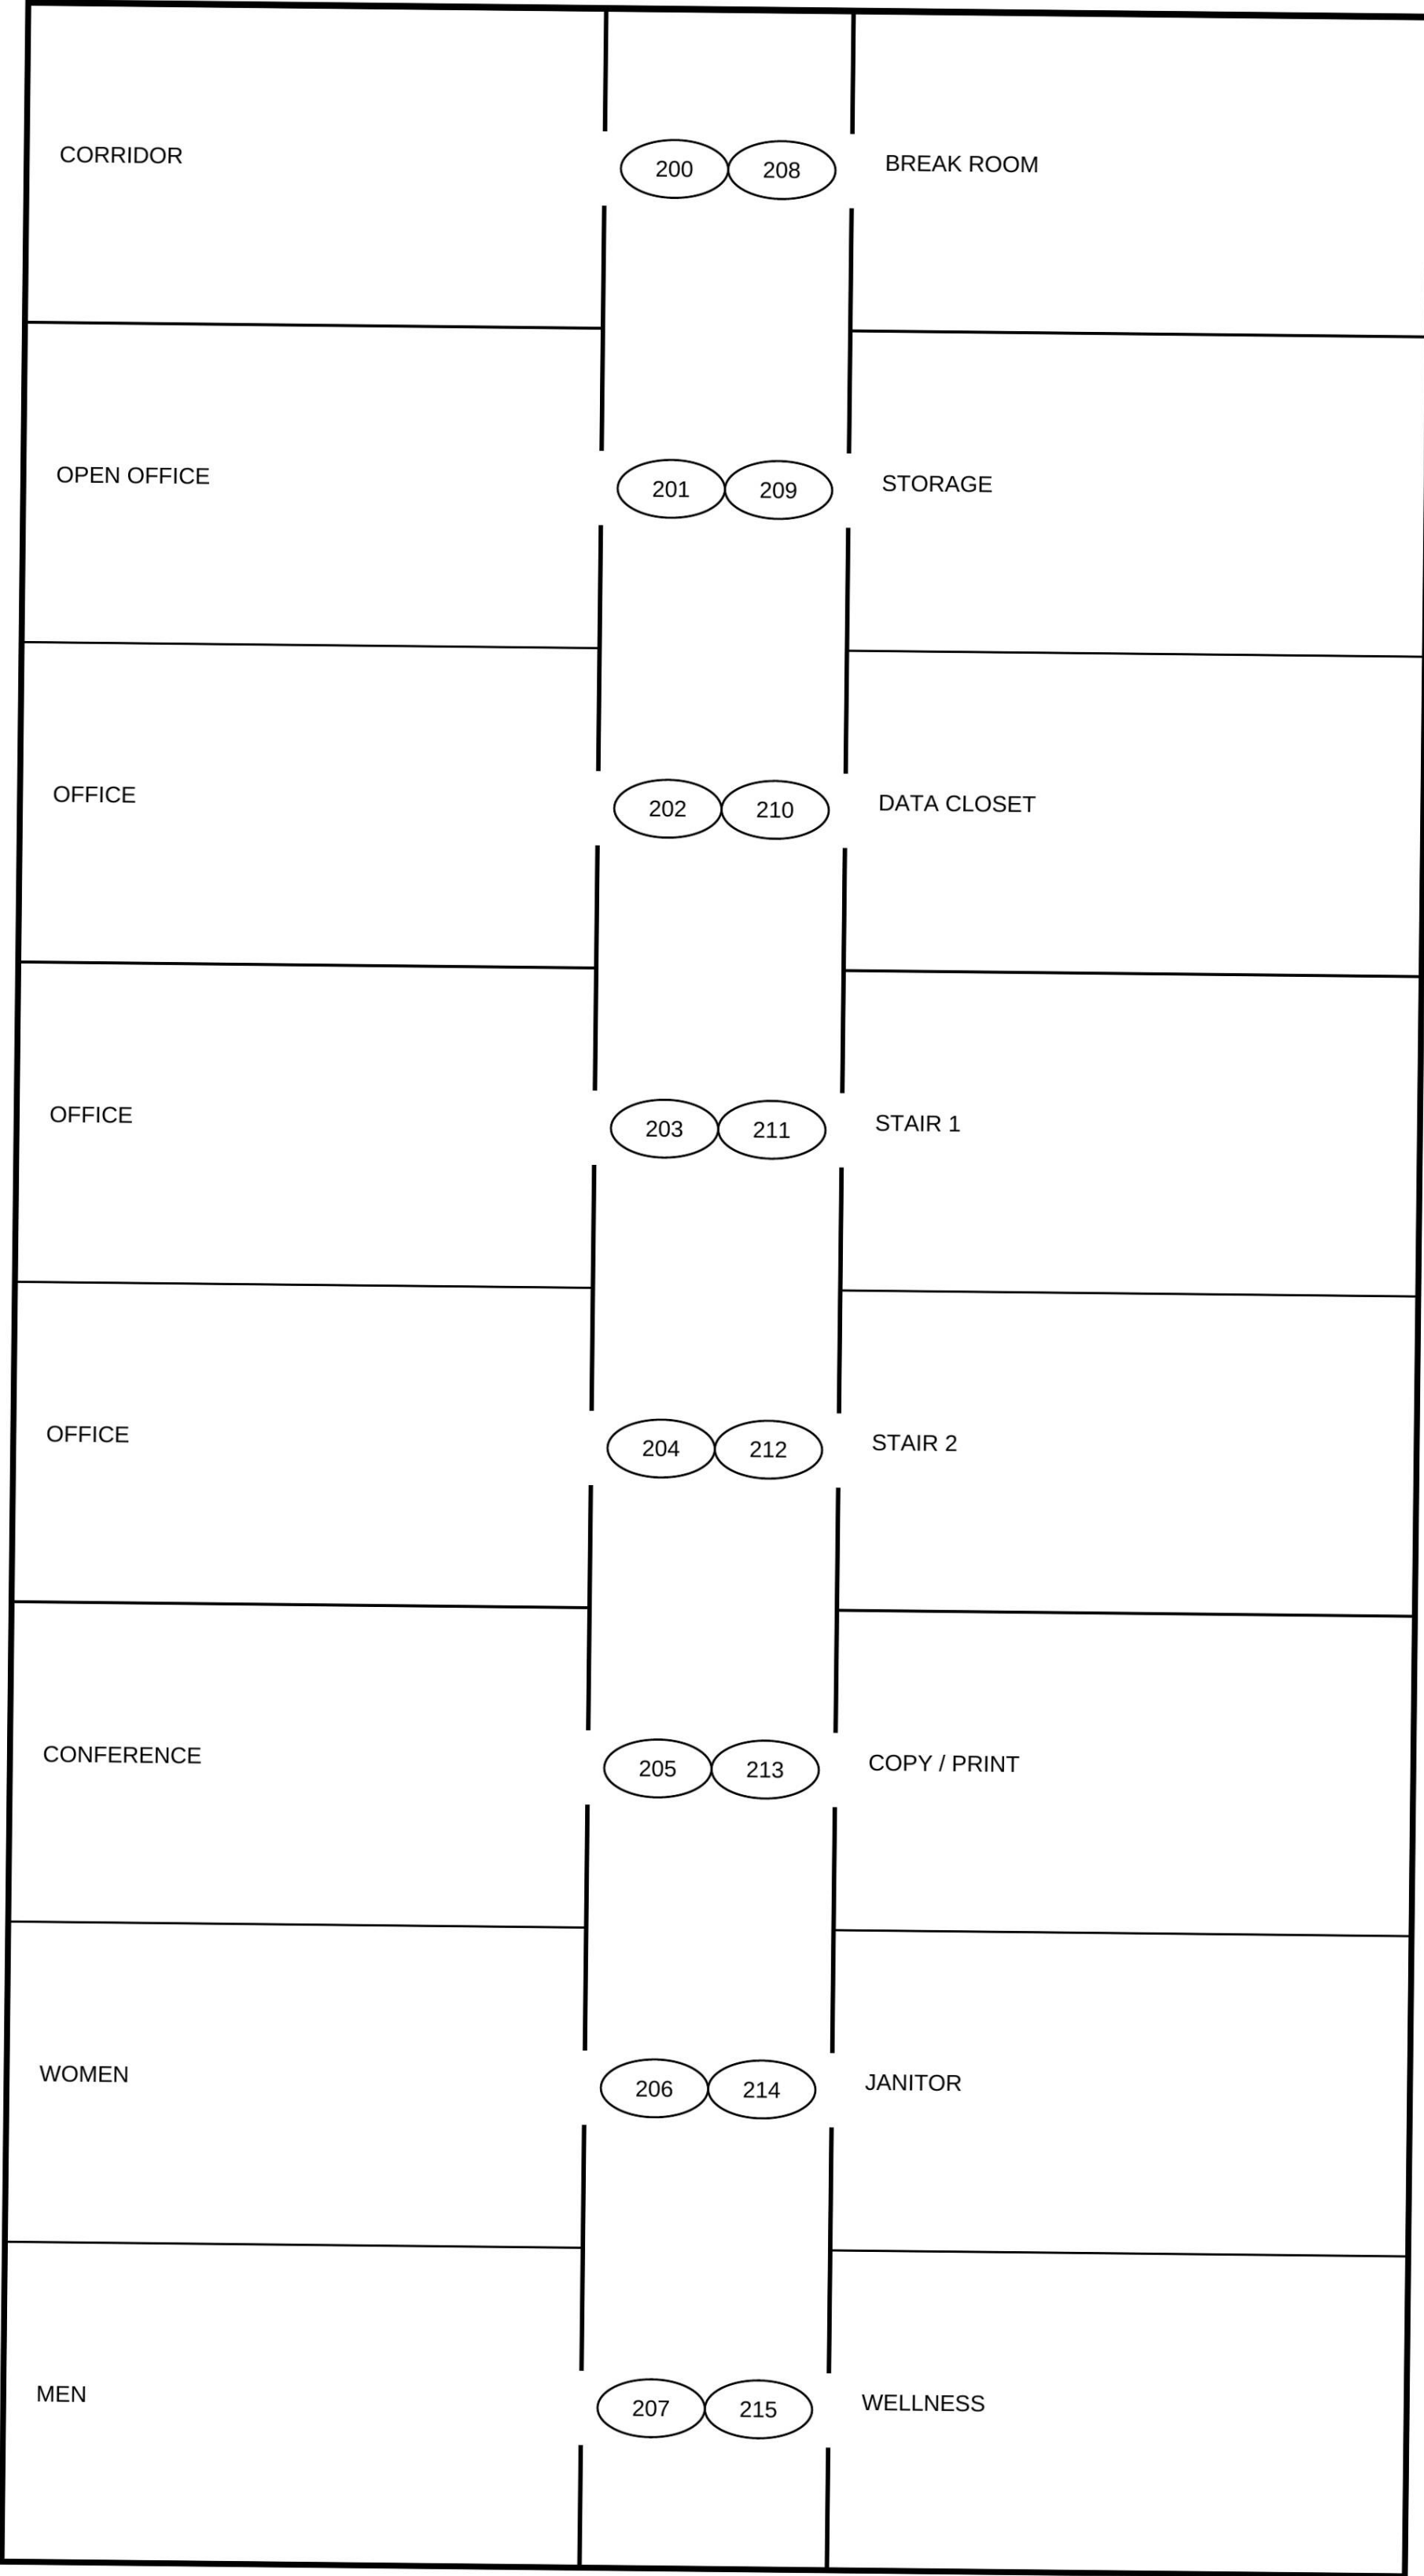

SECOND FLOOR PLAN

SCALE: 1/8" = 1'-0"

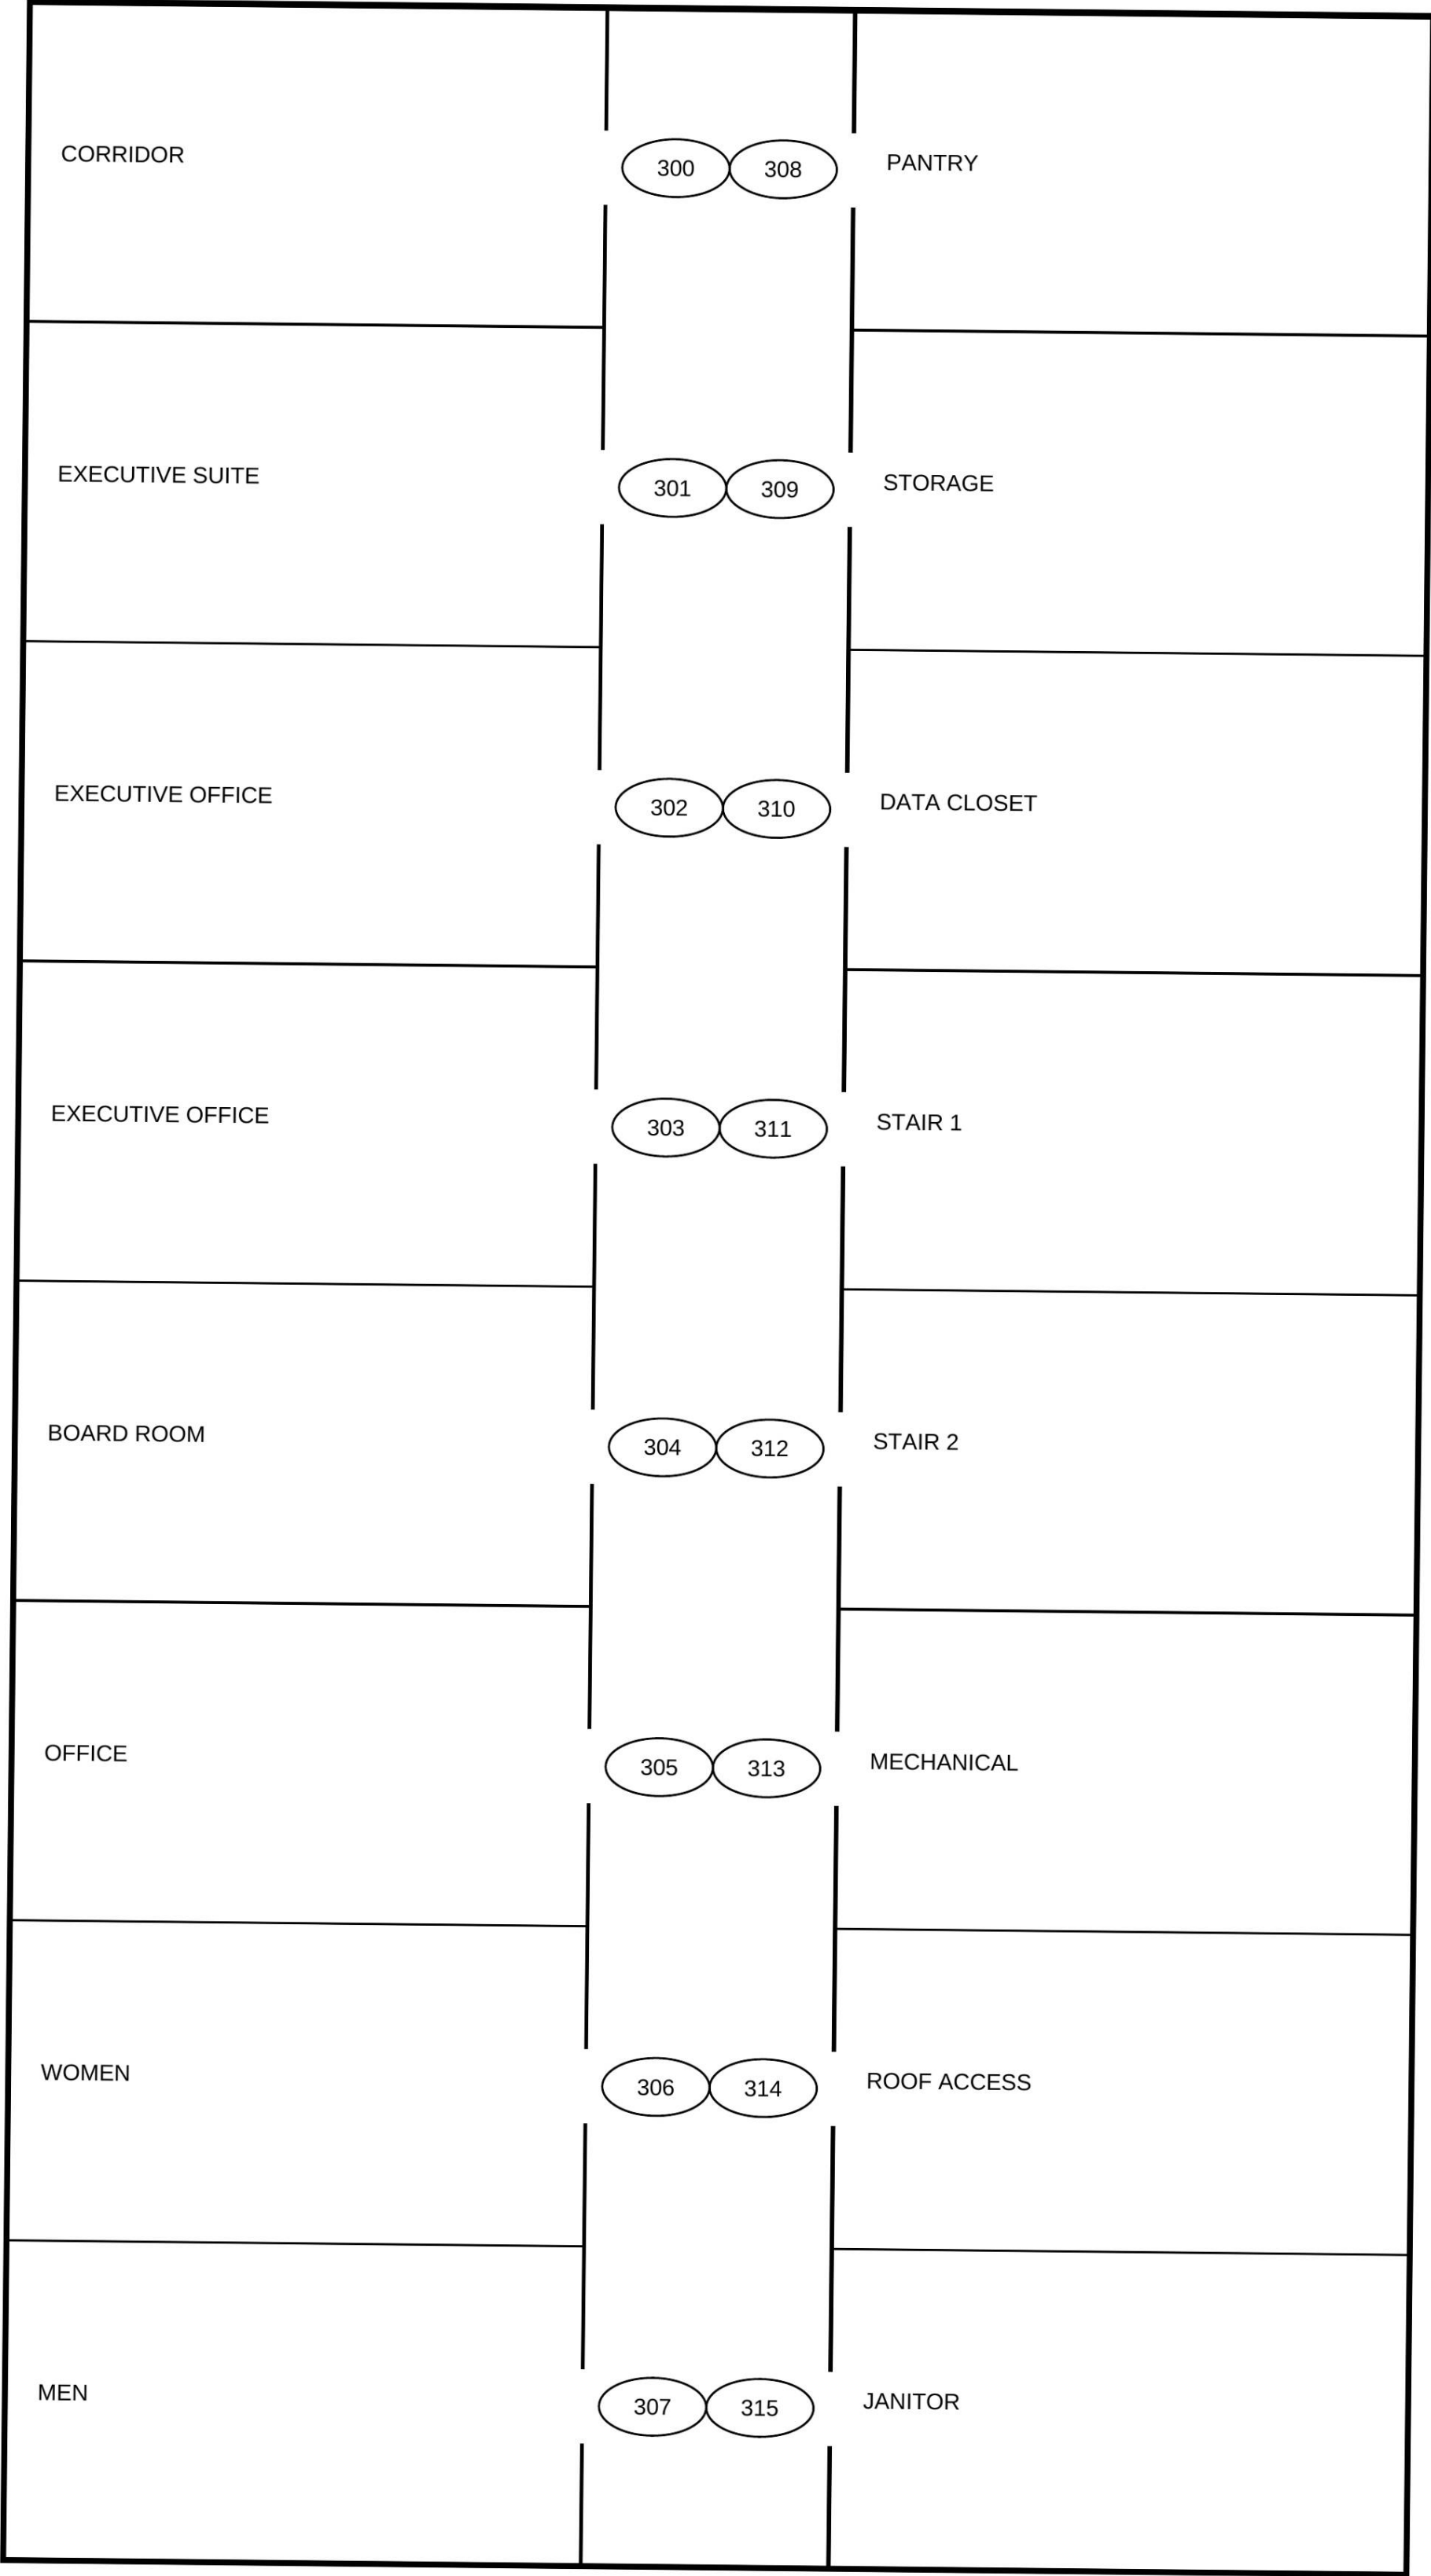

THIRD FLOOR PLAN

SCALE: 1/8" = 1'-0"

WeylandAI Sample Architects (fictional)

THE WEYLANDAI BUILDING

NEW CORPORATE HEADQUARTERS
4400 Bluestem Parkway, Austin, TX

PROJECT NO. WAI-2026-01
BID SET 2026-10-09

FLOOR PLANS - DOOR TAGS

SHEET

A-101

SAMPLE PROJECT - NOT A REAL BUILDING

DOOR SCHEDULE

DOOR NO.	ROOM NAME	WIDTH	HEIGHT	THK	DOOR TYPE	DOOR MATL	FRAME TYPE	FRAME MATL	FIRE RATING	HW GROUP	REMARKS
100A	MAIN ENTRY	6'-0"	7'-0"	1 3/4"	F	AL	3	AL	-	01	PAIR
100B	VESTIBULE	3'-0"	7'-0"	1 3/4"	F	AL	3	AL	-	10	
101	LOBBY	3'-0"	7'-0"	1 3/4"	B	WD	1	HM	-	03	
102	RECEPTION OFFICE	3'-0"	7'-0"	1 3/4"	A	WD	1	HM	-	03	
103	CONFERENCE	3'-0"	7'-0"	1 3/4"	B	WD	1	HM	-	03	
104	OFFICE	3'-0"	7'-0"	1 3/4"	A	WD	1	HM	-	03	
105	OFFICE	3'-0"	7'-0"	1 3/4"	A	WD	1	HM	-	03	
106	WOMEN	3'-0"	7'-0"	1 3/4"	A	WD	1	HM	-	04	
107	MEN	3'-0"	7'-0"	1 3/4"	A	WD	1	HM	-	04	
108	BREAK ROOM	3'-0"	7'-0"	1 3/4"	A	WD	1	HM	-	08	
109	STORAGE	3'-0"	7'-0"	1 3/4"	A	HM	1	HM	-	05	
110	IT / SERVER	3'-0"	7'-0"	1 3/4"	A	HM	1	HM	60 MIN	06	
111	CORRIDOR	6'-0"	7'-0"	1 3/4"	B	WD	2	HM	20 MIN	07	PAIR
112	STAIR 1	3'-0"	7'-0"	1 3/4"	A	HM	1	HM	90 MIN	02	
113	STAIR 2	3'-0"	7'-0"	1 3/4"	A	HM	1	HM	90 MIN	02	
114	JANITOR	3'-0"	7'-0"	1 3/4"	A	HM	1	HM	-	05	
200	CORRIDOR	6'-0"	7'-0"	1 3/4"	B	WD	2	HM	20 MIN	07	PAIR
201	OPEN OFFICE	3'-0"	7'-0"	1 3/4"	B	WD	1	HM	-	03	
202	OFFICE	3'-0"	7'-0"	1 3/4"	A	WD	1	HM	-	03	
203	OFFICE	3'-0"	7'-0"	1 3/4"	A	WD	1	HM	-	03	
204	OFFICE	3'-0"	7'-0"	1 3/4"	A	WD	1	HM	-	03	
205	CONFERENCE	3'-0"	7'-0"	1 3/4"	B	WD	1	HM	-	03	
206	WOMEN	3'-0"	7'-0"	1 3/4"	A	WD	1	HM	-	04	
207	MEN	3'-0"	7'-0"	1 3/4"	A	WD	1	HM	-	04	
208	BREAK ROOM	3'-0"	7'-0"	1 3/4"	A	WD	1	HM	-	04	
209	STORAGE	3'-0"	7'-0"	1 3/4"	A	HM	1	HM	-	08	
210	DATA CLOSET	3'-0"	7'-0"	1 3/4"	A	HM	1	HM	60 MIN	06	
211	STAIR 1	3'-0"	7'-0"	1 3/4"	A	HM	1	HM	90 MIN	02	
212	STAIR 2	3'-0"	7'-0"	1 3/4"	A	HM	1	HM	90 MIN	02	
213	COPY / PRINT	3'-0"	7'-0"	1 3/4"	A	WD	1	HM	90 MIN	02	
214	JANITOR	3'-0"	7'-0"	1 3/4"	A	HM	1	HM	-	03	
215	WELLNESS	3'-0"	7'-0"	1 3/4"	A	WD	1	HM	-	05	
300	CORRIDOR	6'-0"	7'-0"	1 3/4"	B	WD	2	HM	20 MIN	07	PAIR
301	EXECUTIVE SUITE	3'-0"	7'-0"	1 3/4"	B	WD	1	HM	-	03	
302	EXECUTIVE OFFICE	3'-0"	7'-0"	1 3/4"	A	WD	1	HM	-	03	
303	EXECUTIVE OFFICE	3'-0"	7'-0"	1 3/4"	A	WD	1	HM	-	03	
304	BOARD ROOM	3'-0"	7'-0"	1 3/4"	B	WD	1	HM	-	03	
305	OFFICE	3'-0"	7'-0"	1 3/4"	A	WD	1	HM	-	03	
306	WOMEN	3'-0"	7'-0"	1 3/4"	A	WD	1	HM	-	04	
307	MEN	3'-0"	7'-0"	1 3/4"	A	WD	1	HM	-	04	
308	PANTRY	3'-0"	7'-0"	1 3/4"	A	WD	1	HM	-	08	
309	STORAGE	3'-0"	7'-0"	1 3/4"	A	HM	1	HM	-	05	
310	DATA CLOSET	3'-0"	7'-0"	1 3/4"	A	HM	1	HM	60 MIN	06	
311	STAIR 1	3'-0"	7'-0"	1 3/4"	A	HM	1	HM	90 MIN	02	
312	STAIR 2	3'-0"	7'-0"	1 3/4"	A	HM	1	HM	90 MIN	02	
313	MECHANICAL	3'-0"	7'-0"	1 3/4"	A	HM	1	HM	60 MIN	05	
314	ROOF ACCESS	3'-0"	7'-0"	1 3/4"	A	HM	1	HM	-	09	
315	JANITOR	3'-0"	7'-0"	1 3/4"	A	HM	1	HM	-	05	

WeylandAI Sample Architects (fictional)

THE WEYLANDAI BUILDING
NEW CORPORATE HEADQUARTERS
4400 Bluesiem Parkway, Austin, TX
PROJECT NO. WAI-2026-01
BID SET 2026-10-09

HARDWARE: SEE SECTION 08 71 00

DOOR TYPES
A - FLUSH
B - HALF GLASS
F - FULL GLASS (STOREFRONT)

MATERIALS
WD - SOLID CORE WOOD
HM - HOLLOW METAL
AL - ALUMINUM

DOOR SCHEDULE

SHEET

A-601

SAMPLE PROJECT - NOT A REAL BUILDING

SAMPLE PROJECT - NOT A REAL BUILDING

The WeylandAI Building - WAI-2026-01

SECTION 08 71 00 - DOOR HARDWARE

SECTION 08 71 00 - DOOR HARDWARE

PART 3 - EXECUTION

3.1 HARDWARE GROUPS

A. Provide each opening with the hardware listed in its group.

Hardware Group No. 01 MAIN ENTRY PAIR

100A

QTY		DESCRIPTION	CATALOG NUMBER	FINISH	MFR
2	EA	CONTINUOUS HINGE	SL11 HD	628	SEL
2	EA	EXIT DEVICE	99-L-F	626	VON
1	EA	RIM CYLINDER	20-057-ICX	626	SCH
2	EA	SURFACE CLOSER	4040XP EDA	689	LCN
2	EA	KICK PLATE	8400 10" X 34" B-CS	630	IVE
1	EA	GASKETING	188S-BK	BK	ZER
2	EA	DOOR SWEEP	328A	AA	ZER

Hardware Group No. 02 STAIR

112 113 211 212 311 312

QTY		DESCRIPTION	CATALOG NUMBER	FINISH	MFR
3	EA	HINGE	5BB1HW 4.5 X 4.5	652	IVE
1	EA	FIRE EXIT DEVICE	99-EO-F	626	VON
1	EA	SURFACE CLOSER	4040XP REG	689	LCN
1	EA	KICK PLATE	8400 10" X 34" B-CS	630	IVE
1	EA	GASKETING	188S-BK	BK	ZER

Hardware Group No. 03 OFFICE

101 102 103 104 105 201
202 203 204 205 213 301
302 303 304 305

QTY		DESCRIPTION	CATALOG NUMBER	FINISH	MFR
3	EA	HINGE	5BB1HW 4.5 X 4.5	652	IVE
1	EA	ENTRANCE LOCK	ALX53R RHO	626	SCH
1	EA	WALL STOP	WS406/407CCV	630	IVE
3	EA	SILENCER	SR64	GRY	IVE

SAMPLE PROJECT - NOT A REAL BUILDING

The WeylandAI Building - WAI-2026-01

SECTION 08 71 00 - DOOR HARDWARE

Hardware Group No. 04 RESTROOM

106 107 206 207 215 306
307

QTY		DESCRIPTION	CATALOG NUMBER	FINISH	MFR
1	EA	CONTINUOUS HINGE	SL11 HD	628	SEL
1	EA	PRIVACY LOCK W/ INDICATOR	ND40S RHO OS-OCC	626	SCH
1	EA	SURFACE CLOSER	4040XP REG	689	LCN
1	EA	KICK PLATE	8400 10" X 34" B-CS	630	IVE
1	EA	WALL STOP	WS406/407CCV	630	IVE
3	EA	SILENCER	SR64	GRY	IVE

Hardware Group No. 05 STORAGE

109 114 209 214 309 313
315

QTY		DESCRIPTION	CATALOG NUMBER	FINISH	MFR
3	EA	HINGE	5BB1HW 4.5 X 4.5	652	IVE
1	EA	STOREROOM LOCK	ALX80R RHO	626	SCH
1	EA	OVERHEAD STOP	90S	630	GLY
3	EA	SILENCER	SR64	GRY	IVE

Hardware Group No. 06 IT ROOM

110 210 310

QTY		DESCRIPTION	CATALOG NUMBER	FINISH	MFR
3	EA	HINGE	5BB1HW 4.5 X 4.5	652	IVE
1	EA	STOREROOM LOCK	ALX80R RHO	626	SCH
1	EA	ELECTRIC STRIKE	6223 FSE 24VDC	630	VON
1	EA	SURFACE CLOSER	4040XP REG	689	LCN
1	EA	CARD READER	BY DIVISION 28		B/O
3	EA	SILENCER	SR64	GRY	IVE

Hardware Group No. 07 CORRIDOR PAIR

111 200 300

QTY		DESCRIPTION	CATALOG NUMBER	FINISH	MFR
2	EA	CONTINUOUS HINGE	SL11 HD	628	SEL
2	EA	FLUSH BOLT	FB51P	630	IVE
1	EA	DUST PROOF STRIKE	DP1	626	IVE
1	EA	STOREROOM LOCK	ALX80R RHO	626	SCH
2	EA	SURFACE CLOSER	4040XP REG	689	LCN
2	EA	KICK PLATE	8400 10" X 34" B-CS	630	IVE
1	EA	GASKETING	188S-BK	BK	ZER

SAMPLE PROJECT - NOT A REAL BUILDING

The WeylandAI Building - WAI-2026-01

SECTION 08 71 00 - DOOR HARDWARE

Hardware Group No. 08 BREAK ROOM

108 208 308

QTY		DESCRIPTION	CATALOG NUMBER	FINISH	MFR
3	EA	HINGE	5BB1HW 4.5 X 4.5	652	IVE
1	EA	PUSH PLATE	8200 4" X 16"	630	IVE
1	EA	PULL	8302 10" 4" X 16"	630	IVE
1	EA	SURFACE CLOSER	4040XP REG	689	LCN
1	EA	WALL STOP	WS406/407CCV	630	IVE

Hardware Group No. 09 ROOF ACCESS

314

QTY		DESCRIPTION	CATALOG NUMBER	FINISH	MFR
1	EA	CONTINUOUS HINGE	SL57 HD	628	SEL
1	EA	EXIT DEVICE	99-EO	626	VON
1	EA	SURFACE CLOSER	4040XP EDA	689	LCN
1	EA	GASKETING	188S-BK	BK	ZER
1	EA	DOOR SWEEP	328A	AA	ZER

Hardware Group No. 10 VESTIBULE

100B

QTY		DESCRIPTION	CATALOG NUMBER	FINISH	MFR
1	EA	CONTINUOUS HINGE	SL11 HD	628	SEL
1	EA	EXIT DEVICE	99-L-F	626	VON
1	EA	POWER TRANSFER	EPT10	689	VON
1	EA	SURFACE CLOSER	4040SE	689	LCN
1	EA	PULL	8190HD 10" O	630	IVE

END OF SECTION 08 71 00