

# THE WEYLANDAI BUILDING

NEW CORPORATE HEADQUARTERS - BID SET

4400 Bluestem Parkway, Austin, TX

## SHEET INDEX

|          |                                |
|----------|--------------------------------|
| G-001    | COVER SHEET                    |
| A-101    | FLOOR PLANS - DOOR TAGS        |
| A-601    | DOOR SCHEDULE                  |
| 08 71 00 | DOOR HARDWARE (PROJECT MANUAL) |

WeylandAI Sample Architects (fictional)

## THE WEYLANDAI BUILDING

NEW CORPORATE HEADQUARTERS  
4400 Bluestem Parkway, Austin, TX

PROJECT NO. WAI-2026-01  
BID SET 2026-10-09

## COVER SHEET

SHEET

# G-001

SAMPLE PROJECT - NOT A REAL BUILDING

THE WEYLANDAI BUILDING


NEW CORPORATE HEADQUARTERS  
4400 Bluestem Parkway, Austin, TX

PROJECT NO. WAI-2026-01  
BID SET 2026-10-09

FLOOR PLANS - DOOR TAGS


SHEET

A-101

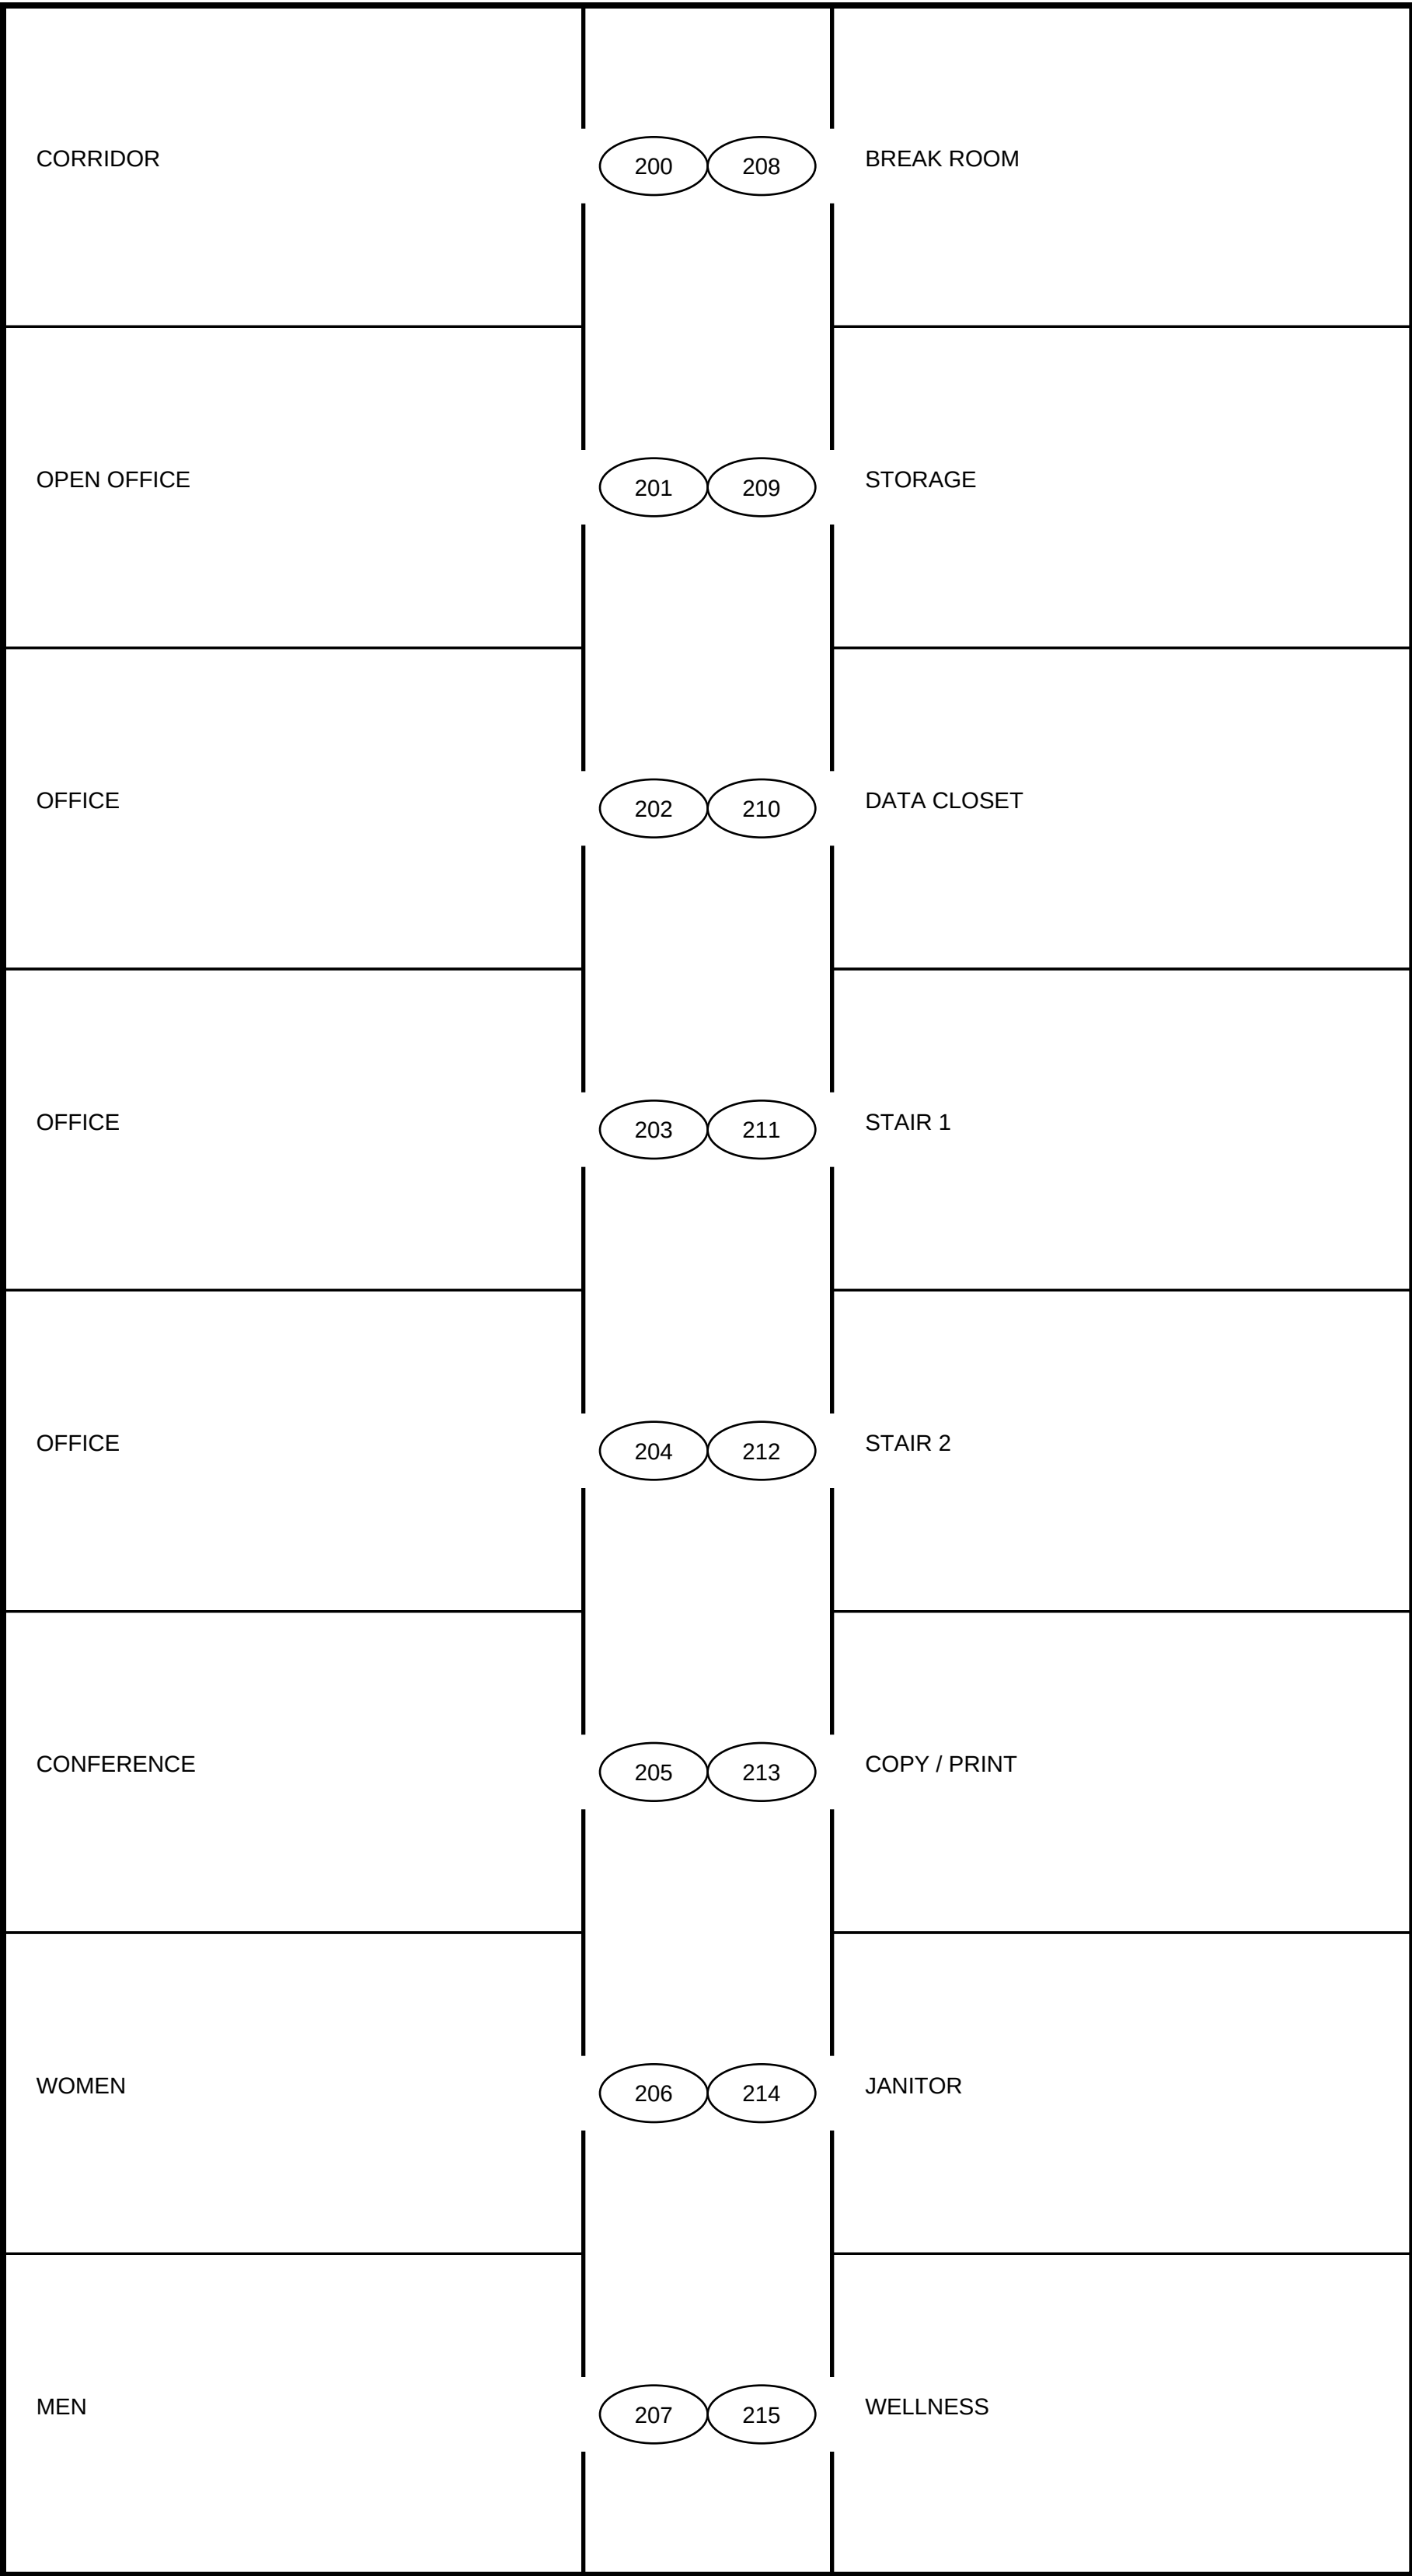


SECOND FLOOR PLAN

SCALE: 1/8" = 1'-0"

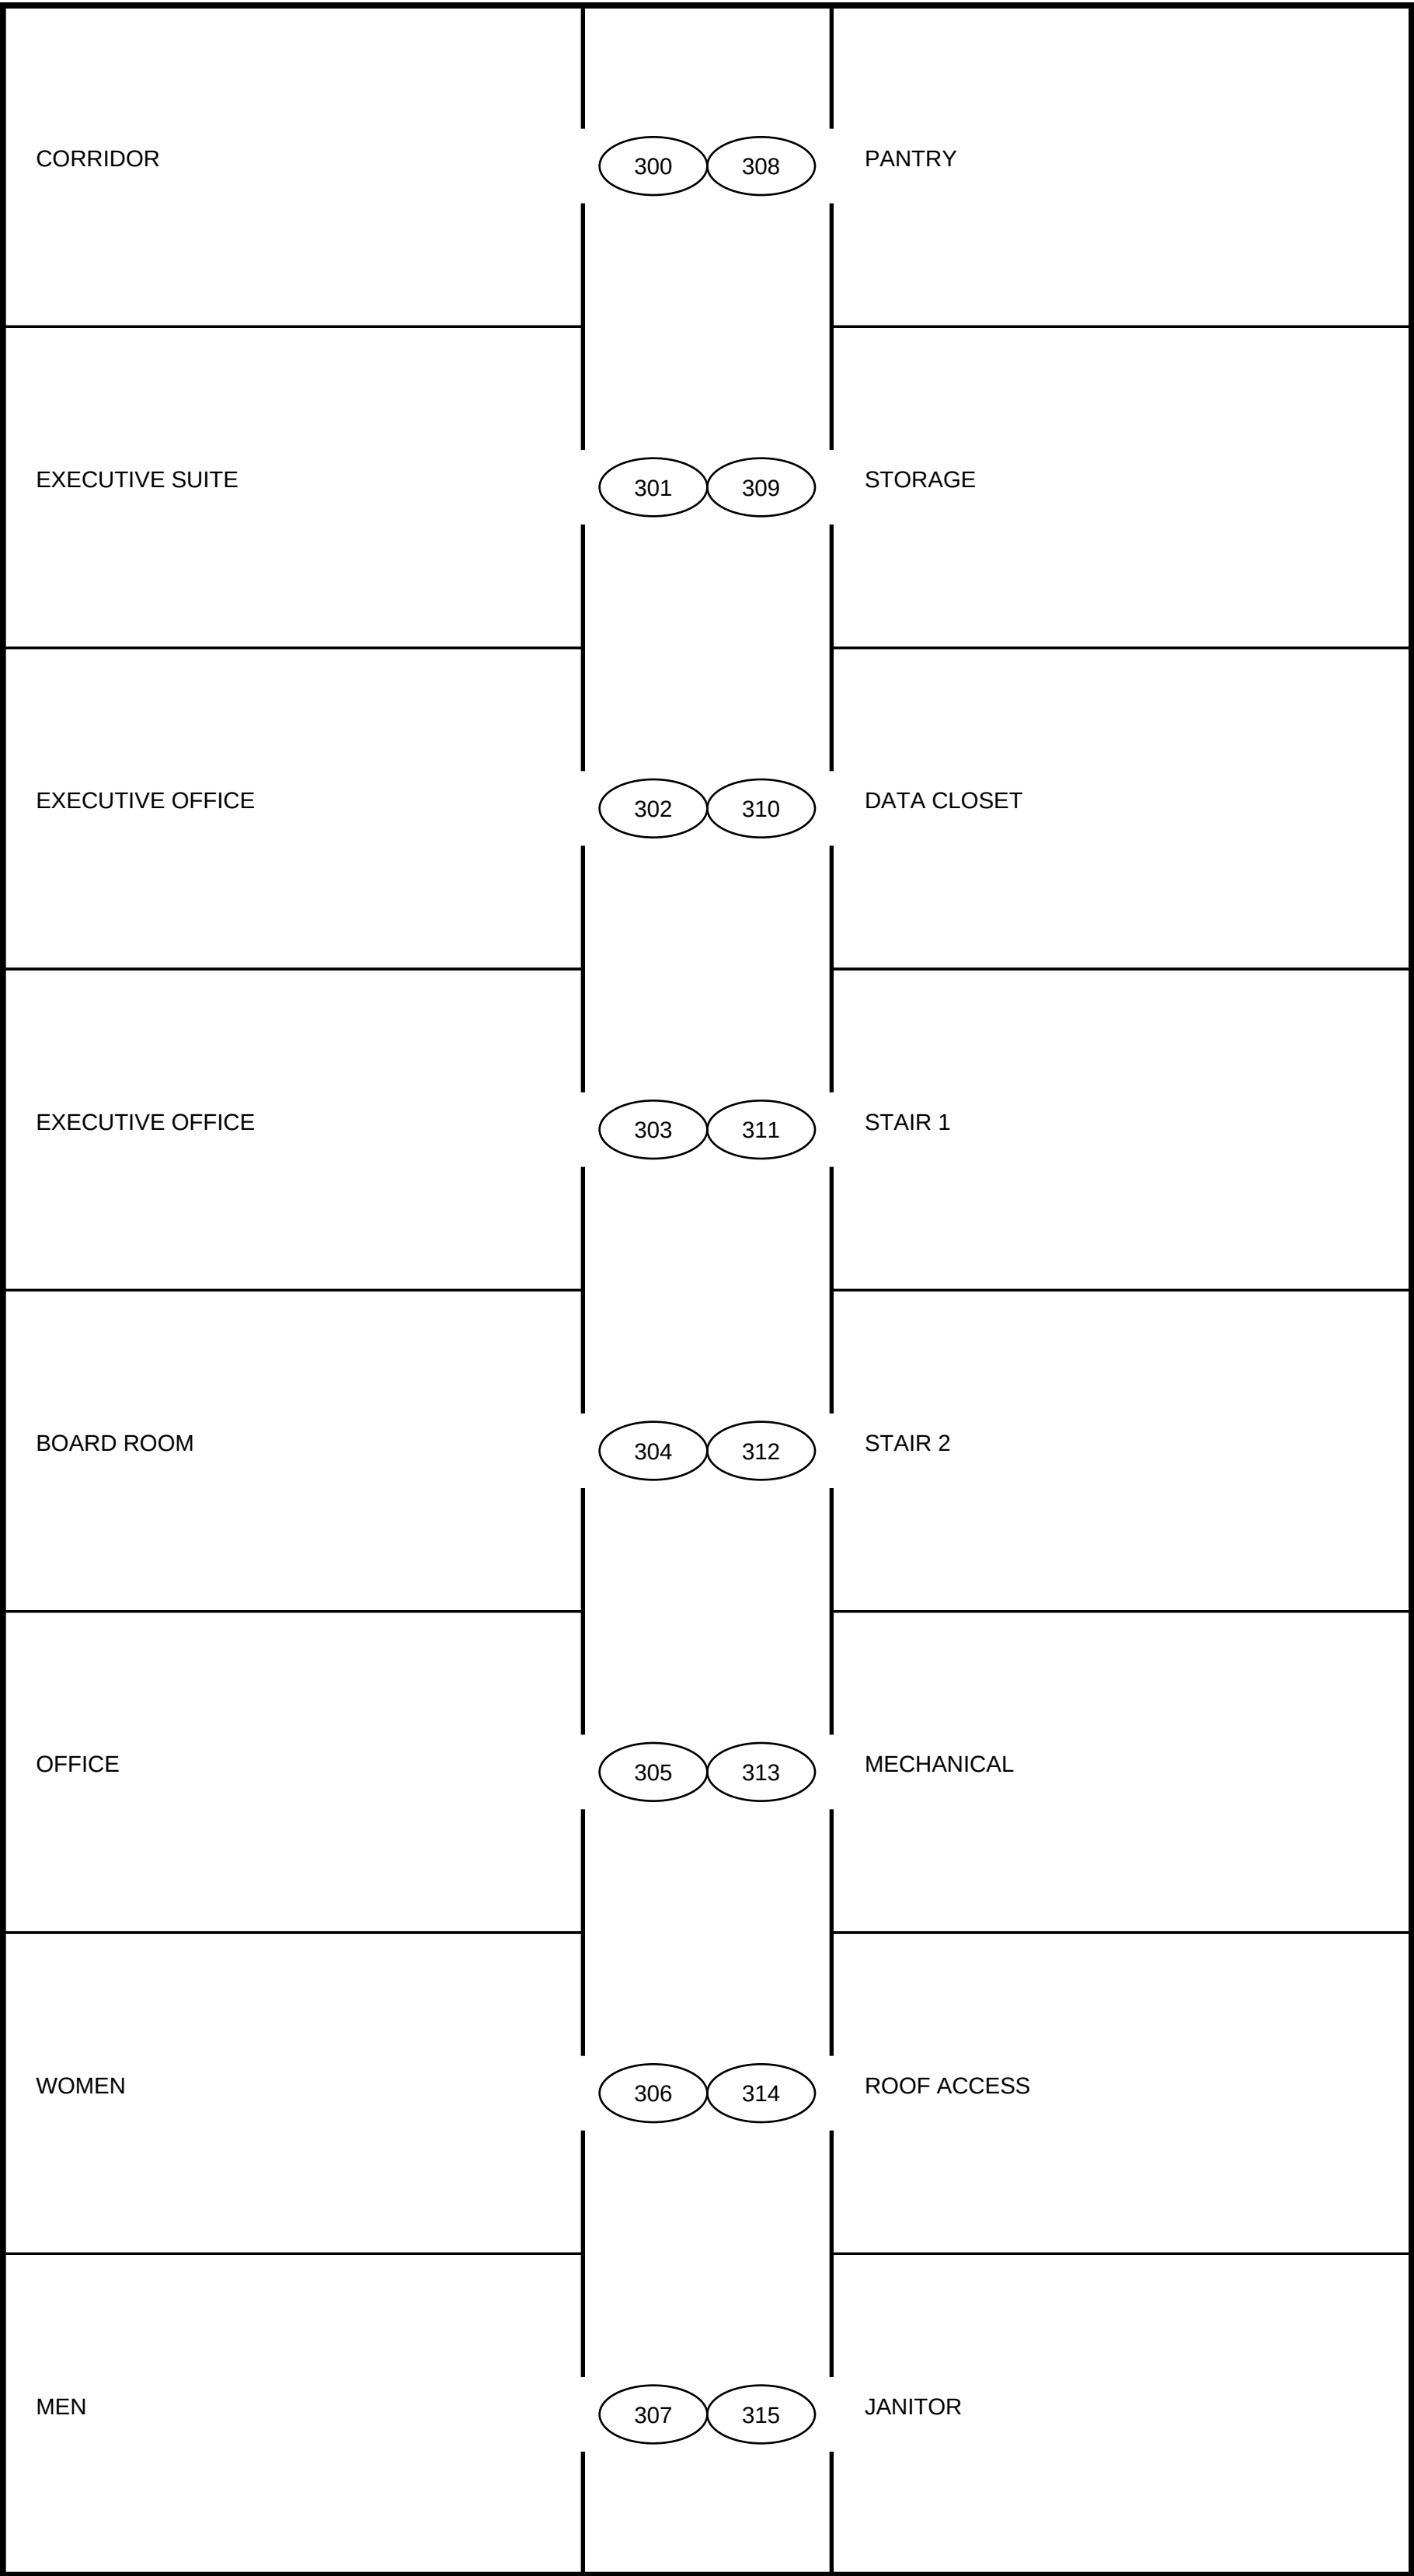

THIRD FLOOR PLAN

SCALE: 1/8" = 1'-0"

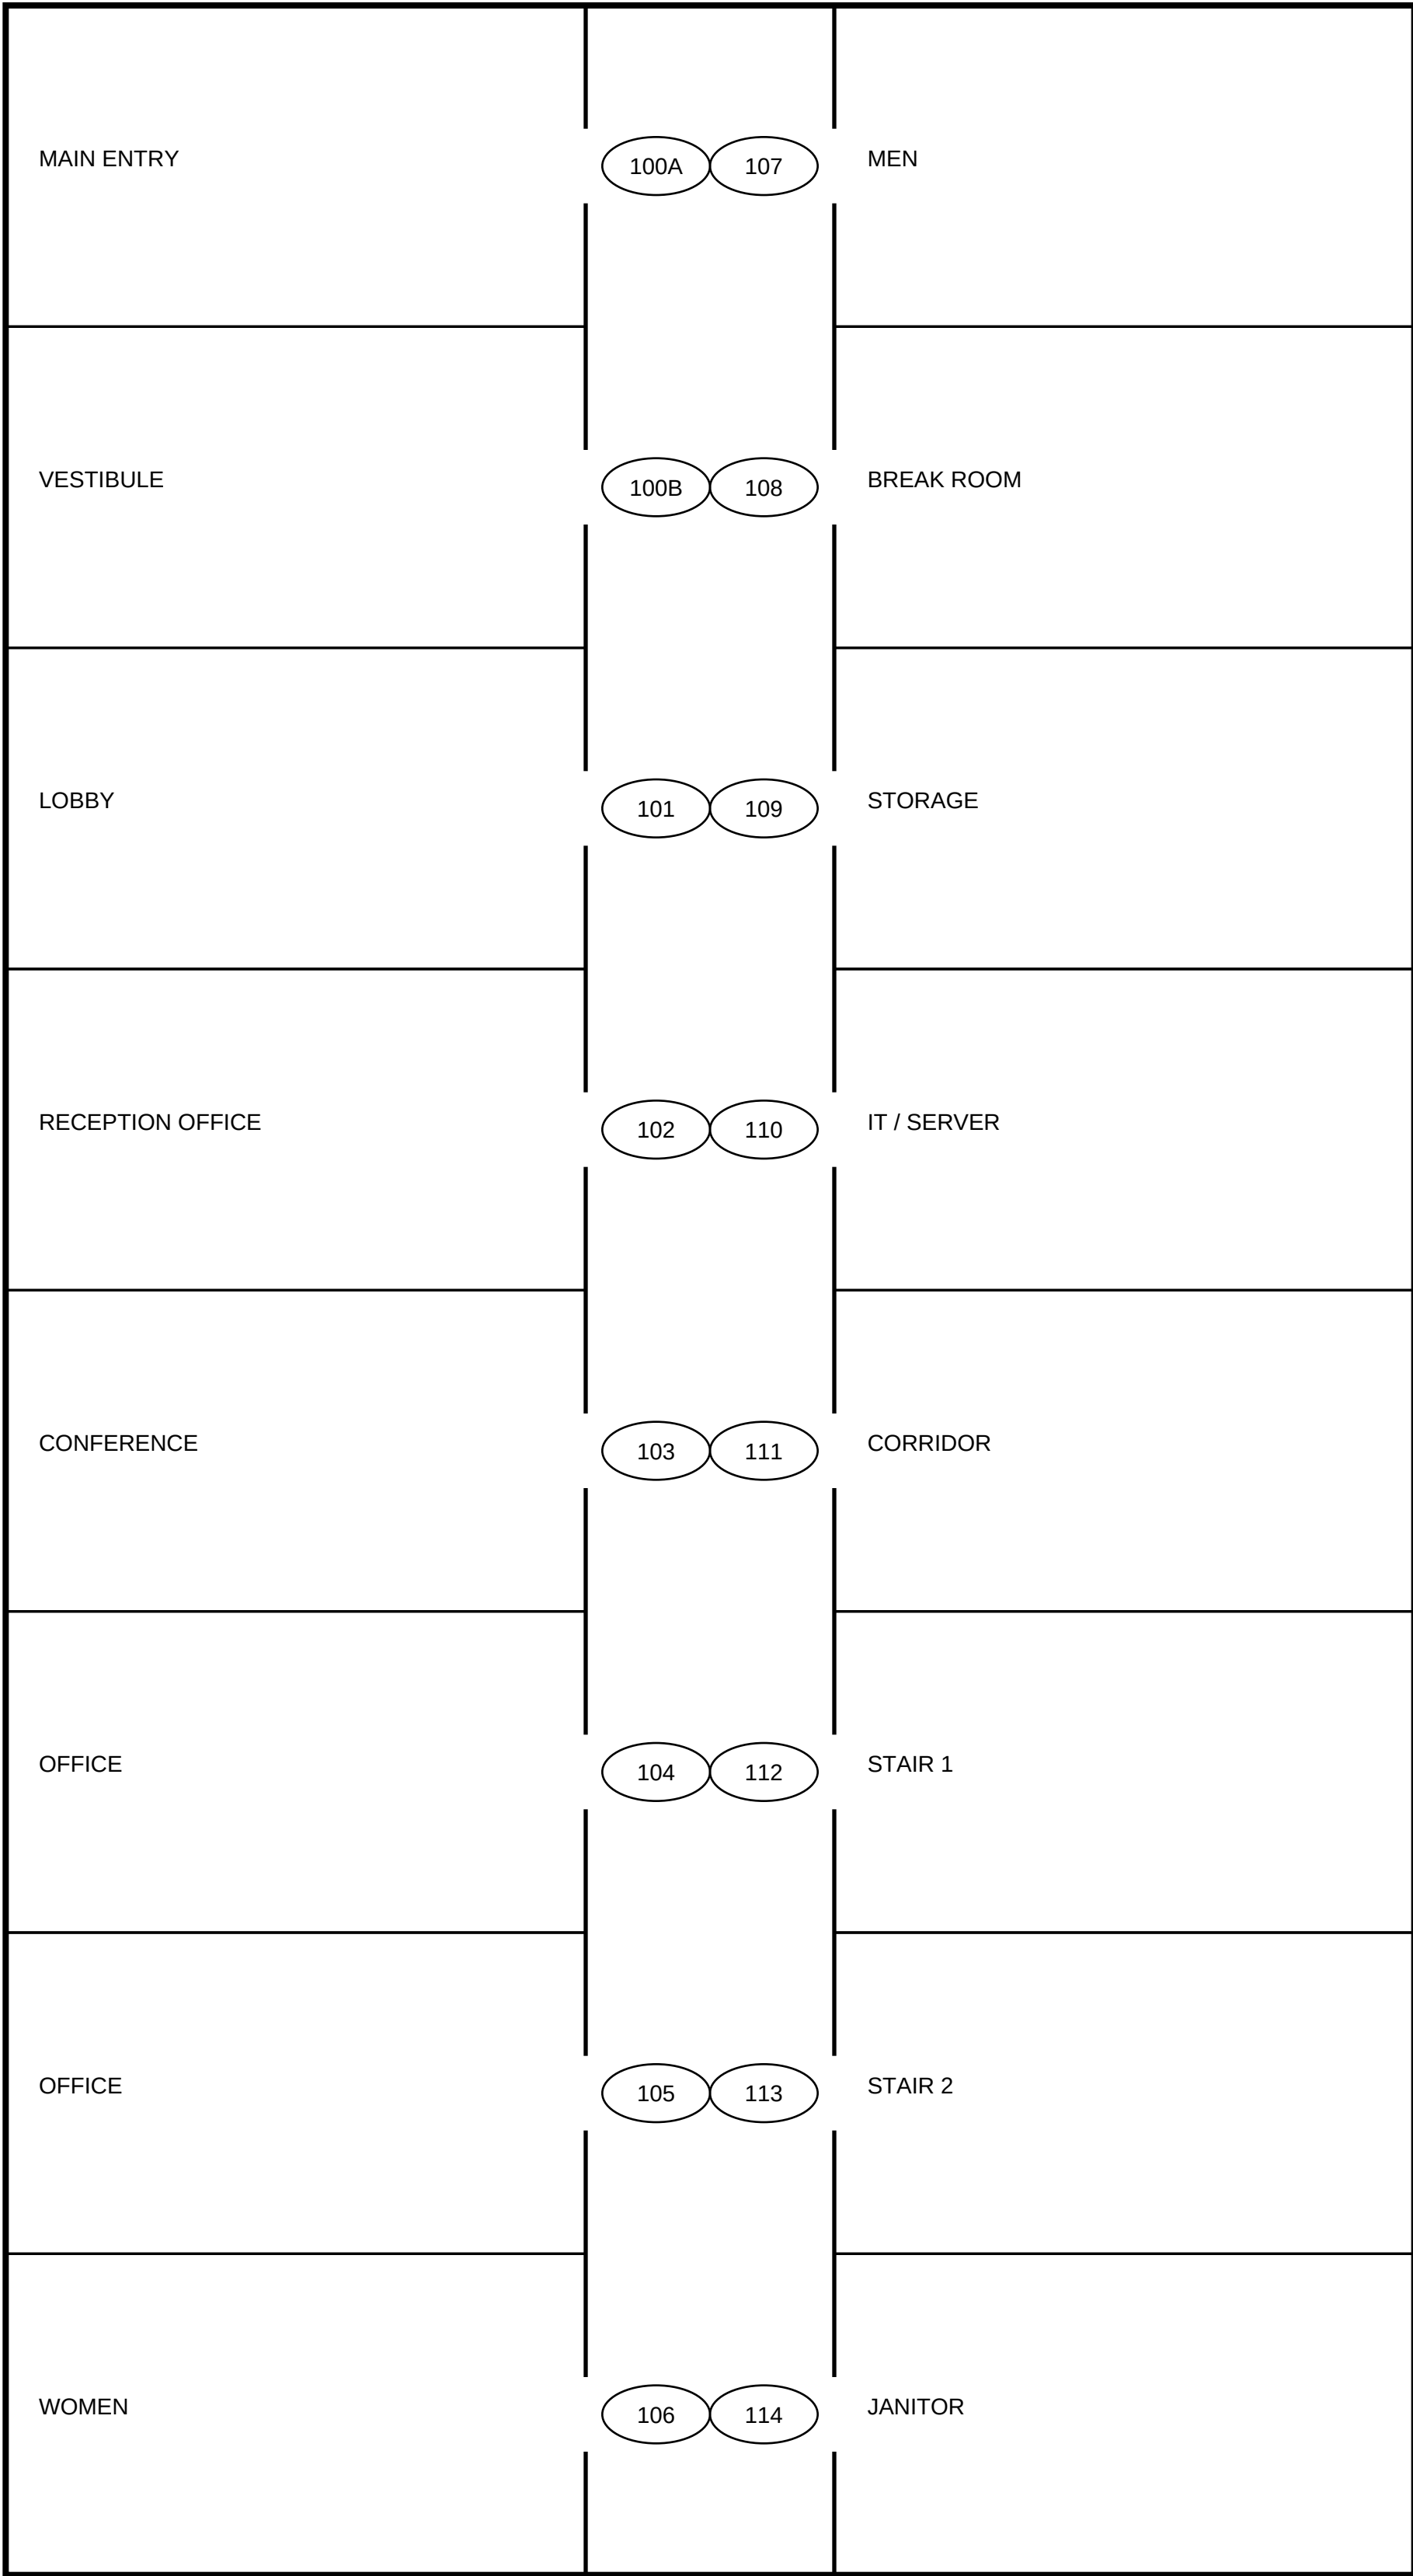

FIRST FLOOR PLAN

SCALE: 1/8" = 1'-0"

DOOR SCHEDULE

| DOOR NO. | ROOM NAME        | WIDTH | HEIGHT | THK    | DOOR TYPE | DOOR MATL | FRAME TYPE | FRAME MATL | FIRE RATING | HW GROUP | REMARKS |
|----------|------------------|-------|--------|--------|-----------|-----------|------------|------------|-------------|----------|---------|
| 100A     | MAIN ENTRY       | 6'-0" | 7'-0"  | 1 3/4" | F         | AL        | 3          | AL         | -           | 01       | PAIR    |
| 100B     | VESTIBULE        | 3'-0" | 7'-0"  | 1 3/4" | F         | AL        | 3          | AL         | -           | 10       |         |
| 101      | LOBBY            | 3'-0" | 7'-0"  | 1 3/4" | B         | WD        | 1          | HM         | -           | 03       |         |
| 102      | RECEPTION OFFICE | 3'-0" | 7'-0"  | 1 3/4" | A         | WD        | 1          | HM         | -           | 03       |         |
| 103      | CONFERENCE       | 3'-0" | 7'-0"  | 1 3/4" | B         | WD        | 1          | HM         | -           | 03       |         |
| 104      | OFFICE           | 3'-0" | 7'-0"  | 1 3/4" | A         | WD        | 1          | HM         | -           | 03       |         |
| 105      | OFFICE           | 3'-0" | 7'-0"  | 1 3/4" | A         | WD        | 1          | HM         | -           | 03       |         |
| 106      | WOMEN            | 3'-0" | 7'-0"  | 1 3/4" | A         | WD        | 1          | HM         | -           | 04       |         |
| 107      | MEN              | 3'-0" | 7'-0"  | 1 3/4" | A         | WD        | 1          | HM         | -           | 04       |         |
| 108      | BREAK ROOM       | 3'-0" | 7'-0"  | 1 3/4" | A         | WD        | 1          | HM         | -           | 08       |         |
| 109      | STORAGE          | 3'-0" | 7'-0"  | 1 3/4" | A         | HM        | 1          | HM         | -           | 05       |         |
| 110      | IT / SERVER      | 3'-0" | 7'-0"  | 1 3/4" | A         | HM        | 1          | HM         | 60 MIN      | 06       |         |
| 111      | CORRIDOR         | 6'-0" | 7'-0"  | 1 3/4" | B         | WD        | 2          | HM         | 20 MIN      | 07       | PAIR    |
| 112      | STAIR 1          | 3'-0" | 7'-0"  | 1 3/4" | A         | HM        | 1          | HM         | 90 MIN      | 02       |         |
| 113      | STAIR 2          | 3'-0" | 7'-0"  | 1 3/4" | A         | HM        | 1          | HM         | 90 MIN      | 02       |         |
| 114      | JANITOR          | 3'-0" | 7'-0"  | 1 3/4" | A         | HM        | 1          | HM         | -           | 05       |         |
| 200      | CORRIDOR         | 6'-0" | 7'-0"  | 1 3/4" | B         | WD        | 2          | HM         | 20 MIN      | 07       | PAIR    |
| 201      | OPEN OFFICE      | 3'-0" | 7'-0"  | 1 3/4" | B         | WD        | 1          | HM         | -           | 03       |         |
| 202      | OFFICE           | 3'-0" | 7'-0"  | 1 3/4" | A         | WD        | 1          | HM         | -           | 03       |         |
| 203      | OFFICE           | 3'-0" | 7'-0"  | 1 3/4" | A         | WD        | 1          | HM         | -           | 03       |         |
| 204      | OFFICE           | 3'-0" | 7'-0"  | 1 3/4" | A         | WD        | 1          | HM         | -           | 03       |         |
| 205      | CONFERENCE       | 3'-0" | 7'-0"  | 1 3/4" | B         | WD        | 1          | HM         | -           | 03       |         |
| 206      | WOMEN            | 3'-0" | 7'-0"  | 1 3/4" | A         | WD        | 1          | HM         | -           | 04       |         |
| 207      | MEN              | 3'-0" | 7'-0"  | 1 3/4" | A         | WD        | 1          | HM         | -           | 04       |         |
| 208      | BREAK ROOM       | 3'-0" | 7'-0"  | 1 3/4" | A         | WD        | 1          | HM         | -           | 08       |         |
| 209      | STORAGE          | 3'-0" | 7'-0"  | 1 3/4" | A         | HM        | 1          | HM         | -           | 05       |         |
| 210      | DATA CLOSET      | 3'-0" | 7'-0"  | 1 3/4" | A         | HM        | 1          | HM         | 60 MIN      | 06       |         |
| 211      | STAIR 1          | 3'-0" | 7'-0"  | 1 3/4" | A         | HM        | 1          | HM         | 90 MIN      | 02       |         |
| 212      | STAIR 2          | 3'-0" | 7'-0"  | 1 3/4" | A         | HM        | 1          | HM         | 90 MIN      | 02       |         |
| 213      | COPY / PRINT     | 3'-0" | 7'-0"  | 1 3/4" | A         | WD        | 1          | HM         | -           | 03       |         |
| 214      | JANITOR          | 3'-0" | 7'-0"  | 1 3/4" | A         | HM        | 1          | HM         | -           | 05       |         |
| 215      | WELLNESS         | 3'-0" | 7'-0"  | 1 3/4" | A         | WD        | 1          | HM         | -           | 04       |         |
| 300      | CORRIDOR         | 6'-0" | 7'-0"  | 1 3/4" | B         | WD        | 2          | HM         | 20 MIN      | 07       | PAIR    |
| 301      | EXECUTIVE SUITE  | 3'-0" | 7'-0"  | 1 3/4" | B         | WD        | 1          | HM         | -           | 03       |         |
| 302      | EXECUTIVE OFFICE | 3'-0" | 7'-0"  | 1 3/4" | A         | WD        | 1          | HM         | -           | 03       |         |
| 303      | EXECUTIVE OFFICE | 3'-0" | 7'-0"  | 1 3/4" | A         | WD        | 1          | HM         | -           | 03       |         |
| 304      | BOARD ROOM       | 3'-0" | 7'-0"  | 1 3/4" | B         | WD        | 1          | HM         | -           | 03       |         |
| 305      | OFFICE           | 3'-0" | 7'-0"  | 1 3/4" | A         | WD        | 1          | HM         | -           | 03       |         |
| 306      | WOMEN            | 3'-0" | 7'-0"  | 1 3/4" | A         | WD        | 1          | HM         | -           | 04       |         |
| 307      | MEN              | 3'-0" | 7'-0"  | 1 3/4" | A         | WD        | 1          | HM         | -           | 04       |         |
| 308      | PANTRY           | 3'-0" | 7'-0"  | 1 3/4" | A         | WD        | 1          | HM         | -           | 08       |         |
| 309      | STORAGE          | 3'-0" | 7'-0"  | 1 3/4" | A         | HM        | 1          | HM         | -           | 05       |         |
| 310      | DATA CLOSET      | 3'-0" | 7'-0"  | 1 3/4" | A         | HM        | 1          | HM         | 60 MIN      | 06       |         |
| 311      | STAIR 1          | 3'-0" | 7'-0"  | 1 3/4" | A         | HM        | 1          | HM         | 90 MIN      | 02       |         |
| 312      | STAIR 2          | 3'-0" | 7'-0"  | 1 3/4" | A         | HM        | 1          | HM         | 90 MIN      | 02       |         |
| 313      | MECHANICAL       | 3'-0" | 7'-0"  | 1 3/4" | A         | HM        | 1          | HM         | 60 MIN      | 05       |         |
| 314      | ROOF ACCESS      | 3'-0" | 7'-0"  | 1 3/4" | A         | HM        | 1          | HM         | -           | 09       |         |
| 315      | JANITOR          | 3'-0" | 7'-0"  | 1 3/4" | A         | HM        | 1          | HM         | -           | 05       |         |

DOOR TYPES

A - FLUSH  
B - HALF GLASS  
F - FULL GLASS (STOREFRONT)

MATERIALS

WD - SOLID CORE WOOD  
HM - HOLLOW METAL  
AL - ALUMINUM

HARDWARE: SEE SECTION 08 71 00

WeylandAI Sample Architects (fictional)

THE WEYLANDAI BUILDING

NEW CORPORATE HEADQUARTERS  
4400 Bluestem Parkway, Austin, TX

PROJECT NO. WAI-2026-01  
BID SET 2026-10-09

DOOR SCHEDULE

SHEET

A-601

**SECTION 08 71 00 - DOOR HARDWARE****PART 3 - EXECUTION****3.1 HARDWARE GROUPS**

A. Provide each opening with the hardware listed in its group.

**Hardware Group No. 01 MAIN ENTRY PAIR**

100A

| QTY |    | DESCRIPTION      | CATALOG NUMBER      | FINISH | MFR |
|-----|----|------------------|---------------------|--------|-----|
| 2   | EA | CONTINUOUS HINGE | SL11 HD             | 628    | SEL |
| 2   | EA | EXIT DEVICE      | 99-L-F              | 626    | VON |
| 1   | EA | RIM CYLINDER     | 20-057-ICX          | 626    | SCH |
| 2   | EA | SURFACE CLOSER   | 4040XP EDA          | 689    | LCN |
| 2   | EA | KICK PLATE       | 8400 10" X 34" B-CS | 630    | IVE |
| 1   | EA | GASKETING        | 188S-BK             | BK     | ZER |
| 2   | EA | DOOR SWEEP       | 328A                | AA     | ZER |

**Hardware Group No. 02 STAIR**

112                      113                      211                      212                      311                      312

| QTY |    | DESCRIPTION      | CATALOG NUMBER      | FINISH | MFR |
|-----|----|------------------|---------------------|--------|-----|
| 3   | EA | HINGE            | 5BB1HW 4.5 X 4.5    | 652    | IVE |
| 1   | EA | FIRE EXIT DEVICE | 99-EO-F             | 626    | VON |
| 1   | EA | SURFACE CLOSER   | 4040XP REG          | 689    | LCN |
| 1   | EA | KICK PLATE       | 8400 10" X 34" B-CS | 630    | IVE |
| 1   | EA | GASKETING        | 188S-BK             | BK     | ZER |

**Hardware Group No. 03 OFFICE**

101                      102                      103                      104                      105                      201  
 202                      203                      204                      205                      213                      301  
 302                      303                      304                      305

| QTY |    | DESCRIPTION   | CATALOG NUMBER   | FINISH | MFR |
|-----|----|---------------|------------------|--------|-----|
| 3   | EA | HINGE         | 5BB1HW 4.5 X 4.5 | 652    | IVE |
| 1   | EA | ENTRANCE LOCK | ALX53R RHO       | 626    | SCH |
| 1   | EA | WALL STOP     | WS406/407CCV     | 630    | IVE |
| 3   | EA | SILENCER      | SR64             | GRY    | IVE |

**SAMPLE PROJECT - NOT A REAL BUILDING**

The WeylandAI Building - WAI-2026-01

SECTION 08 71 00 - DOOR HARDWARE

**Hardware Group No. 04 RESTROOM**

|     |     |     |     |     |     |
|-----|-----|-----|-----|-----|-----|
| 106 | 107 | 206 | 207 | 215 | 306 |
| 307 |     |     |     |     |     |

| QTY |    | DESCRIPTION               | CATALOG NUMBER      | FINISH | MFR |
|-----|----|---------------------------|---------------------|--------|-----|
| 1   | EA | CONTINUOUS HINGE          | SL11 HD             | 628    | SEL |
| 1   | EA | PRIVACY LOCK W/ INDICATOR | ND40S RHO OS-OCC    | 626    | SCH |
| 1   | EA | SURFACE CLOSER            | 4040XP REG          | 689    | LCN |
| 1   | EA | KICK PLATE                | 8400 10" X 34" B-CS | 630    | IVE |
| 1   | EA | WALL STOP                 | WS406/407CCV        | 630    | IVE |
| 3   | EA | SILENCER                  | SR64                | GRY    | IVE |

**Hardware Group No. 05 STORAGE**

|     |     |     |     |     |     |
|-----|-----|-----|-----|-----|-----|
| 109 | 114 | 209 | 214 | 309 | 313 |
| 315 |     |     |     |     |     |

| QTY |    | DESCRIPTION    | CATALOG NUMBER   | FINISH | MFR |
|-----|----|----------------|------------------|--------|-----|
| 3   | EA | HINGE          | 5BB1HW 4.5 X 4.5 | 652    | IVE |
| 1   | EA | STOREROOM LOCK | ALX80R RHO       | 626    | SCH |
| 1   | EA | OVERHEAD STOP  | 90S              | 630    | GLY |
| 3   | EA | SILENCER       | SR64             | GRY    | IVE |

**Hardware Group No. 06 IT ROOM**

|     |     |     |
|-----|-----|-----|
| 110 | 210 | 310 |
|-----|-----|-----|

| QTY |    | DESCRIPTION     | CATALOG NUMBER   | FINISH | MFR |
|-----|----|-----------------|------------------|--------|-----|
| 3   | EA | HINGE           | 5BB1HW 4.5 X 4.5 | 652    | IVE |
| 1   | EA | STOREROOM LOCK  | ALX80R RHO       | 626    | SCH |
| 1   | EA | ELECTRIC STRIKE | 6223 FSE 24VDC   | 630    | VON |
| 1   | EA | SURFACE CLOSER  | 4040XP REG       | 689    | LCN |
| 1   | EA | CARD READER     | BY DIVISION 28   |        | B/O |
| 3   | EA | SILENCER        | SR64             | GRY    | IVE |

**Hardware Group No. 07 CORRIDOR PAIR**

|     |     |     |
|-----|-----|-----|
| 111 | 200 | 300 |
|-----|-----|-----|

| QTY |    | DESCRIPTION       | CATALOG NUMBER      | FINISH | MFR |
|-----|----|-------------------|---------------------|--------|-----|
| 2   | EA | CONTINUOUS HINGE  | SL11 HD             | 628    | SEL |
| 2   | EA | FLUSH BOLT        | FB51P               | 630    | IVE |
| 1   | EA | DUST PROOF STRIKE | DP1                 | 626    | IVE |
| 1   | EA | STOREROOM LOCK    | ALX80R RHO          | 626    | SCH |
| 2   | EA | SURFACE CLOSER    | 4040XP REG          | 689    | LCN |
| 2   | EA | KICK PLATE        | 8400 10" X 34" B-CS | 630    | IVE |
| 1   | EA | GASKETING         | 188S-BK             | BK     | ZER |

## SAMPLE PROJECT - NOT A REAL BUILDING

The WeylandAI Building - WAI-2026-01

SECTION 08 71 00 - DOOR HARDWARE

### Hardware Group No. 08 BREAK ROOM

| 108 |    | 208            | 308               |        |     |
|-----|----|----------------|-------------------|--------|-----|
| QTY |    | DESCRIPTION    | CATALOG NUMBER    | FINISH | MFR |
| 3   | EA | HINGE          | 5BB1HW 4.5 X 4.5  | 652    | IVE |
| 1   | EA | PUSH PLATE     | 8200 4" X 16"     | 630    | IVE |
| 1   | EA | PULL           | 8302 10" 4" X 16" | 630    | IVE |
| 1   | EA | SURFACE CLOSER | 4040XP REG        | 689    | LCN |
| 1   | EA | WALL STOP      | WS406/407CCV      | 630    | IVE |

### Hardware Group No. 09 ROOF ACCESS

| 314 |    |                  |                |        |     |
|-----|----|------------------|----------------|--------|-----|
| QTY |    | DESCRIPTION      | CATALOG NUMBER | FINISH | MFR |
| 1   | EA | CONTINUOUS HINGE | SL57 HD        | 628    | SEL |
| 1   | EA | EXIT DEVICE      | 99-EO          | 626    | VON |
| 1   | EA | SURFACE CLOSER   | 4040XP EDA     | 689    | LCN |
| 1   | EA | GASKETING        | 188S-BK        | BK     | ZER |
| 1   | EA | DOOR SWEEP       | 328A           | AA     | ZER |

### Hardware Group No. 10 VESTIBULE

| 100B |    |                  |                |        |     |
|------|----|------------------|----------------|--------|-----|
| QTY  |    | DESCRIPTION      | CATALOG NUMBER | FINISH | MFR |
| 1    | EA | CONTINUOUS HINGE | SL11 HD        | 628    | SEL |
| 1    | EA | EXIT DEVICE      | 99-L-F         | 626    | VON |
| 1    | EA | POWER TRANSFER   | EPT10          | 689    | VON |
| 1    | EA | SURFACE CLOSER   | 4040SE         | 689    | LCN |
| 1    | EA | PULL             | 8190HD 10" O   | 630    | IVE |

END OF SECTION 08 71 00