

HARDWARE SCHEDULE SUBMITTAL

PROJECT: R2502 Missouri Hope (first project)
DATE: 2026-10-10
PREPARED BY: Mobley Contracting

TABLE OF CONTENTS

1.	Cover Page	1
2.	Table of Contents	2
3.	Door Schedule (extracted) - 211 doors	3
4.	Source: R2502-door-schedule-pages.pdf (4 pages)	10

Door Schedule (extracted)

R2502 Missouri Hope (first project) - 211 doors read from R2502-door-schedule-pages.pdf

Machine-read from the uploaded schedule; values stay drafts until reviewed. (?) = not read with certainty, check it on the sheet. Source = page and table row on the uploaded sheet (appended at the end of this pack...

Mark	Hardware group	Size (W x H)	Thick.	Fire rating	Door type / matl / fin	Frame type / matl / fin	Notes	Source
AD101	06.02	3'-0" x 7'-0"	1 3/4"	-	WD-1 / - / -	TYP-2 / - / -	Room: MENS RESTROOM	p.1 row 0
AD102	06.02	3'-0" x 7'-0"	1 3/4"	-	WD-1 / - / -	TYP-2 / - / -	Room: WOMENS RESTROOM	p.1 row 1
PT101	09.08	8'-0" x 7'-4"	1 3/4"	-	HM-1(PR) / - / -	TYP-1 / - / -	Room: EXISTING GYMNASIUM	p.2 row 0
101A	07.03	3'-0" x 6'-8"	1 3/4"	-	WD-1 / - / -	EXIST / - / -	1; Room: DORM 101	p.3 row 0
101B	06.01	2'-0" x 6'-8"	1 3/4"	-	WD-1 / - / -	EXIST / - / -	1 & 2; Room: RESTROOM 101B	p.3 row 1
102	05.01	2'-6" x 6'-8"	1 3/4"	-	WD-1 / - / -	EXIST / - / -	1 & 2; Room: LAUNDRY ROOM...	p.3 row 2
103A	07.03	3'-0" x 6'-8"	1 3/4"	-	WD-1 / - / -	EXIST / - / -	1; Room: DORM 103	p.3 row 3
103B	06.01	2'-0" x 6'-8"	1 3/4"	-	WD-1 / - / -	EXIST / - / -	1 & 2; Room: RESTROOM 101B	p.3 row 4
104A	07.04	3'-0" x 6'-8"	1 3/4"	3/4 HR	WD-1 / - / -	TYP-2 / - / -	Room: SINGLE BEDROOM 104A	p.3 row 5
104B	06.01	3'-0" x 6'-8"	1 3/4"	-	WD-1 / - / -	TYP-2 / - / -	2; Room: PRIVATE BATH 104B	p.3 row 6
104C	06.01	3'-0" x 6'-8"	1 3/4"	-	WD-2 / - / -	TYP-2 / - / -	3; Room: SINGLE BEDROOM 1...	p.3 row 7
104D	04.02	PR 3'-4" x 6'-8"	1 3/4"	-	WD-2 (PR) / - / -	TYP-2 / - / -	3; Room: CLOSET 104	p.3 row 8
104E	04.02	3'-4" x 6'-8"	1 3/4"	-	WD-2 (PR) / - / -	TYP-2 / - / -	3; Room: CLOSET 104	p.3 row 9
105A	07.04	3'-0" x 6'-8"	1 3/4"	3/4 HR	WD-1 / - / -	EXIST / - / -	1; Room: DORM 105	p.3 row 10
105B	06.01	2'-0" x 6'-8"	1 3/4"	-	WD-1 / - / -	EXIST / - / -	1 & 2; Room: RESTROOM 105B	p.3 row 11
107A	07.04	3'-0" x 6'-8"	1 3/4"	3/4 HR	WD-1 / - / -	EXIST / - / -	1; Room: DORM 107	p.3 row 12
107B	06.01	2'-0" x 6'-8"	1 3/4"	-	WD-1 / - / -	EXIST / - / -	1 & 2; Room: RESTROOM 105B	p.3 row 13
109A	07.04	3'-0" x 6'-8"	1 3/4"	3/4 HR	WD-1 / - / -	EXIST / - / -	1; Room: DORM 109	p.3 row 14
109B	06.01	2'-0" x 6'-8"	1 3/4"	-	WD-1 / - / -	EXIST / - / -	1 & 2; Room: RESTROOM 109B	p.3 row 15
110	09.05	3'-0" x 6'-8"	1 3/4"	3/4 HR	WD-1 / - / -	EXIST / - / -	1; Room: STORAGE 110	p.3 row 16
111A	07.04	3'-0" x 6'-8"	1 3/4"	3/4 HR	WD-1 / - / -	EXIST / - / -	1; Room: DORM 111	p.3 row 17
111B	06.01	2'-0" x 6'-8"	1 3/4"	-	WD-1 / - / -	EXIST / - / -	1 & 2; Room: RESTROOM 109B	p.3 row 18
112A	01.02	6'-0" x 7'-0"	1 3/4"	-	AL-1 (PR) / - / -	GLZ-A / - / -	4; Room: VESTIBULE 112	p.3 row 19
112B	04.01	6'-0" x 7'-0"	1 3/4"	-	AL-1 (PR) / - / -	GLZ-B / - / -	Room: VESTIBULE 112	p.3 row 20
113	08.02	3'-0" x 6'-8"	1 3/4"	-	WD-1 / - / -	EXIST / - / -	1; Room: KITCHENETE 113	p.3 row 21
114	09.02	3'-0" x 6'-8"	1 3/4"	-	WD-1 / - / -	EXIST / - / -	1; Room: STORAGE 114	p.3 row 22
115	06.02	3'-0" x 6'-8"	1 3/4"	-	WD-1 / - / -	EXIST / - / -	1 & 2; Room: UNISEX RESTRO...	p.3 row 23
116	09.01	3'-0" x 6'-8"	1 3/4"	-	WD-1 / - / -	EXIST / - / -	1 & 2; Room: JANITOR CLOSE...	p.3 row 24
117	07.01	3'-0" x 6'-8"	1 3/4"	-	WD-1 / - / -	TYP-2 / - / -	Room: OFFICE 117	p.3 row 25
118	07.01	3'-0" x 6'-8"	1 3/4"	-	WD-1 / - / -	TYP-2 / - / -	Room: OFFICE 118	p.3 row 26
119	08.01	3'-0" x 6'-8"	1 3/4"	-	WD-1 / - / -	TYP-2 / - / -	Room: CONFERENCE ROOM ...	p.3 row 27
120A	07.01	3'-0" x 6'-8"	1 3/4"	-	WD-1 / - / -	TYP-2 / - / -	Room: OFFICE 120	p.3 row 28
120B	06.01	3'-0" x 6'-8"	1 3/4"	-	WD-1 / - / -	TYP-2 / - / -	2; Room: RESTROOM 120B	p.3 row 29
121	08.01	3'-0" x 6'-8"	1 3/4"	-	WD-1 / - / -	TYP-2 / - / -	Room: CONFERENCE ROOM ...	p.3 row 30
122A	07.01	3'-0" x 6'-8"	1 3/4"	-	WD-1 / - / -	TYP-2 / - / -	Room: OFFICE 122	p.3 row 31

Door Schedule (extracted) (continued)

R2502 Missouri Hope (first project) - 211 doors read from R2502-door-schedule-pages.pdf

Machine-read from the uploaded schedule; values stay drafts until reviewed. (?) = not read with certainty, check it on the sheet. Source = page and table row on the uploaded sheet (appended at the end of this pack...

Mark	Hardware group	Size (W x H)	Thick.	Fire rating	Door type / matl / fin	Frame type / matl / fin	Notes	Source
122B	06.01	3'-0" x 6'-8"	1 3/4"	-	WD-1 / - / -	TYP-2 / - / -	2; Room: RESTROOM 120B	p.3 row 32
123A	07.01	3'-0" x 6'-8"	1 3/4"	-	WD-1 / - / -	TYP-2 / - / -	Room: OFFICE 123	p.3 row 33
123B	06.01	3'-0" x 6'-8"	1 3/4"	-	WD-1 / - / -	TYP-2 / - / -	2; Room: RESTROOM 123B	p.3 row 34
124	09.06	3'-0" x 6'-8"	1 3/4"	3/4 HR	WD-1 / - / -	EXIST / - / -	1; Room: STORAGE 124	p.3 row 35
125A	07.04	3'-0" x 6'-8"	1 3/4"	3/4 HR	WD-1 / - / -	TYP-2 / - / -	Room: OFFICE 125	p.3 row 36
125B	06.01	3'-0" x 6'-8"	1 3/4"	-	WD-1 / - / -	TYP-2 / - / -	2; Room: RESTROOM 125B	p.3 row 37
126A	07.04	3'-0" x 6'-8"	1 3/4"	3/4 HR	WD-1 / - / -	TYP-2 / - / -	Room: OFFICE 126	p.3 row 38
126B	06.01	3'-0" x 6'-8"	1 3/4"	-	WD-1 / - / -	TYP-2 / - / -	2; Room: RESTROOM 126B	p.3 row 39
127	08.03	3'-0" x 6'-8"	1 3/4"	3/4 HR	WD-1 / - / -	TYP-2 / - / -	Room: CLASSROOM 127	p.3 row 40
128A	07.04	3'-0" x 6'-8"	1 3/4"	3/4 HR	WD-1 / - / -	TYP-2 / - / -	Room: OFFICE 128	p.3 row 41
128B	06.01	3'-0" x 6'-8"	1 3/4"	-	WD-1 / - / -	TYP-2 / - / -	2; Room: RESTROOM 126B	p.3 row 42
129A	05.04	8'-0" x 7'-0"	1 3/4"	-	HM-1 (PR) / - / -	TYP-1 / - / -	Room: MECHANICAL ROOM 129	p.3 row 43
129B	00.01	3'-0" x 6'-8"	1 3/4"	-	EXIST / - / -	EXIST / - / -	1; Room: MECHANICAL ROOM...	p.3 row 44
129C	00.01	5'-0" x 7'-0"	1 3/4"	-	EXIST / - / -	EXIST / - / -	1; Room: MECHANICAL ROOM...	p.3 row 45
129D	00.01	3'-0" x 6'-8"	1 3/4"	3/4 HR	EXIST / - / -	EXIST / - / -	1; Room: STAIR	p.3 row 46
129F	00.01	3'-0" x 6'-8"	1 3/4"	-	EXIST / - / -	EXIST / - / -	1; Room: MECHANICAL ROOM...	p.3 row 47
130A	01.01	3'-0" x 7'-0"	1 3/4"	3/4 HR	HM-2 / - / -	TYP-1 / - / -	4; Room: CORRIDOR 130	p.3 row 48
130B	00.01	3'-0" x 6'-8"	1 3/4"	3/4 HR	EXIST / - / -	EXIST / - / -	1; Room: STAIR	p.3 row 49
130C	05.02A	3'-0" x 6'-8"	1 3/4"	3/4 HR	HM-2 / - / -	TYP-2 / - / -	Room: CORRIDOR 130	p.3 row 50
133A	00.02	3'-0" x 7'-0"	1 3/4"	3/4 HR	EXIST / - / -	EXIST / - / -	1 & 4; Room: CORRIDOR 133	p.3 row 51
133B	00.01	3'-0" x 6'-8"	1 3/4"	3/4 HR	EXIST / - / -	EXIST / - / -	1; Room: STAIR	p.3 row 52
133C	05.02A	3'-0" x 6'-8"	1 3/4"	3/4 HR	HM-2 / - / -	TYP-2 / - / -	Room: CORRIDOR 133	p.3 row 53
201A	07.03	3'-0" x 6'-8"	1 3/4"	-	WD-1 / - / -	EXIST / - / -	1; Room: DORM 201	p.3 row 0
201B	06.01	2'-0" x 6'-8"	1 3/4"	-	WD-1 / - / -	EXIST / - / -	1 & 2; Room: RESTROOM 201B	p.3 row 1
202A	07.03	3'-0" x 6'-8"	1 3/4"	-	WD-1 / - / -	EXIST / - / -	1; Room: DORM 202	p.3 row 2
202B	06.01	2'-0" x 6'-8"	1 3/4"	-	WD-1 / - / -	EXIST / - / -	1 & 2; Room: RESTROOM 202B	p.3 row 3
203A	07.03	3'-0" x 6'-8"	1 3/4"	-	WD-1 / - / -	EXIST / - / -	1; Room: DORM 203	p.3 row 4
203B	06.01	2'-0" x 6'-8"	1 3/4"	-	WD-1 / - / -	EXIST / - / -	1 & 2; Room: RESTROOM 203B	p.3 row 5
204A	07.03	3'-0" x 6'-8"	1 3/4"	-	WD-1 / - / -	EXIST / - / -	1; Room: DORM 204	p.3 row 6
204B	06.01	2'-0" x 6'-8"	1 3/4"	-	WD-1 / - / -	EXIST / - / -	1 & 2; Room: RESTROOM 202B	p.3 row 7
205A	07.03	3'-0" x 6'-8"	1 3/4"	3/4 HR	WD-1 / - / -	EXIST / - / -	1; Room: DORM 205	p.3 row 8
205B	06.01	2'-0" x 6'-8"	1 3/4"	-	WD-1 / - / -	EXIST / - / -	1 & 2; Room: RESTROOM 203B	p.3 row 9
206A	07.03	3'-0" x 6'-8"	1 3/4"	3/4 HR	WD-1 / - / -	EXIST / - / -	1; Room: DORM 206	p.3 row 10
206B	06.01	2'-0" x 6'-8"	1 3/4"	-	WD-1 / - / -	EXIST / - / -	1 & 2; Room: RESTROOM 206B	p.3 row 11
207A	07.03	3'-0" x 6'-8"	1 3/4"	3/4 HR	WD-1 / - / -	EXIST / - / -	1; Room: DORM 207	p.3 row 12

Door Schedule (extracted) (continued)

R2502 Missouri Hope (first project) - 211 doors read from R2502-door-schedule-pages.pdf

Machine-read from the uploaded schedule; values stay drafts until reviewed. (?) = not read with certainty, check it on the sheet. Source = page and table row on the uploaded sheet (appended at the end of this pack...

Mark	Hardware group	Size (W x H)	Thick.	Fire rating	Door type / matl / fin	Frame type / matl / fin	Notes	Source
207B	06.01	2'-0" x 6'-8"	1 3/4"	-	WD-1 / - / -	EXIST / - / -	1 & 2; Room: RESTROOM 207B	p.3 row 13
208A	07.03	3'-0" x 6'-8"	1 3/4"	3/4 HR	WD-1 / - / -	EXIST / - / -	1; Room: DORM 208	p.3 row 14
208B	06.01	2'-0" x 6'-8"	1 3/4"	-	WD-1 / - / -	EXIST / - / -	1 & 2; Room: RESTROOM 206B	p.3 row 15
209A	07.03	3'-0" x 6'-8"	1 3/4"	3/4 HR	WD-1 / - / -	EXIST / - / -	1; Room: DORM 209	p.3 row 16
209B	06.01	2'-0" x 6'-8"	1 3/4"	-	WD-1 / - / -	EXIST / - / -	1 & 2; Room: RESTROOM 207B	p.3 row 17
210A	07.03	3'-0" x 6'-8"	1 3/4"	-	WD-1 / - / -	EXIST / - / -	1; Room: DORM 210	p.3 row 18
210B	06.01	2'-0" x 6'-8"	1 3/4"	-	WD-1 / - / -	EXIST / - / -	1 & 2; Room: RESTROOM 210B	p.3 row 19
211A	07.03	3'-0" x 6'-8"	1 3/4"	-	WD-1 / - / -	EXIST / - / -	1; Room: DORM 211	p.3 row 20
211B	06.01	2'-0" x 6'-8"	1 3/4"	-	WD-1 / - / -	EXIST / - / -	1 & 2; Room: RESTROOM 211B	p.3 row 21
212A	07.03	3'-0" x 6'-8"	1 3/4"	-	WD-1 / - / -	EXIST / - / -	1; Room: DORM 212	p.3 row 22
212B	06.01	2'-0" x 6'-8"	1 3/4"	-	WD-1 / - / -	EXIST / - / -	1 & 2; Room: RESTROOM 210B	p.3 row 23
213A	07.03	3'-0" x 6'-8"	1 3/4"	-	WD-1 / - / -	EXIST / - / -	1; Room: DORM 213	p.3 row 24
213B	06.01	2'-0" x 6'-8"	1 3/4"	-	WD-1 / - / -	EXIST / - / -	1 & 2; Room: RESTROOM 211B	p.3 row 25
214A	07.03	3'-0" x 6'-8"	1 3/4"	-	WD-1 / - / -	EXIST / - / -	1; Room: DORM 214	p.3 row 26
214B	06.01	2'-0" x 6'-8"	1 3/4"	-	WD-1 / - / -	EXIST / - / -	1 & 2; Room: RESTROOM 214B	p.3 row 27
215A	07.02	3'-0" x 6'-8"	1 3/4"	-	WD-1 / - / -	TYP-2 / - / -	Room: PRIVATE DORM 215	p.3 row 28
215B	06.01	3'-0" x 6'-8"	1 3/4"	-	WD-1 / - / -	TYP-2 / - / -	2; Room: PRIVATE RESTROO...	p.3 row 29
216A	07.03	3'-0" x 6'-8"	1 3/4"	-	WD-1 / - / -	EXIST / - / -	1; Room: DORM 216	p.3 row 30
216B	06.01	2'-0" x 6'-8"	1 3/4"	-	WD-1 / - / -	EXIST / - / -	1 & 2; Room: RESTROOM 214B	p.3 row 31
217A	07.03	3'-0" x 6'-8"	1 3/4"	-	WD-1 / - / -	EXIST / - / -	1; Room: DORM 217	p.3 row 32
217B	06.01	2'-0" x 6'-8"	1 3/4"	-	WD-1 / - / -	EXIST / - / -	1 & 2; Room: RESTROOM 217B	p.3 row 33
218A	07.03	3'-0" x 6'-8"	1 3/4"	-	WD-1 / - / -	EXIST / - / -	1; Room: DORM 218	p.3 row 34
218B	06.01	2'-0" x 6'-8"	1 3/4"	-	WD-1 / - / -	EXIST / - / -	1 & 2; Room: RESTROOM 218B	p.3 row 35
219A	07.03	3'-0" x 6'-8"	1 3/4"	-	WD-1 / - / -	EXIST / - / -	1; Room: DORM 219	p.3 row 36
219B	06.01	2'-0" x 6'-8"	1 3/4"	-	WD-1 / - / -	EXIST / - / -	1 & 2; Room: RESTROOM 217B	p.3 row 37
220A	07.03	3'-0" x 6'-8"	1 3/4"	-	WD-1 / - / -	EXIST / - / -	1; Room: DORM 220	p.3 row 38
220B	06.01	2'-0" x 6'-8"	1 3/4"	-	WD-1 / - / -	EXIST / - / -	1 & 2; Room: RESTROOM 218B	p.3 row 39
221A	07.03	3'-0" x 6'-8"	1 3/4"	-	WD-1 / - / -	EXIST / - / -	1; Room: DORM 221	p.3 row 40
221B	06.01	2'-0" x 6'-8"	1 3/4"	-	WD-1 / - / -	EXIST / - / -	1 & 2; Room: RESTROOM 221`B	p.3 row 41
222A	07.03	3'-0" x 6'-8"	1 3/4"	-	WD-1 / - / -	EXIST / - / -	1; Room: DORM 222	p.3 row 42
222B	06.01	2'-0" x 6'-8"	1 3/4"	-	WD-1 / - / -	EXIST / - / -	1 & 2; Room: RESTROOM 222B	p.3 row 43
223A	07.03	3'-0" x 6'-8"	1 3/4"	-	WD-1 / - / -	EXIST / - / -	1; Room: DORM 223	p.3 row 44
223B	06.01	2'-0" x 6'-8"	1 3/4"	-	WD-1 / - / -	EXIST / - / -	1 & 2; Room: RESTROOM 221B	p.3 row 45
224A	07.03	3'-0" x 6'-8"	1 3/4"	-	WD-1 / - / -	EXIST / - / -	1; Room: DORM 224	p.3 row 46
224B	06.01	2'-0" x 6'-8"	1 3/4"	-	WD-1 / - / -	EXIST / - / -	1 & 2; Room: RESTROOM 222B	p.3 row 47

Door Schedule (extracted) (continued)

R2502 Missouri Hope (first project) - 211 doors read from R2502-door-schedule-pages.pdf

Machine-read from the uploaded schedule; values stay drafts until reviewed. (?) = not read with certainty, check it on the sheet. Source = page and table row on the uploaded sheet (appended at the end of this pack...

Mark	Hardware group	Size (W x H)	Thick.	Fire rating	Door type / matl / fin	Frame type / matl / fin	Notes	Source
225A	07.03	3'-0" x 6'-8"	1 3/4"	-	WD-1 / - / -	EXIST / - / -	1; Room: DORM 225	p.3 row 48
225B	06.01	2'-0" x 6'-8"	1 3/4"	-	WD-1 / - / -	EXIST / - / -	1 & 2; Room: RESTROOM 225B	p.3 row 49
226A	07.02	3'-0" x 6'-8"	1 3/4"	-	WD-1 / - / -	EXIST / - / -	1; Room: ACCESSIBLE DORM ...	p.3 row 50
226B	06.01	3'-0" x 6'-8"	1 3/4"	-	WD-1 / - / -	EXIST / - / -	1 & 2; Room: ACCESSIBLE RE...	p.3 row 51
227A	07.03	3'-0" x 6'-8"	1 3/4"	-	WD-1 / - / -	EXIST / - / -	1; Room: DORM 227	p.3 row 52
227B	06.01	2'-0" x 6'-8"	1 3/4"	-	WD-1 / - / -	EXIST / - / -	1 & 2; Room: RESTROOM 225B	p.3 row 53
228A	07.03	3'-0" x 6'-8"	1 3/4"	-	WD-1 / - / -	EXIST / - / -	1; Room: DORM 228	p.3 row 54
228B	06.01	2'-0" x 6'-8"	1 3/4"	-	WD-1 / - / -	EXIST / - / -	1 & 2; Room: RESTROOM 228B	p.3 row 55
229A	07.03	3'-0" x 6'-8"	1 3/4"	-	WD-1 / - / -	EXIST / - / -	1; Room: DORM 229	p.3 row 56
229B	06.01	2'-0" x 6'-8"	1 3/4"	-	WD-1 / - / -	EXIST / - / -	1 & 2; Room: RESTROOM 229B	p.3 row 57
230A	07.03	3'-0" x 6'-8"	1 3/4"	-	WD-1 / - / -	EXIST / - / -	1; Room: DORM 230	p.3 row 58
230B	06.01	2'-0" x 6'-8"	1 3/4"	-	WD-1 / - / -	EXIST / - / -	1 & 2; Room: RESTROOM 228B	p.3 row 59
231A	07.03	3'-0" x 6'-8"	1 3/4"	-	WD-1 / - / -	EXIST / - / -	1; Room: DORM 231	p.3 row 60
231B	06.01	2'-0" x 6'-8"	1 3/4"	-	WD-1 / - / -	EXIST / - / -	1 & 2; Room: RESTROOM 229B	p.3 row 61
232A	07.03	3'-0" x 6'-8"	1 3/4"	-	WD-1 / - / -	TYP-2 / - / -	Room: LIVING ROOM 232	p.3 row 62
232B	06.01	3'-0" x 6'-8"	1 3/4"	-	WD-1 / - / -	TYP-2 / - / -	2; Room: RESTROOM 232B	p.3 row 63
232C	06.01	3'-0" x 6'-8"	1 3/4"	-	WD-1 / - / -	TYP-2 / - / -	Room: BEDROOM 232	p.3 row 64
233A	00.01	3'-0" x 6'-8"	1 3/4"	3/4 HR	EXIST / - / -	EXIST / - / -	1; Room: STAIR	p.3 row 65
233B	05.02	3'-0" x 6'-8"	1 3/4"	3/4 HR	HM-2 / - / -	TYP-2 / - / -	Room: CORRIDOR 240	p.3 row 66
234	-	3'-0" x 6'-8"	1 3/4"	-	WD-2 / - / -	TYP-2 / - / -	3; Room: UNISEX RESTROOM...	p.3 row 67
235A	00.01	3'-0" x 6'-8"	1 3/4"	3/4 HR	EXIST / - / -	EXIST / - / -	1; Room: STAIR	p.3 row 68
235B	05.02	3'-0" x 6'-8"	1 3/4"	3/4 HR	HM-2 / - / -	TYP-2 / - / -	Room: CORRIDOR 240	p.3 row 69
236	09.03	3'-0" x 6'-8"	1 3/4"	-	WD-1 / - / -	EXIST / - / -	1 & 2; Room: JANITOR CLOSE...	p.3 row 70
237	09.04	3'-0" x 6'-8"	1 3/4"	-	WD-1 / - / -	EXIST / - / -	1 & 2; Room: CLEAN LINEN 237	p.3 row 71
238	09.02	3'-0" x 6'-8"	1 3/4"	3/4 HR	WD-1 / - / -	EXIST / - / -	1; Room: STORAGE 238	p.3 row 72
239A	01.01	3'-0" x 7'-0"	1 3/4"	3/4 HR	AL-1 / - / -	GLZ-C / - / -	4; Room: CORRIDOR 239	p.3 row 73
239B	01.01	3'-0" x 7'-0"	1 3/4"	3/4 HR	AL-1 / - / -	GLZ-D / - / -	4; Room: CORRIDOR 239	p.3 row 74
239C	00.01	3'-0" x 6'-8"	1 3/4"	3/4 HR	EXIST / - / -	EXIST / - / -	Room: STAIR	p.3 row 75
239D	05.02A	3'-0" x 6'-8"	1 3/4"	3/4 HR	HM-2 / - / -	TYP-2 / - / -	Room: CORRIDOR 239	p.3 row 76
301A	07.03	3'-0" x 6'-8"	1 3/4"	-	WD-1 / - / -	EXIST / - / -	1; Room: DORM 301	p.4 row 0
301B	06.01	2'-0" x 6'-8"	1 3/4"	-	WD-1 / - / -	EXIST / - / -	1 & 2; Room: RESTROOM 301B	p.4 row 1
302A	07.03	3'-0" x 6'-8"	1 3/4"	-	WD-1 / - / -	EXIST / - / -	1; Room: DORM 302	p.4 row 2
302B	06.01	2'-0" x 6'-8"	1 3/4"	-	WD-1 / - / -	EXIST / - / -	1 & 2; Room: RESTROOM 302B	p.4 row 3
303A	07.03	3'-0" x 6'-8"	1 3/4"	-	WD-1 / - / -	EXIST / - / -	1; Room: DORM 303	p.4 row 4
303B	06.01	2'-0" x 6'-8"	1 3/4"	-	WD-1 / - / -	EXIST / - / -	1 & 2; Room: RESTROOM 303B	p.4 row 5

Door Schedule (extracted) (continued)

R2502 Missouri Hope (first project) - 211 doors read from R2502-door-schedule-pages.pdf

Machine-read from the uploaded schedule; values stay drafts until reviewed. (?) = not read with certainty, check it on the sheet. Source = page and table row on the uploaded sheet (appended at the end of this pack...

Mark	Hardware group	Size (W x H)	Thick.	Fire rating	Door type / matl / fin	Frame type / matl / fin	Notes	Source
304A	07.03	3'-0" x 6'-8"	1 3/4"	-	WD-1 / - / -	EXIST / - / -	1; Room: DORM 304	p.4 row 6
304B	06.01	2'-0" x 6'-8"	1 3/4"	-	WD-1 / - / -	EXIST / - / -	1 & 2; Room: RESTROOM 302B	p.4 row 7
305A	07.03	3'-0" x 6'-8"	1 3/4"	-	WD-1 / - / -	EXIST / - / -	1; Room: DORM 305	p.4 row 8
305B	06.01	2'-0" x 6'-8"	1 3/4"	-	WD-1 / - / -	EXIST / - / -	1 & 2; Room: RESTROOM 303B	p.4 row 9
306A	07.03	3'-0" x 6'-8"	1 3/4"	-	WD-1 / - / -	EXIST / - / -	1; Room: DORM 306	p.4 row 10
306B	06.01	2'-0" x 6'-8"	1 3/4"	-	WD-1 / - / -	EXIST / - / -	1 & 2; Room: RESTROOM 306B	p.4 row 11
307A	07.03	3'-0" x 6'-8"	1 3/4"	-	WD-1 / - / -	EXIST / - / -	1; Room: DORM 307	p.4 row 12
307B	06.01	2'-0" x 6'-8"	1 3/4"	-	WD-1 / - / -	EXIST / - / -	1 & 2; Room: RESTROOM 307B	p.4 row 13
308A	07.03	3'-0" x 6'-8"	1 3/4"	-	WD-1 / - / -	EXIST / - / -	1; Room: DORM 308	p.4 row 14
308B	06.01	2'-0" x 6'-8"	1 3/4"	-	WD-1 / - / -	EXIST / - / -	1 & 2; Room: RESTROOM 306B	p.4 row 15
309A	07.03	3'-0" x 6'-8"	1 3/4"	-	WD-1 / - / -	EXIST / - / -	1; Room: DORM 309	p.4 row 16
309B	06.01	2'-0" x 6'-8"	1 3/4"	-	WD-1 / - / -	EXIST / - / -	1 & 2; Room: RESTROOM 307B	p.4 row 17
310A	07.03	3'-0" x 6'-8"	1 3/4"	-	WD-1 / - / -	EXIST / - / -	1; Room: DORM 310	p.4 row 18
310B	06.01	2'-0" x 6'-8"	1 3/4"	-	WD-1 / - / -	EXIST / - / -	1 & 2; Room: RESTROOM 310B	p.4 row 19
311A	07.03	3'-0" x 6'-8"	1 3/4"	-	WD-1 / - / -	EXIST / - / -	1; Room: DORM 311	p.4 row 20
311B	06.01	2'-0" x 6'-8"	1 3/4"	-	WD-1 / - / -	EXIST / - / -	1 & 2; Room: RESTROOM 311B	p.4 row 21
312A	07.03	3'-0" x 6'-8"	1 3/4"	-	WD-1 / - / -	EXIST / - / -	1; Room: DORM 312	p.4 row 22
312B	06.01	2'-0" x 6'-8"	1 3/4"	-	WD-1 / - / -	EXIST / - / -	1 & 2; Room: RESTROOM 310B	p.4 row 23
313A	07.03	3'-0" x 6'-8"	1 3/4"	-	WD-1 / - / -	EXIST / - / -	1; Room: DORM 313	p.4 row 24
313B	06.01	2'-0" x 6'-8"	1 3/4"	-	WD-1 / - / -	EXIST / - / -	1 & 2; Room: RESTROOM 311B	p.4 row 25
314A	07.03	3'-0" x 6'-8"	1 3/4"	-	WD-1 / - / -	EXIST / - / -	1; Room: DORM 314	p.4 row 26
314B	06.01	2'-0" x 6'-8"	1 3/4"	-	WD-1 / - / -	EXIST / - / -	1 & 2; Room: RESTROOM 314B	p.4 row 27
315A	07.02	3'-0" x 6'-8"	1 3/4"	-	WD-1 / - / -	TYP-2 / - / -	Room: ACCESSIBLE DORM 315	p.4 row 28
315B	06.01	3'-0" x 6'-8"	1 3/4"	-	WD-1 / - / -	TYP-2 / - / -	2; Room: ACCESSIBLE RESTR...	p.4 row 29
316A	07.03	3'-0" x 6'-8"	1 3/4"	-	WD-1 / - / -	EXIST / - / -	1; Room: DORM 316	p.4 row 30
316B	06.01	2'-0" x 6'-8"	1 3/4"	-	WD-1 / - / -	EXIST / - / -	1 & 2; Room: RESTROOM 314B	p.4 row 31
317A	07.03	3'-0" x 6'-8"	1 3/4"	-	WD-1 / - / -	EXIST / - / -	1; Room: DORM 317	p.4 row 32
317B	06.01	2'-0" x 6'-8"	1 3/4"	-	WD-1 / - / -	EXIST / - / -	1 & 2; Room: RESTROOM 317B	p.4 row 33
318A	07.03	3'-0" x 6'-8"	1 3/4"	-	WD-1 / - / -	EXIST / - / -	1; Room: DORM 318	p.4 row 34
318B	06.01	2'-0" x 6'-8"	1 3/4"	-	WD-1 / - / -	EXIST / - / -	1 & 2; Room: RESTROOM 318B	p.4 row 35
319A	07.03	3'-0" x 6'-8"	1 3/4"	-	WD-1 / - / -	EXIST / - / -	1; Room: DORM 319	p.4 row 36
319B	06.01	2'-0" x 6'-8"	1 3/4"	-	WD-1 / - / -	EXIST / - / -	1 & 2; Room: RESTROOM 317B	p.4 row 37
320A	07.03	3'-0" x 6'-8"	1 3/4"	-	WD-1 / - / -	EXIST / - / -	1; Room: DORM 320	p.4 row 38
320B	06.01	2'-0" x 6'-8"	1 3/4"	-	WD-1 / - / -	EXIST / - / -	1 & 2; Room: RESTROOM 318B	p.4 row 39
321A	07.03	3'-0" x 6'-8"	1 3/4"	-	WD-1 / - / -	EXIST / - / -	1; Room: DORM 321	p.4 row 40

Door Schedule (extracted) (continued)

R2502 Missouri Hope (first project) - 211 doors read from R2502-door-schedule-pages.pdf

Machine-read from the uploaded schedule; values stay drafts until reviewed. (?) = not read with certainty, check it on the sheet. Source = page and table row on the uploaded sheet (appended at the end of this pack...


Mark	Hardware group	Size (W x H)	Thick.	Fire rating	Door type / matl / fin	Frame type / matl / fin	Notes	Source
321B	06.01	2'-0" x 6'-8"	1 3/4"	-	WD-1 / - / -	EXIST / - / -	1 & 2; Room: RESTROOM 321B	p.4 row 41
322A	07.03	3'-0" x 6'-8"	1 3/4"	-	WD-1 / - / -	EXIST / - / -	1; Room: DORM 322	p.4 row 42
322B	06.01	2'-0" x 6'-8"	1 3/4"	-	WD-1 / - / -	EXIST / - / -	1 & 2; Room: RESTROOM 322B	p.4 row 43
323A	07.03	3'-0" x 6'-8"	1 3/4"	-	WD-1 / - / -	EXIST / - / -	1; Room: DORM 323	p.4 row 44
323B	06.01	2'-0" x 6'-8"	1 3/4"	-	WD-1 / - / -	EXIST / - / -	1 & 2; Room: RESTROOM 321B	p.4 row 45
324A	07.03	3'-0" x 6'-8"	1 3/4"	-	WD-1 / - / -	EXIST / - / -	1; Room: DORM 324	p.4 row 46
324B	06.01	2'-0" x 6'-8"	1 3/4"	-	WD-1 / - / -	EXIST / - / -	1 & 2; Room: RESTROOM 322B	p.4 row 47
325A	07.03	3'-0" x 6'-8"	1 3/4"	-	WD-1 / - / -	EXIST / - / -	1; Room: DORM 325	p.4 row 48
325B	06.01	2'-0" x 6'-8"	1 3/4"	-	WD-1 / - / -	EXIST / - / -	1 & 2; Room: RESTROOM 325B	p.4 row 49
326A	07.02	3'-0" x 6'-8"	1 3/4"	-	WD-1 / - / -	EXIST / - / -	1; Room: ACCESSIBLE DORM ...	p.4 row 50
326B	06.01	3'-0" x 6'-8"	1 3/4"	-	WD-1 / - / -	TYP-2 / - / -	2; Room: ACCESSIBLE RESTR...	p.4 row 51
327A	07.03	3'-0" x 6'-8"	1 3/4"	-	WD-1 / - / -	EXIST / - / -	1; Room: DORM 327	p.4 row 52
327B	06.01	2'-0" x 6'-8"	1 3/4"	-	WD-1 / - / -	EXIST / - / -	1 & 2; Room: RESTROOM 325B	p.4 row 53
328A	07.03	3'-0" x 6'-8"	1 3/4"	-	WD-1 / - / -	EXIST / - / -	1; Room: DORM 328	p.4 row 54
328B	06.01	2'-0" x 6'-8"	1 3/4"	-	WD-1 / - / -	EXIST / - / -	1 & 2; Room: RESTROOM 328B	p.4 row 55
329A	07.03	3'-0" x 6'-8"	1 3/4"	-	WD-1 / - / -	EXIST / - / -	1; Room: DORM 329	p.4 row 56
329B	06.01	2'-0" x 6'-8"	1 3/4"	-	WD-1 / - / -	EXIST / - / -	1 & 2; Room: RESTROOM 329B	p.4 row 57
330A	07.03	3'-0" x 6'-8"	1 3/4"	-	WD-1 / - / -	EXIST / - / -	1; Room: DORM 330	p.4 row 58
330B	06.01	2'-0" x 6'-8"	1 3/4"	-	WD-1 / - / -	EXIST / - / -	1 & 2; Room: RESTROOM 328B	p.4 row 59
331A	07.03	3'-0" x 6'-8"	1 3/4"	-	WD-1 / - / -	EXIST / - / -	1; Room: DORM 331	p.4 row 60
331B	06.01	2'-0" x 6'-8"	1 3/4"	-	WD-1 / - / -	EXIST / - / -	1 & 2; Room: RESTROOM 329B	p.4 row 61
332A	07.03	3'-0" x 6'-8"	1 3/4"	-	WD-1 / - / -	TYP-2 / - / -	Room: LIVING ROOM 332	p.4 row 62
332B	06.01	3'-0" x 6'-8"	1 3/4"	-	WD-1 / - / -	TYP-2 / - / -	2; Room: RESTROOM 332B	p.4 row 63
332C	06.01	3'-0" x 6'-8"	1 3/4"	-	WD-2 / - / -	TYP-2 / - / -	3; Room: BEDROOM 332C	p.4 row 64
332D	06.01	3'-0" x 6'-8"	1 3/4"	-	WD-2 / - / -	TYP-2 / - / -	3; Room: BEDROOM 332D	p.4 row 65
333A	00.01	3'-0" x 6'-8"	1 3/4"	3/4 HR	EXIST / - / -	EXIST / - / -	1; Room: STAIR	p.4 row 66
333B	05.02	3'-0" x 6'-8"	1 3/4"	3/4 HR	HM-2 / - / -	TYP-2 / - / -	Room: CORRIDOR 341	p.4 row 67
334	06.02	3'-0" x 6'-8"	1 3/4"	-	WD-2 / - / -	TYP-2 / - / -	3; Room: UNISEX RESTROOM...	p.4 row 68
335A	00.01	3'-0" x 6'-8"	1 3/4"	3/4 HR	EXIST / - / -	EXIST / - / -	1; Room: STAIR	p.4 row 69
335B	05.02	3'-0" x 6'-8"	1 3/4"	3/4 HR	HM-2 / - / -	TYP-2 / - / -	Room: CORRIDOR 341	p.4 row 70
336A	09.03	3'-0" x 6'-8"	1 3/4"	-	WD-1 / - / -	EXIST / - / -	1 & 2; Room: JANITOR CLOSE...	p.4 row 71
336B	09.02	3'-0" x 6'-8"	1 3/4"	-	WD-1 / - / -	TYP-2 / - / -	Room: STORAGE 336B	p.4 row 72
337	09.04	3'-0" x 6'-8"	1 3/4"	-	WD-1 / - / -	EXIST / - / -	1 & 2; Room: CLEAN LINEN 337	p.4 row 73
338A	-	3'-0" x 6'-8"	1 3/4"	3/4 HR	EXIST / - / -	EXIST / - / -	1; Room: STAIR	p.4 row 74
338B	05.02	3'-0" x 6'-8"	1 3/4"	3/4 HR	HM-2 / - / -	TYP-2 / - / -	Room: CORRIDOR 340	p.4 row 75

Door Schedule (extracted) (continued)


R2502 Missouri Hope (first project) - 211 doors read from R2502-door-schedule-pages.pdf

Machine-read from the uploaded schedule; values stay drafts until reviewed. (?) = not read with certainty, check it on the sheet. Source = page and table row on the uploaded sheet (appended at the end of this pack...


Mark	Hardware group	Size (W x H)	Thick.	Fire rating	Door type / matl / fin	Frame type / matl / fin	Notes	Source
339	09.02	3'-0" x 6'-8"	1 3/4"	3/4 HR	WD-1 / - / -	EXIST / - / -	1; Room: STORAGE 339	p.4 row 76

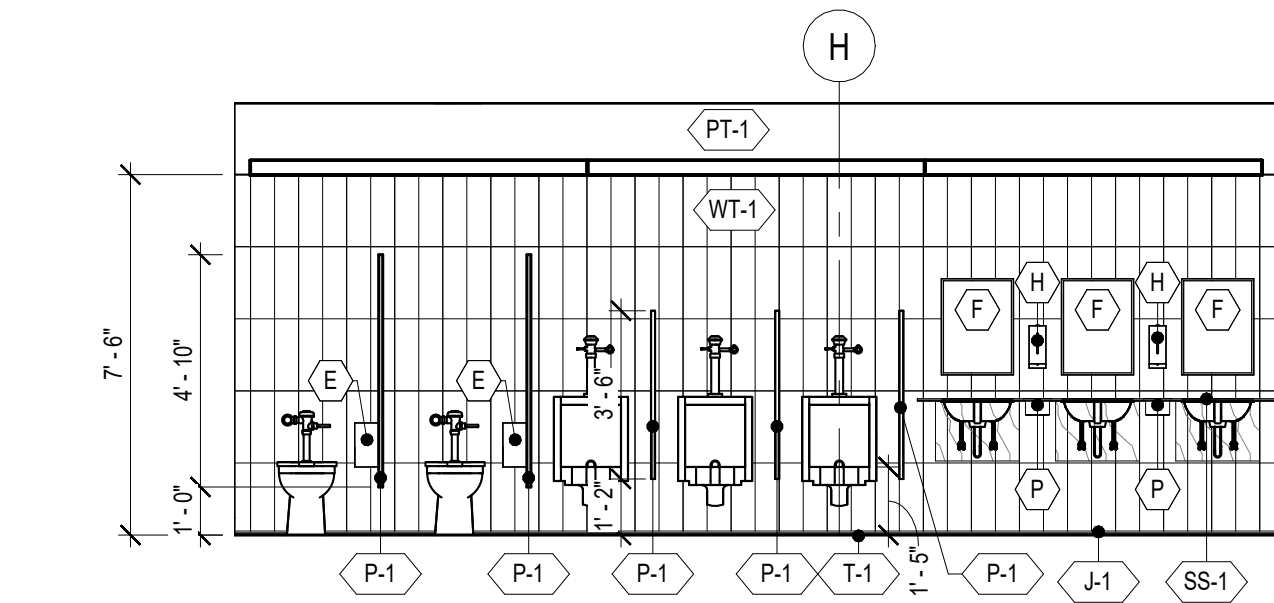


1
A-112
MENS RESTROOM
SCALE: 1/4" = 1'-0"

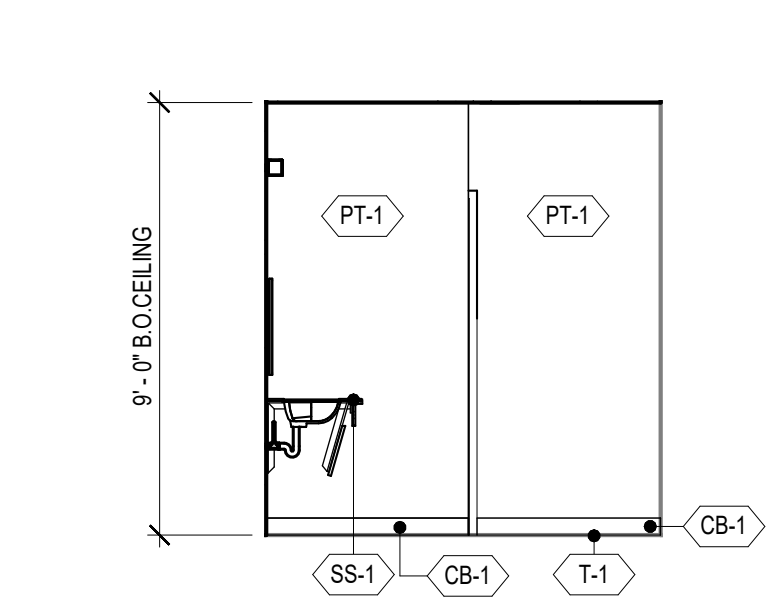


2
A-112
MENS RESTROOM
SCALE: 1/4" = 1'-0"

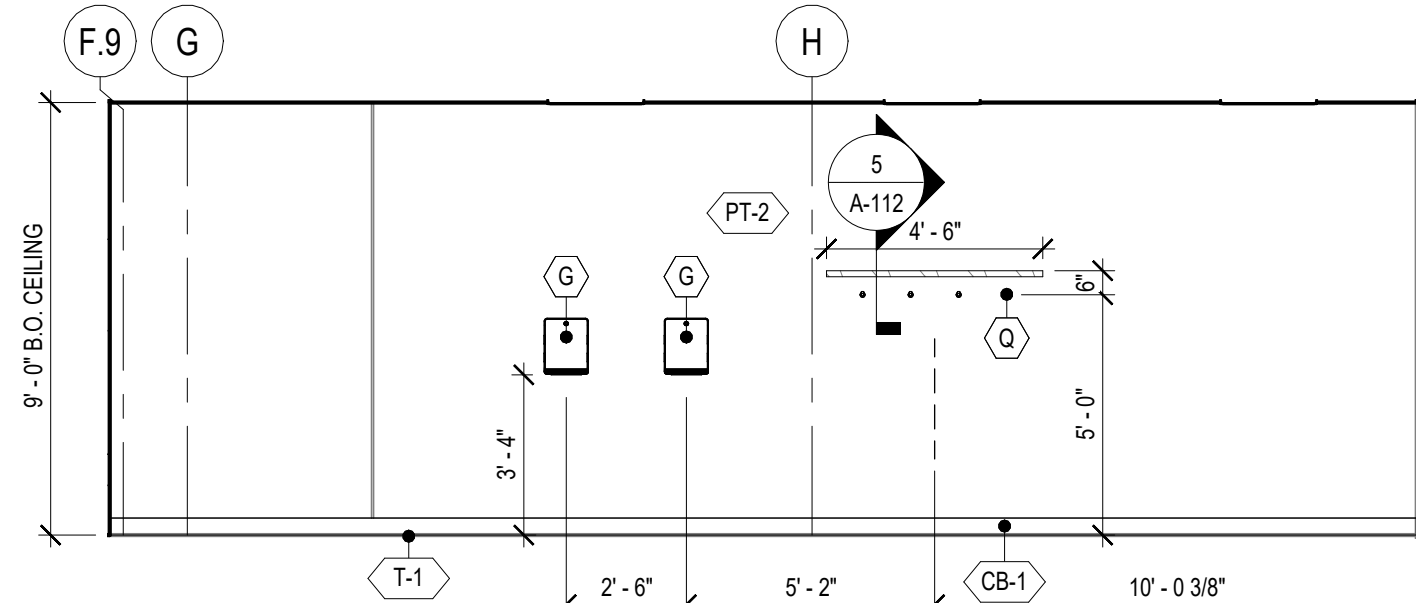


3
A-112
MENS RESTROOM
SCALE: 1/4" = 1'-0"

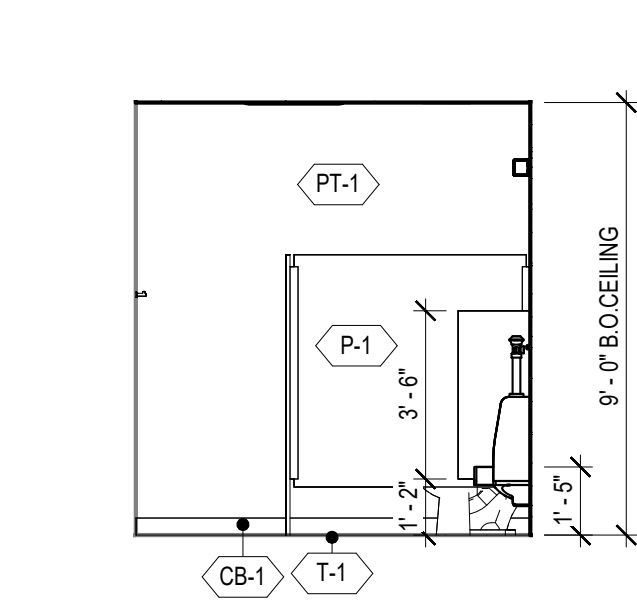


4
A-112
MENS RESTROOM
SCALE: 1/4" = 1'-0"

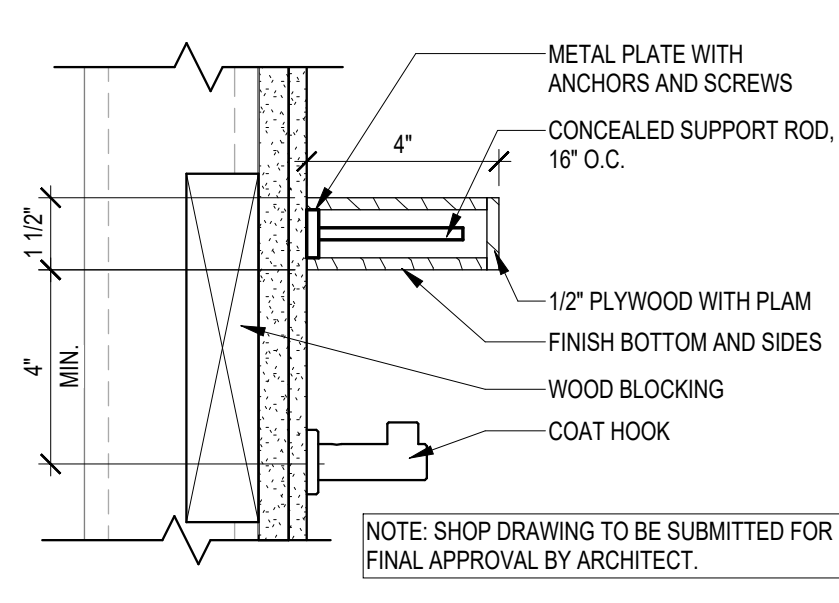


5
A-112
SHELF DETAIL
SCALE: 3" = 1'-0"

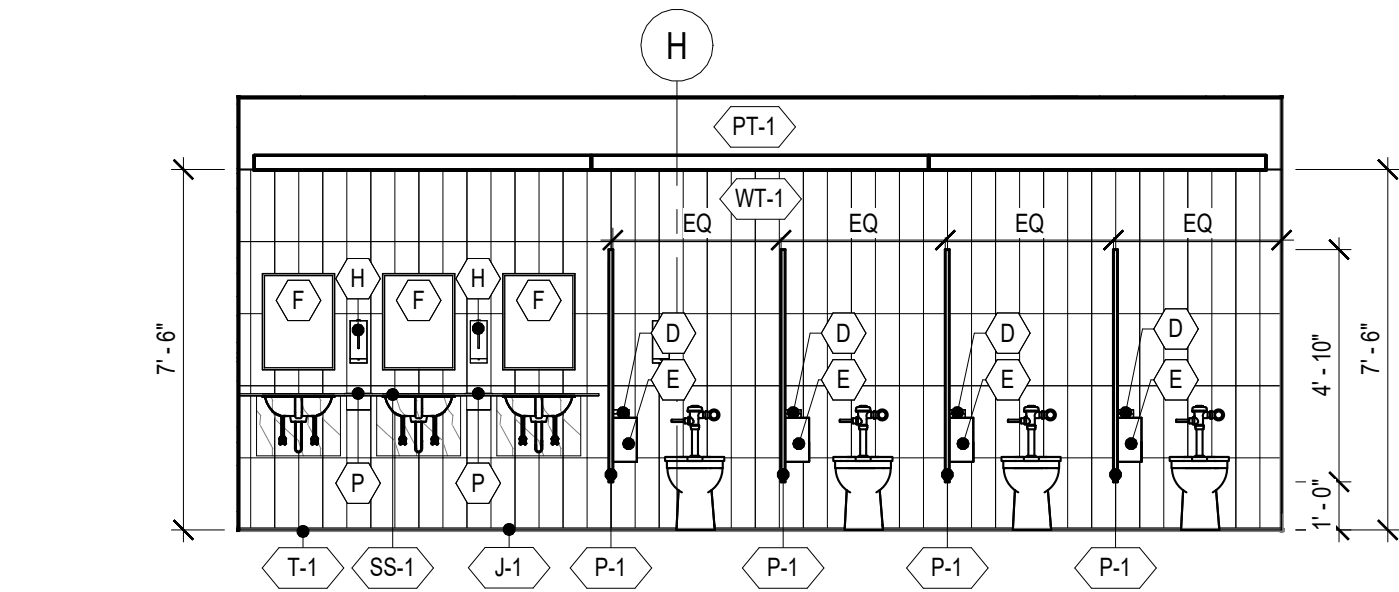


6
A-112
WOMENS RESTROOM
SCALE: 1/4" = 1'-0"

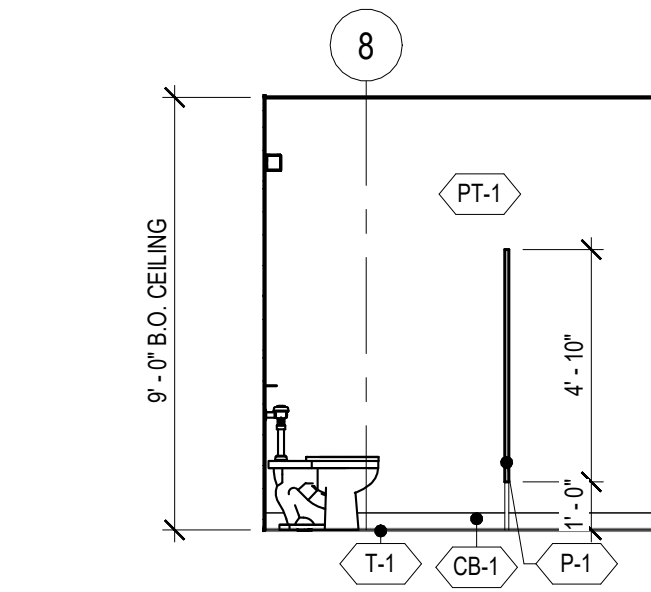


7
A-112
WOMENS RESTROOM
SCALE: 1/4" = 1'-0"

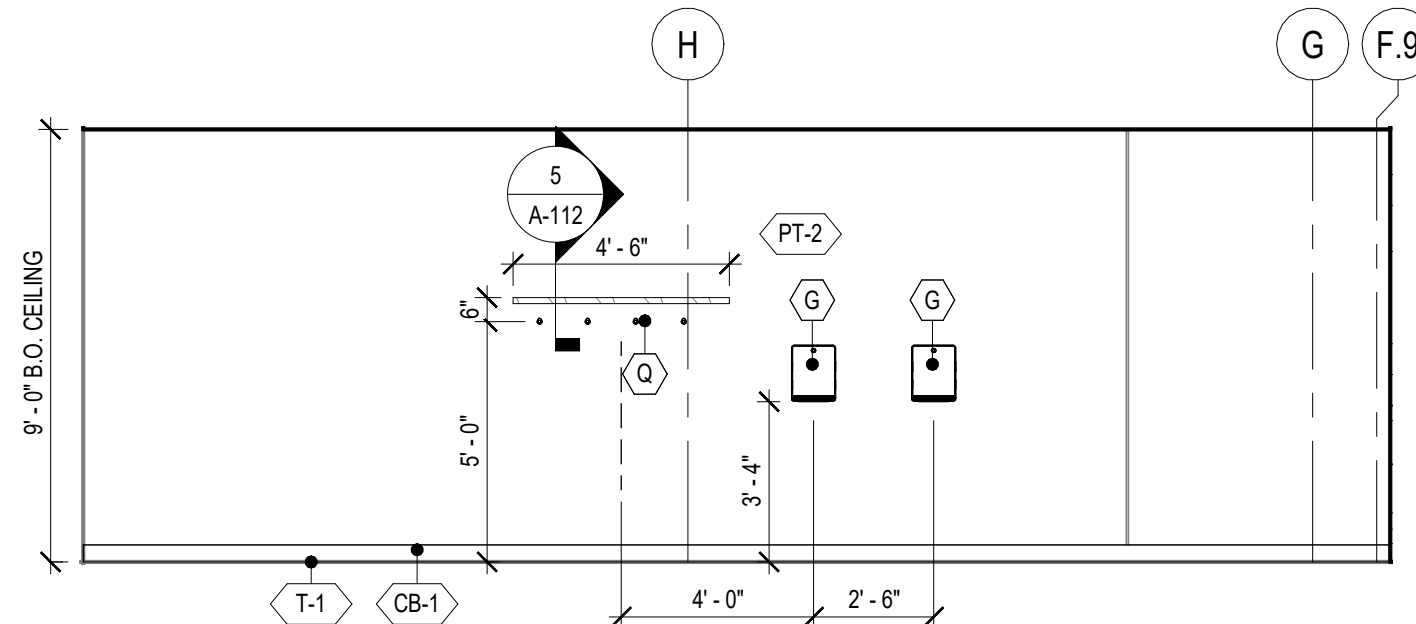

8
A-112
WOMENS RESTROOM
SCALE: 1/4" = 1'-0"

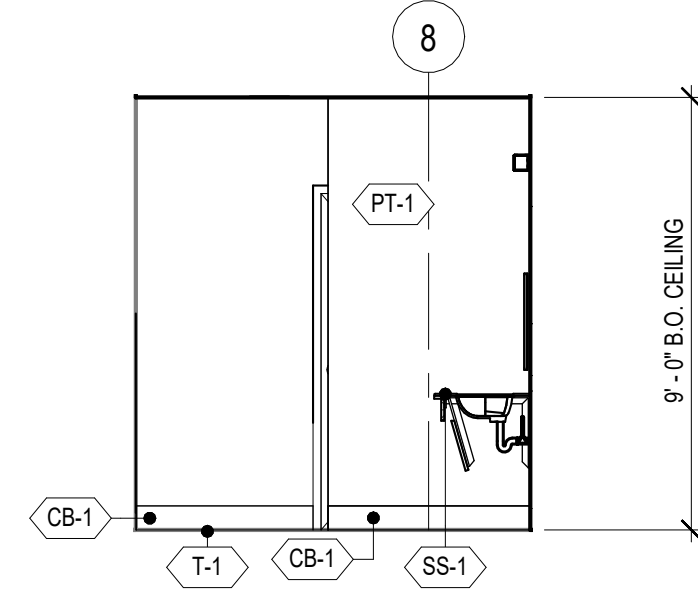

9
A-112
WOMENS RESTROOM
SCALE: 1/4" = 1'-0"

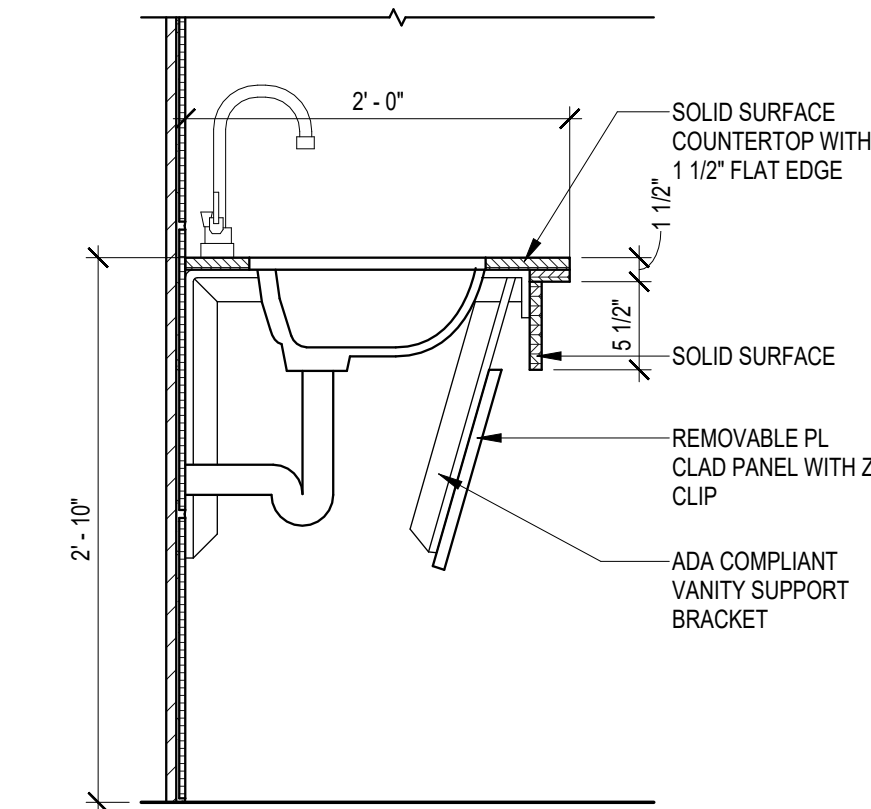

10
A-112
TYP. LAV BASE CAB
SCALE: 1" = 1'-0"

GENERAL NOTE:
REFER TO SHEET G-004 FOR MOUNTING HEIGHTS


DOOR AND FRAME SCHEDULE

DOOR NUMBER	LOCATION	DOOR			FRAME			FIRE RATING	HARDWARE SETS	NOTES
		TYPE	WIDTH	HEIGHT	THICKNESS	TYPE	HEAD			
AD101	MENS RESTROOM	WD-1	3'-0"	7'-0"	1 3/4"	TYP-2	4/A-602		06.02	2
AD102	WOMENS RESTROOM	WD-1	3'-0"	7'-0"	1 3/4"	TYP-2	4/A-602		06.02	2


GENERAL NOTE: REFER TO SHEET A-602 FOR DOOR AND FRAME TYPES.

NOTES:


- NOT USED
- UNDERCUT DOOR 1"

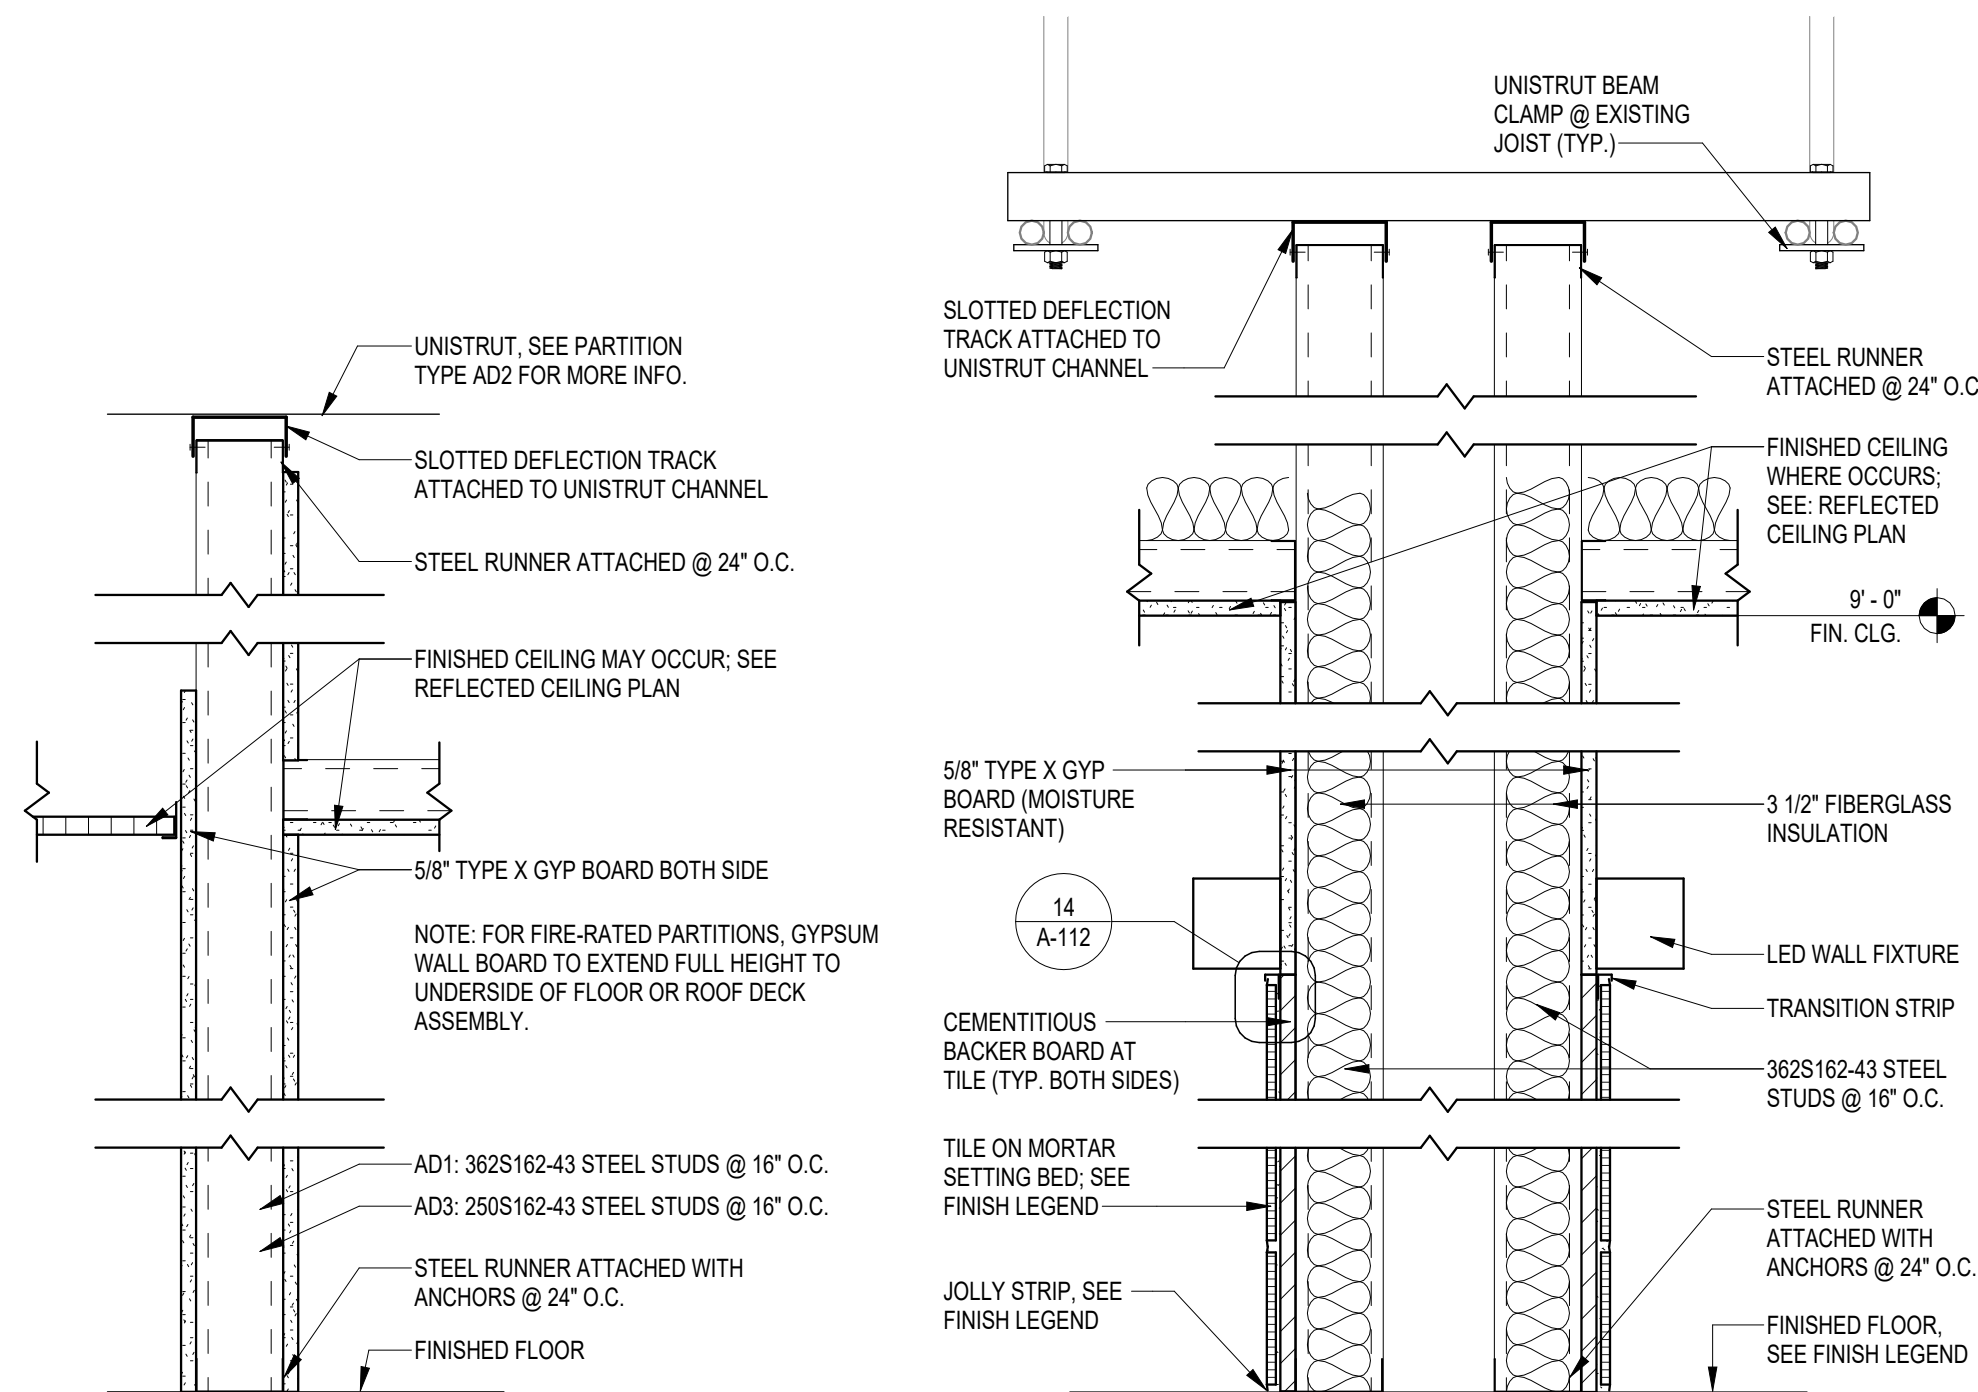


11
A-112
PARTITION TYPE AD1/AD3
SCALE: 1 1/2" = 1'-0"

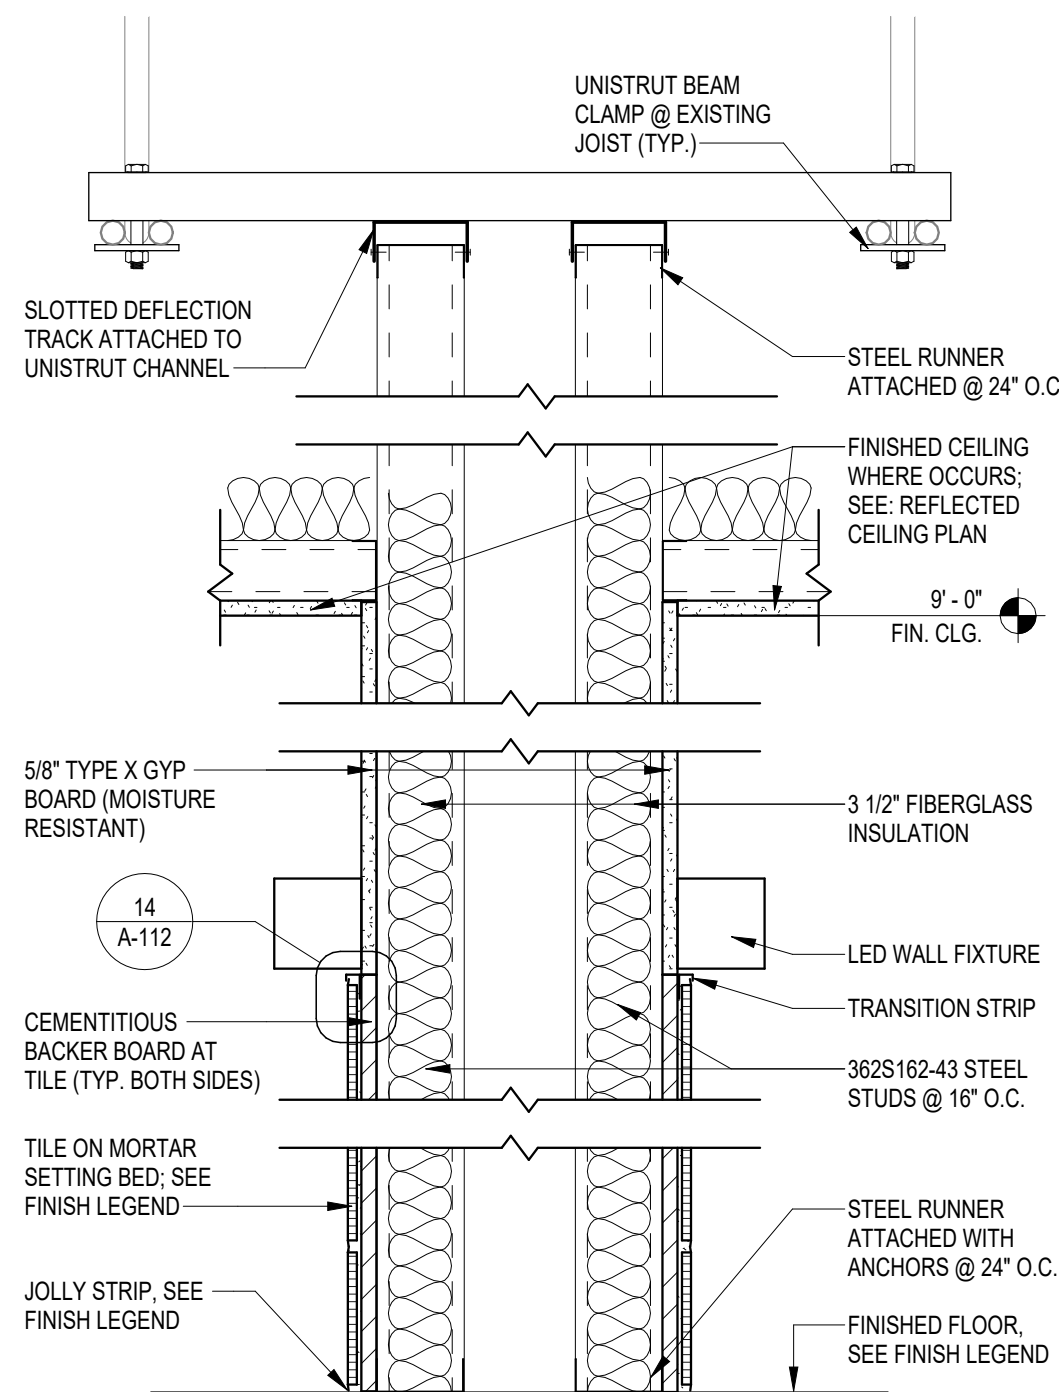

12
A-112
PARTITION TYPE AD2
SCALE: 1 1/2" = 1'-0"

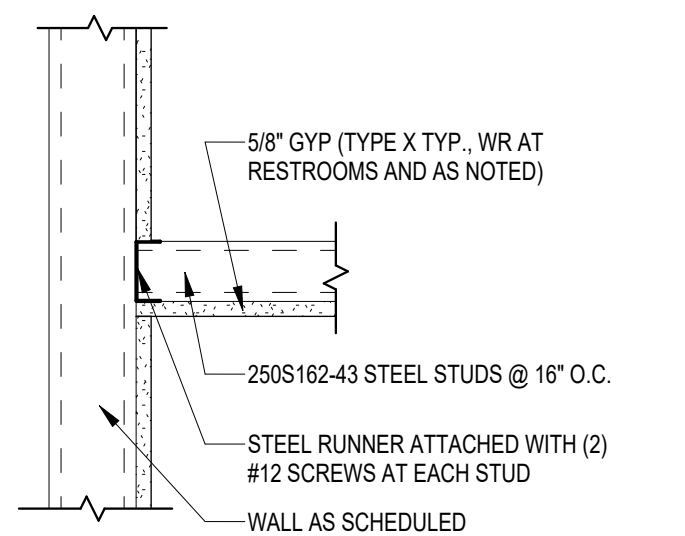

13
A-112
GYPSUM CEILING
SCALE: 1 1/2" = 1'-0"

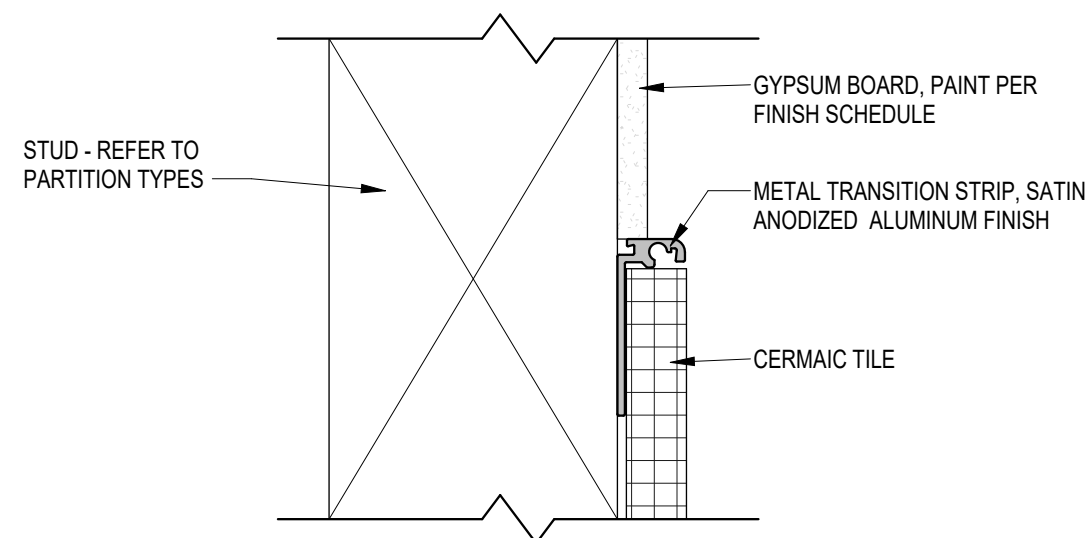

14
A-112
TRANSITION DETAIL - TILE TO GYP.
SCALE: 3" = 1'-0"

FINISH LEGEND:

FLOORING / COVE BASE MATERIALS:

T-1 BOD: PORCELAIN TILE - DALTILE - VOLUME 1.0, COLOR: THUNDER, SIZE: 12x24 - INSTALLATION METHOD: STRAIGHT SET
APPROVED EQUIVALENTS: MSI SURFACES - GRIS, COLOR: LOFT (NLOGR1224-N), SIZE: 12x24 SHAW CONTRACT GROUP - CEMENTED (CT78J), COLOR: ATMOSPHERE (00560), SIZE: 12x24

J-1 BOD: TRIM TILE - DALTILE - JOLLY, COLOR: TO MATCH T-1, SIZE: 1/2X12
APPROVED EQUIVALENTS: MSI SURFACES - QUARTER ROUND, COLOR TO MATCH SHAW CONTRACT GROUP - QUARTER ROUND, COLOR TO MATCH

CB-1 BOD: COVE BASE - DALTILE - VOLUME 1.0, COLOR: THUNDER, SIZE: 6X12
APPROVED EQUIVALENTS: MSI SURFACES - GRIS, BULLNOSE, COLOR: LOFT, SIZE: 3X18 SHAW CONTRACT GROUP - CEMENTED (CT81J), BULLNOSE, COLOR: ATMOSPHERE (00560), SIZE: 6X12

MISC:

P-1 BOD: TOILET PARTITIONS - BOBRICK - DURALINE, COLOR: CHARCOAL
APPROVED EQUIVALENTS: ASI GLOBAL PARTITIONS - COLOR THRU PHENOLIC, COLOR: CHARCOAL 8237
BRADLEY CORP. - PHENOLIC PRIVACY, COLOR: SLATE GREY D81

PL-1 BOD: LAMINATE - WILSONART - STANDARD LAMINATE, COLOR: NEO WALNUT 7991, FINE VELVET FINISH
APPROVED EQUIVALENTS: FORMICA - FORMAL WALNUT, 5782
ARBORITE - UPTOWN URBAN WALNUT, W474

SS-1 BOD: SOLID SURFACE COUNTERTOP - CORIAN - LAGUNA TERRAZZO
APPROVED EQUIVALENTS: WILSONART - BLUESTONE, 9074EA
FORMICA - TUMBLED GLASS, 413

WALL MATERIALS / FINISHES:

PT-1A BOD: BENJAMIN MOORE - SEMI-GLOSS - 860 APPARTITION
APPROVED EQUIVALENTS: SHERWIN WILLIAMS - EGGSHELL - COLOR APPROVED BY ARCHITECT
PPG - EGGSHELL - COLOR APPROVED BY ARCHITECT

PT-2A BOD: BENJAMIN MOORE - SEMI-GLOSS - 840 KENSINGTON BLUE
APPROVED EQUIVALENTS: SHERWIN WILLIAMS - EGGSHELL - COLOR APPROVED BY ARCHITECT
PPG - EGGSHELL - COLOR APPROVED BY ARCHITECT

PT-3A BOD: BENJAMIN MOORE - FLAT - WHITE (01) - DRYFALL
APPROVED EQUIVALENTS: SHERWIN WILLIAMS - FLAT - COLOR APPROVED BY ARCHITECT
PPG - FLAT - COLOR APPROVED BY ARCHITECT

PT-4A BOD: BENJAMIN MOORE - EGGSHELL - COLOR APPROVED BY ARCHITECT
APPROVED EQUIVALENTS: SHERWIN WILLIAMS - EGGSHELL - COLOR APPROVED BY ARCHITECT
PPG - EGGSHELL - COLOR APPROVED BY ARCHITECT

WT-1 BOD: RESTROOM WALL TILE - DALTILE - ANNAPOLIS REMIX, COLOR: SAIL MATTE, SIZE: 6x18 - INSTALLATION METHOD: VERTICAL, STRAIGHT SET
APPROVED EQUIVALENTS: AMERICAN OLEAN - COLORSTORY WALL, COLOR: MATTE DESIGNER WHITE, SIZE: 4x16

GENERAL NOTES:

BASIS OF DESIGN AND APPROVED EQUIVALENTS: THE MATERIALS, PRODUCTS, AND SYSTEMS INDICATED IN THE DRAWINGS AND SPECIFICATIONS ESTABLISH THE BASIS OF DESIGN. ALL PROPOSED ALTERNATES SHALL BE SUBMITTED WITH REQUIRED SAMPLES AND PRODUCT DATA.

NO ALTERNATES SHALL BE MADE WITHOUT THE WRITTEN APPROVAL OF THE ARCHITECT AND/OR INTERIOR DESIGNER. APPROVAL MUST BE OBTAINED PRIOR TO ORDERING OR INSTALLATION.

TOILET ROOM ACCESSORIES:

REFER TO A-111 AND A-112 FOR LOCATIONS

	MFGR. - USED FOR BASIS OF DESIGN SEE SPECS FOR EQUIVALENT MFGR.	ITEM DESCRIPTION
(A)	NOT USED	-
(B)	NOT USED	-
(C)	NOT USED	-
(D)	BOBRICK	SANITARY NAPKIN DISPOSAL, B-270, SURFACE MOUNTED, SATIN FINISH
(E)	BOBRICK	TOILET TISSUE DISPENSER, B-4288, SURFACE-MOUNTED, SATIN FINISH
(F)	BOBRICK	CHANNEL-FRAMED MIRROR, B-165x1824, BRIGHT POLISHED
(G)	BY OWNER	PAPER TOWEL DISPENSER OWNER SUPPLIED
(H)	BY OWNER	SOAP DISPENSER OWNER SUPPLIED
(I)	NOT USED	-
(J)	NOT USED	-
(K)	NOT USED	-
(L)	NOT USED	-
(M)	NOT USED	-
(N)	NOT USED	-
(O)	NOT USED	-
(P)	BOBRICK	CIRCULAR WASTE CHUTE, B-532, COUNTERTOP-MOUNTED, SATIN FINISH
(Q)	BOBRICK	COAT HOOK, B-5542, SURFACE-MOUNTED, SATIN FINISH STEEL

STATE OF MISSOURI MIKE KEHOE GOVERNOR

CASCO DIVERSIFIED CORPORATION
ARCHITECTURAL
LICENSE #: 000329
EXP. DATE: 12/31/25



Professional of Record:
MICHAEL S. SUNDERMEYER
LICENSE #: 2014026855
EXP. DATE: 12/31/26

CASCO

12 SUNNEDRIVE SUITE 100 ST. LOUIS, MO 63143
T 314.621.1100

OFFICE OF ADMINISTRATION DIVISION OF FACILITIES MANAGEMENT, DESIGN AND CONSTRUCTION

DEPARTMENT OF

MISSOURI STATE HIGHWAY PATROL

RENOVATIONS TO INTERIOR/EXTERIOR & INSTALL EMERGENCY GENERATOR, MULTIPLE ASSETS

MSHP GENERAL
HEADQUARTERS COMPLEX
1510 E. ELM STREET
JEFFERSON CITY, MO 65101

PROJECT # R2502-01

SITE # 6001

FACILITY #8136001006

REVISIONS

No. Description Date

ISSUE DATE: 12/16/25

DWG FILE #: 2404694

DRAWN BY: LAA

CHECKED BY: JVR

DESIGNED BY: RAR


SHEET TITLE:


ADMIN. RESTROOM PLANS
AND DETAILS ALTERNATE #1

SHEET NUMBER:


A-112

SHEET 28 OF 148
12/16/25

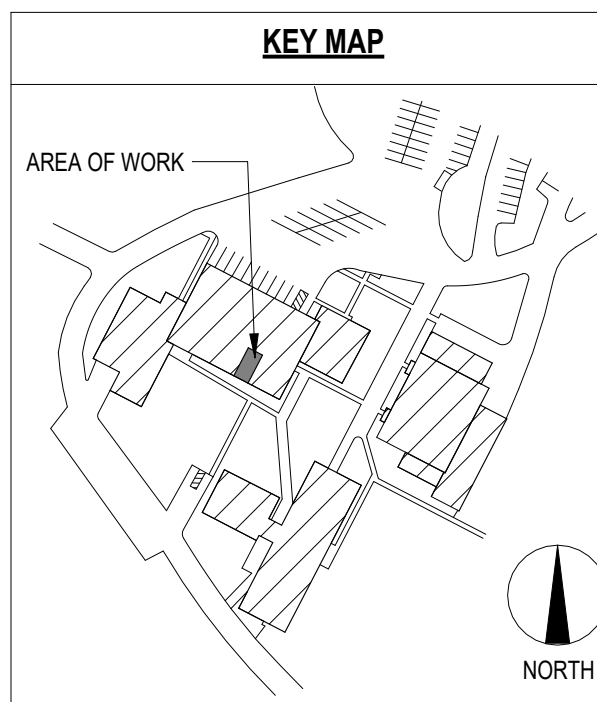

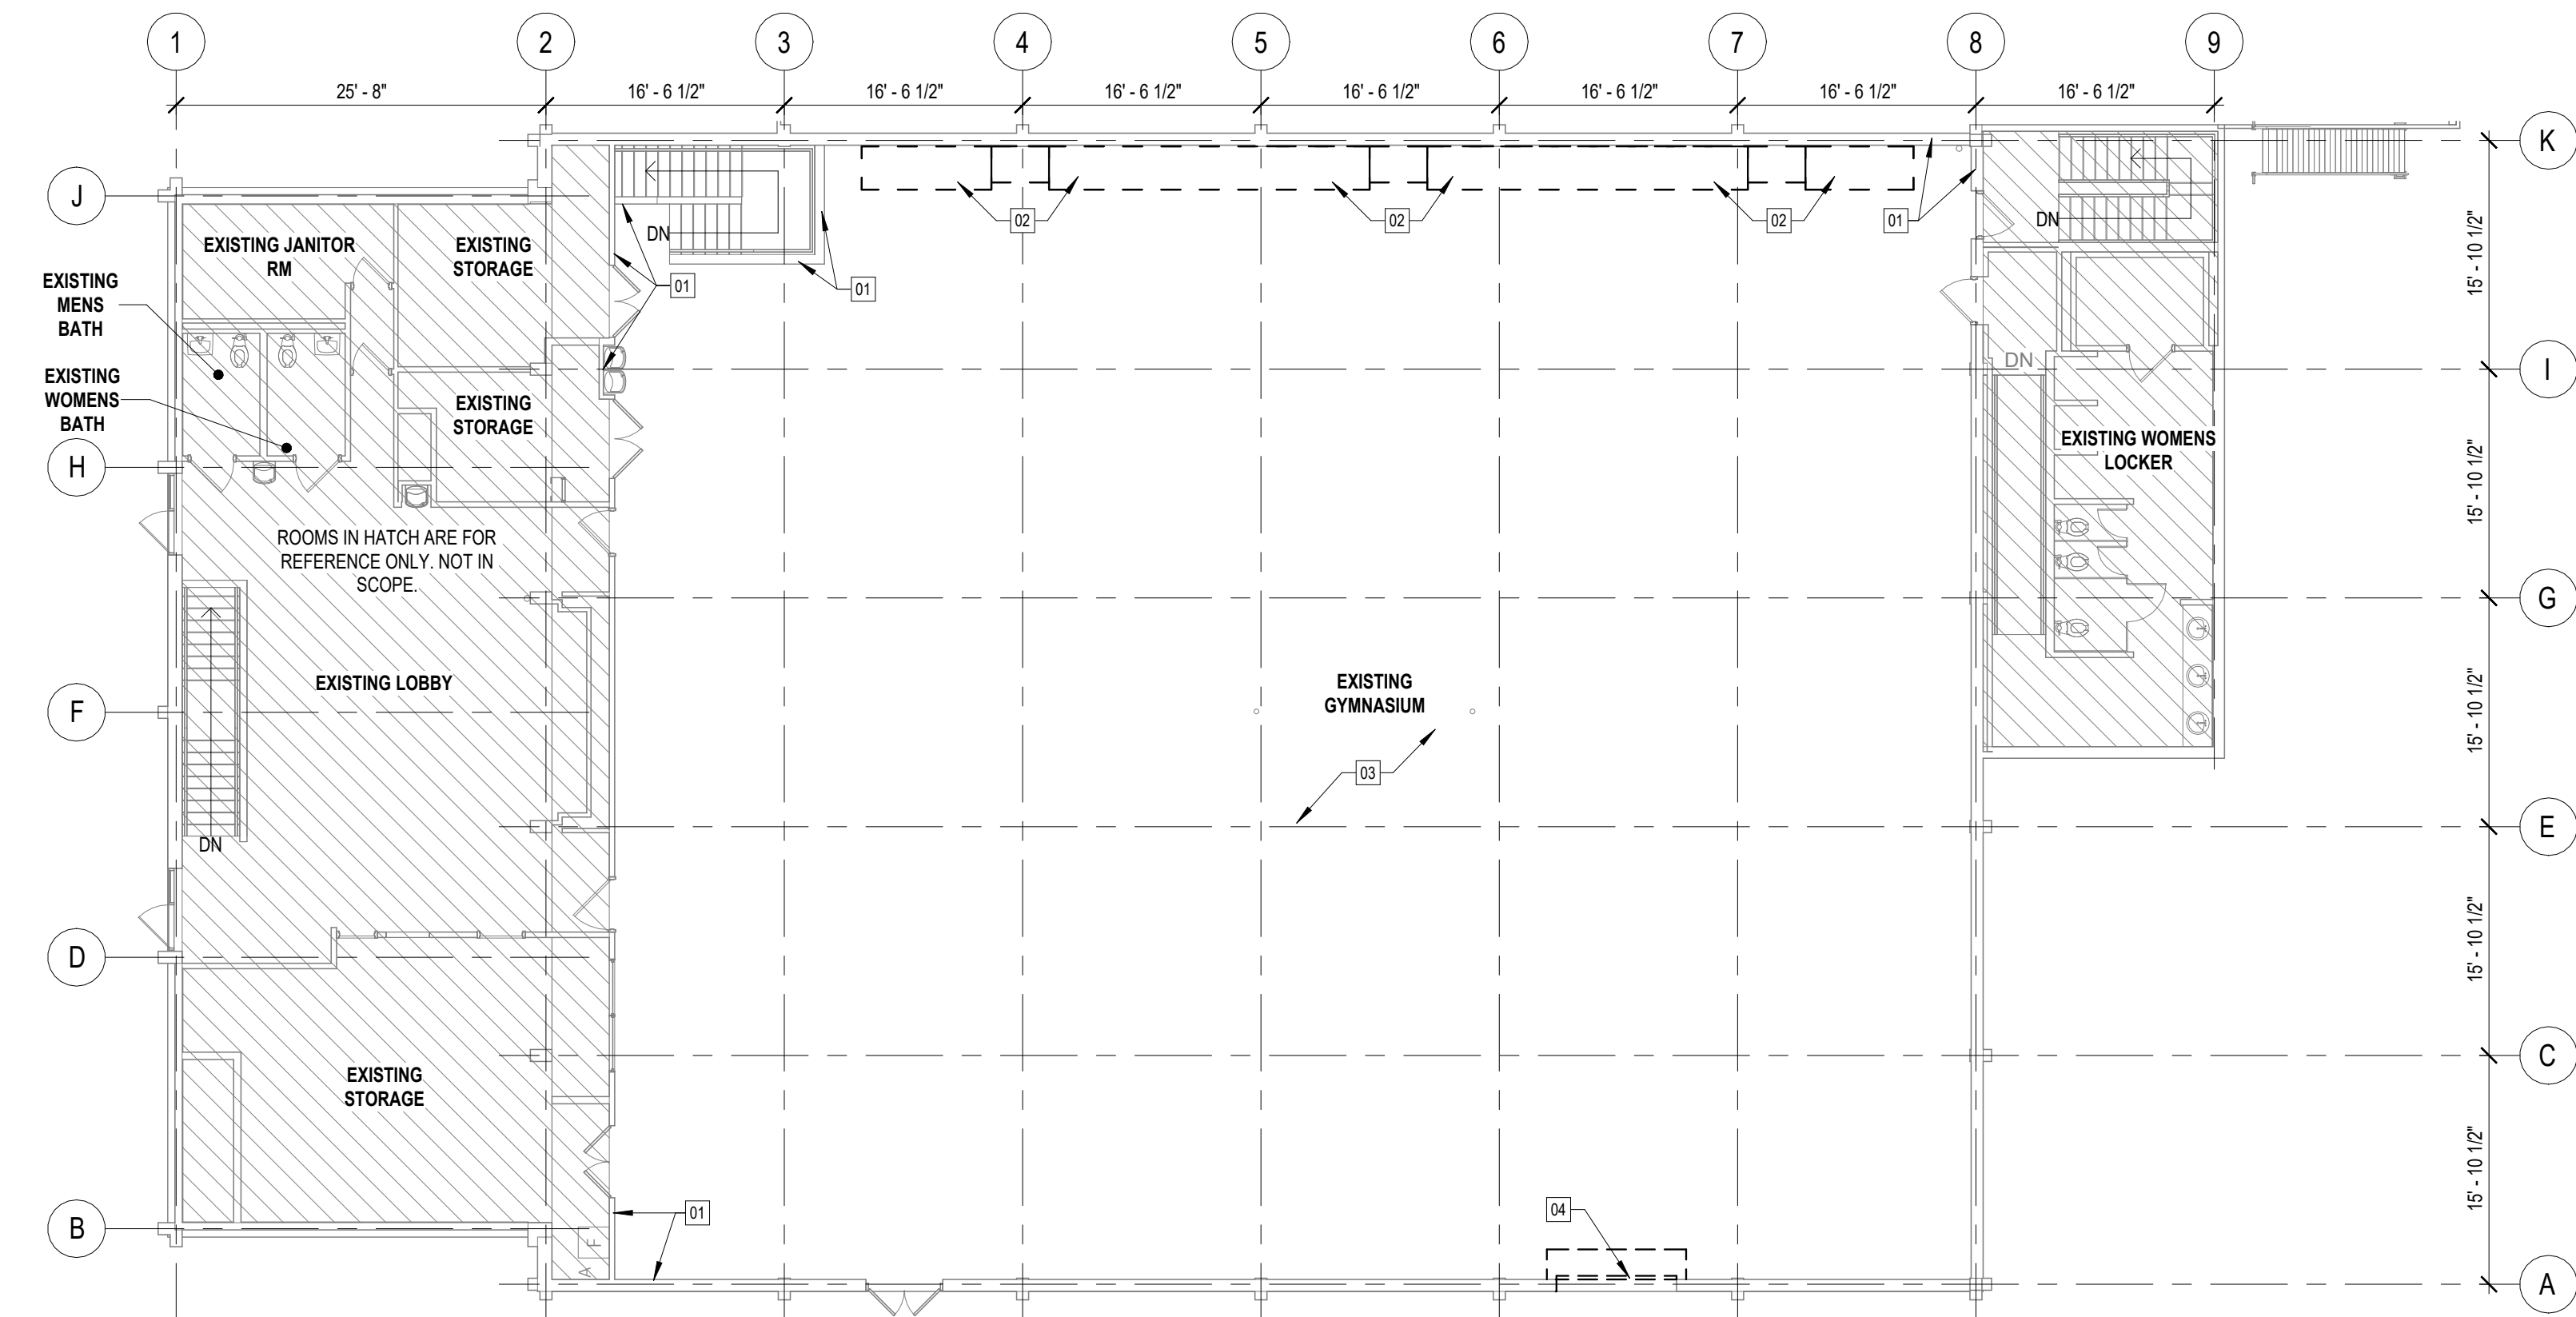

DEMOLITION - GYMNASIUM
SCALE: 3/32" = 1'-0"
TRUE NORTH BLDG NORTH

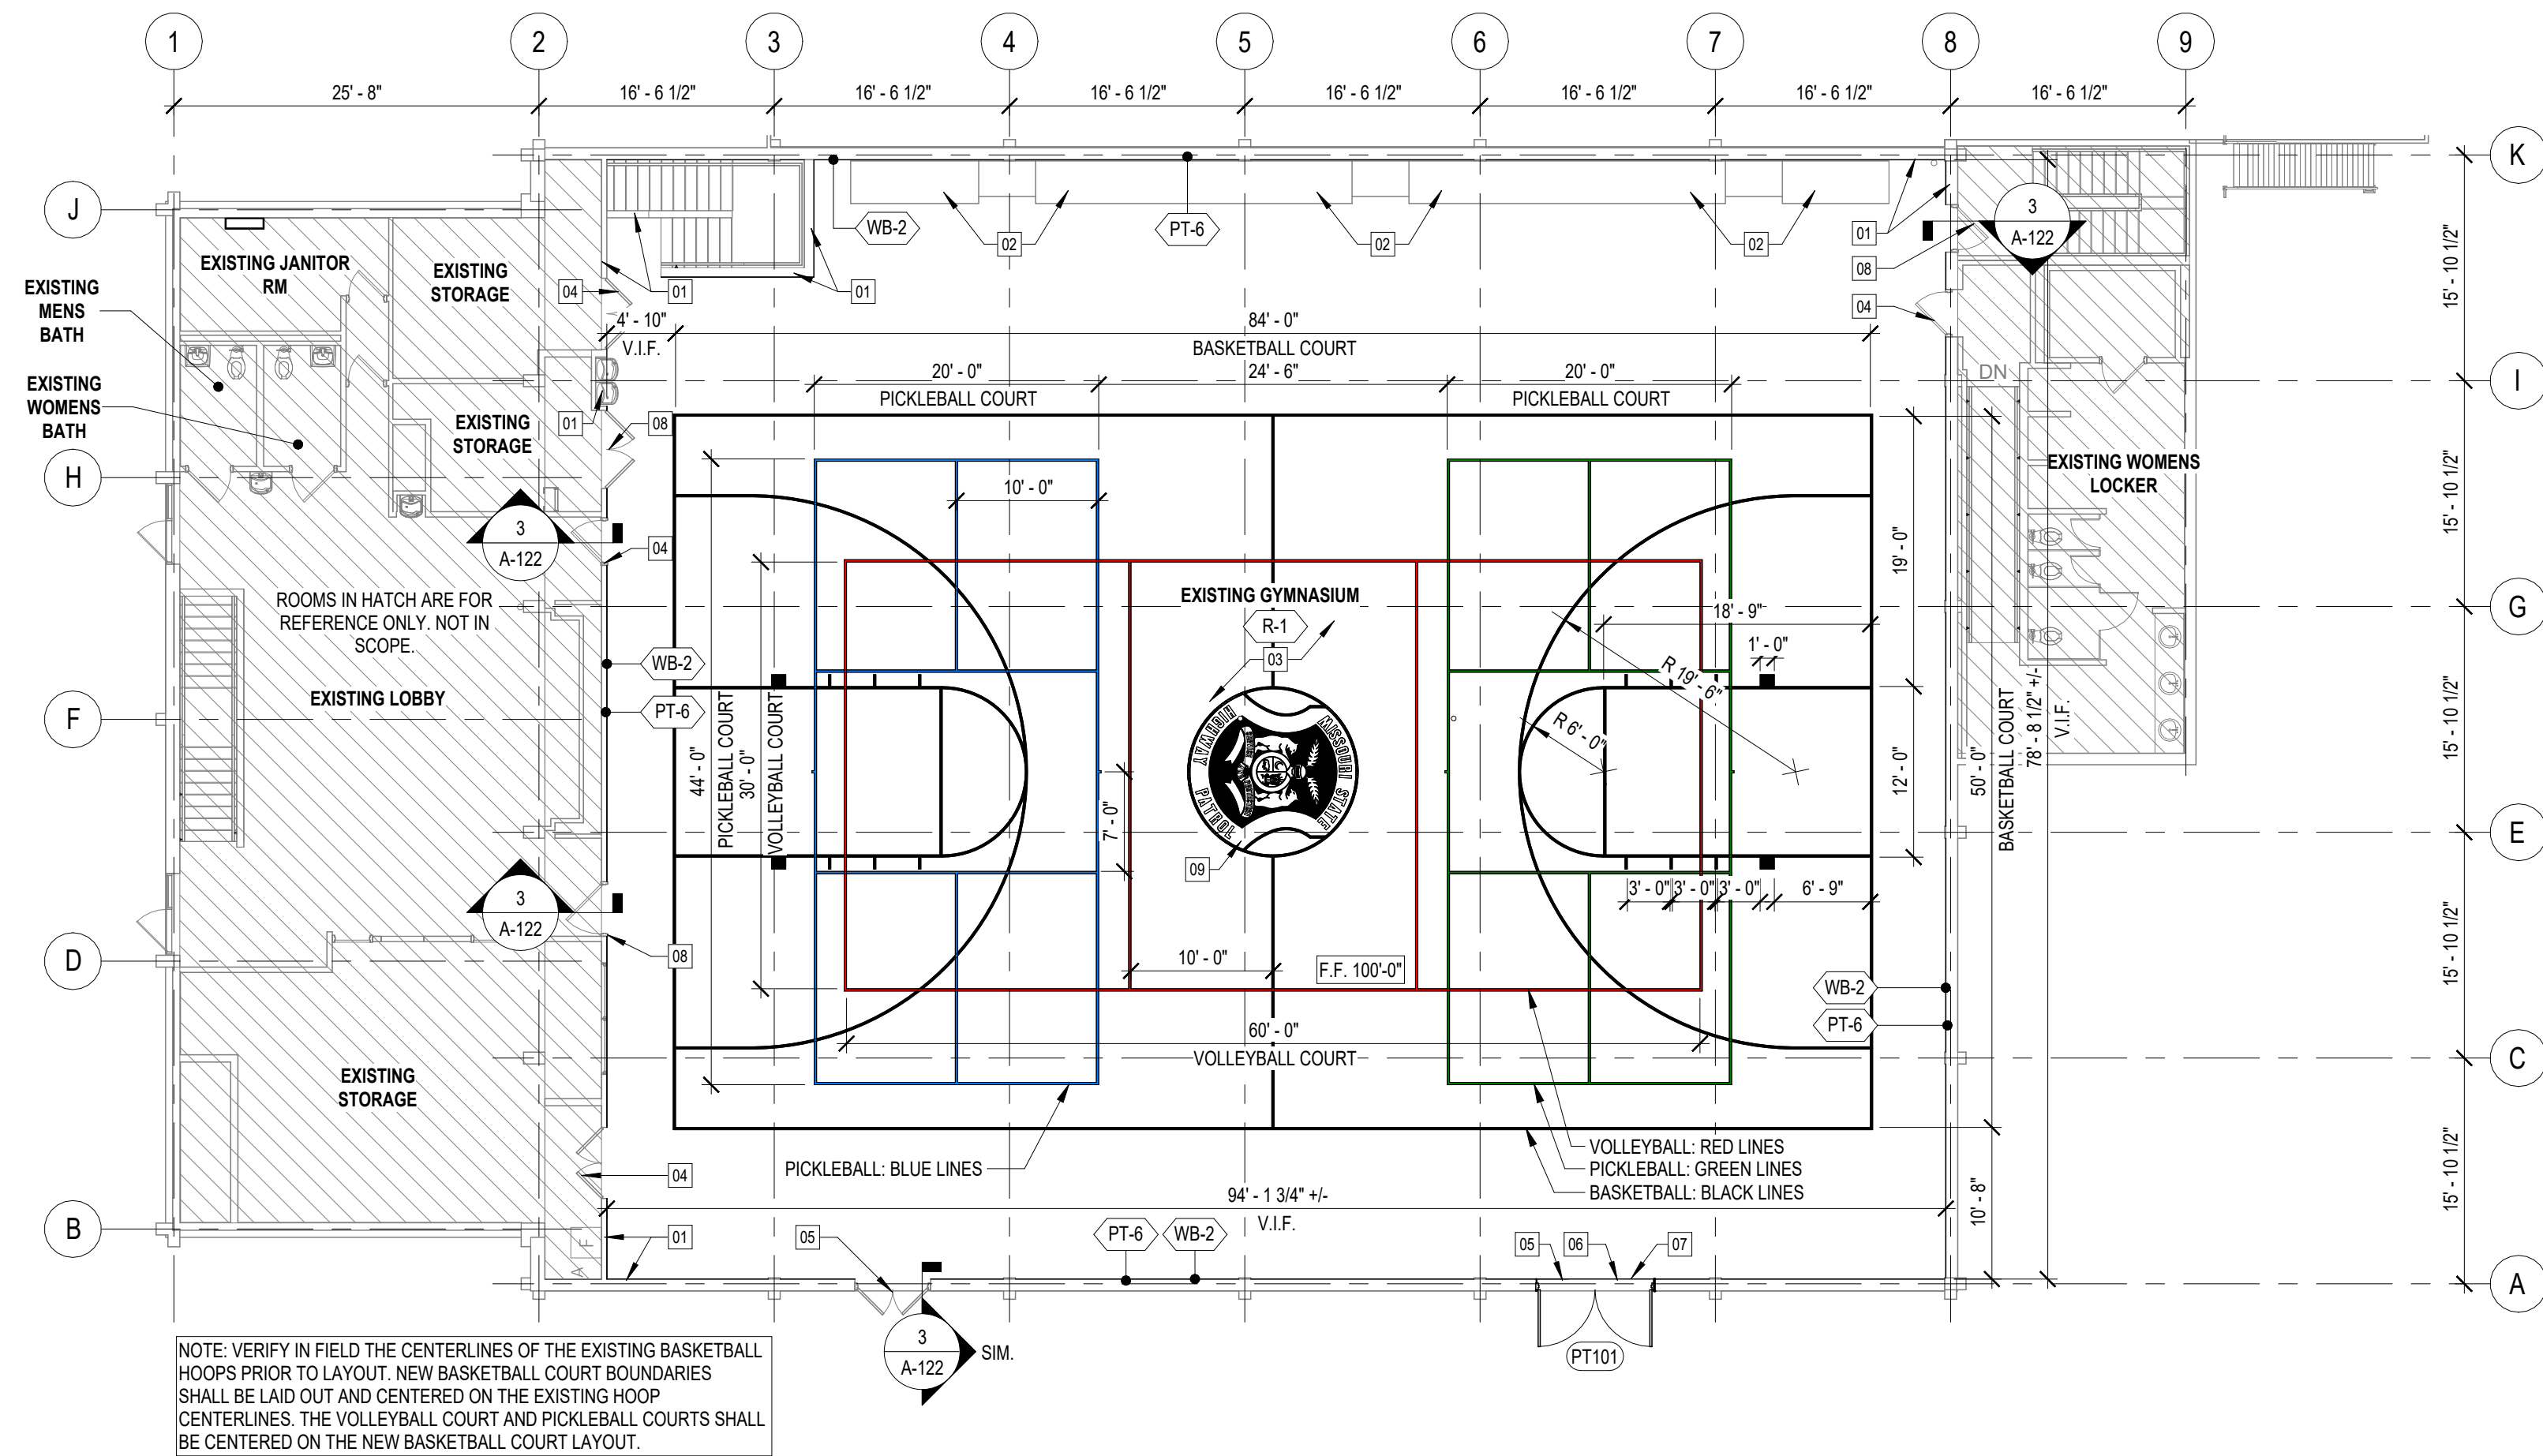

GYMNASIUM
SCALE: 3/32" = 1'-0"
TRUE NORTH BLDG NORTH

DEMOLITION PLAN LEGEND

- EXISTING CONSTRUCTION TO BE REMAIN
- EXISTING WALLS, DOORS, ETC. TO BE REMOVED
- AREA NOT IN SCOPE

DOOR AND FRAME SCHEDULE											
DOOR NUMBER	LOCATION	TYPE	DOOR			FRAME				FIRE RATING	HARDWARE SETS
			NOMINAL	WIDTH	HEIGHT	THICKNESS	TYPE	HEAD	JAMB	SILL	
PT101	EXISTING GYMNASIUM	HM-1(PR)	8'-0"	7'-4"	1'3 3/4"		TYP-1	3/A-602	6/A-602	8/A-602	09.08

GENERAL NOTE: REFER TO SHEET A-602 FOR DOOR AND FRAME TYPES.

NEW CONSTRUCTION PLAN LEGEND

- EXISTING CONSTRUCTION TO BE REMAIN
- AREA NOT IN SCOPE

FINISH LEGEND: MANUFACTURERS IDENTIFIED BELOW ARE BASIS OF DESIGN. REFER TO SPECS FOR EQUIVALENT MANUFACTURERS.

PT-6 BENJAMIN MOORE - EGGSHELL - OC-54 WHITE WISP


PT-7 BENJAMIN MOORE - SATIN - 1631 MIDNIGHT OIL - EXISTING & NEW DOORS & FRAMES

R-1 RESILIENT SHEET FLOORING - TARKETTSPO RTS - OMNISPORT MULTI-USE - COLOR: BEECH / SEE PLAN FOR KEYS & CENTER LINE COLORS

WB-2 RUBBER WALL BASE - JOHNSONITE - DURACOVE THERMOPLASTIC RUBBER - COLOR: BURN'T UMBER 63 - SIZE: 4" X 0.06

ALTERNATE NOTES:

1. REFER TO PAINT SPECIFICATIONS FOR DIFFERENT TYPES OF PRIMER AND PAINT FOR THE FOUR TYPES OF SUBSTRATES.

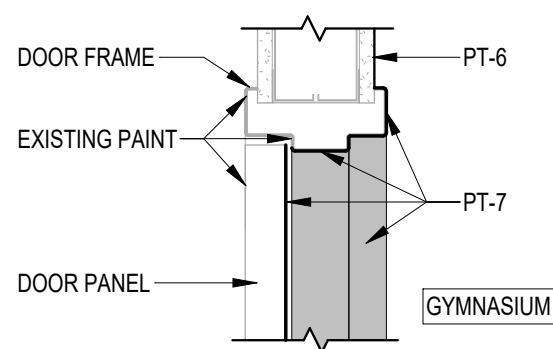

DOOR FRAME PAINT
SCALE: 1 1/2" = 1'-0"


- GENERAL DEMOLITION NOTES:**
- REFER TO DEMOLITION SPECIFICATIONS FOR ADDITIONAL INFORMATION.
 - REFER TO FLOOR PLAN ON THIS SHEET FOR PROPOSED NEW CONSTRUCTION.
 - ALL EXISTING MECHANICAL DIFFUSERS & DUCTWORK, ELECTRICAL DEVICES, LIGHTS, OUTLETS, SWITCHES & EQUIPMENT WHICH IS TO BE REMOVED SHALL BE IN ENTIRETY (WITHIN WALL PARTITIONS, CEILING SYSTEMS, ETC.) OR UNLESS NOTED OTHERWISE.
 - REFER TO STRUCTURAL, ELECTRICAL AND MECHANICAL DRAWINGS FOR ADDITIONAL DEMOLITION SCOPE AND REQUIREMENTS.
 - REMOVE ALL EXISTING SITE CONSTRUCTION AND DELETERIOUS MATERIALS UNLESS NOTED OTHERWISE.
 - ASBESTOS MATERIAL HAS BEEN IDENTIFIED IN THE 12X12 TILE MASTIC OF THE GYMNASIUM. SEE SPECIFICATIONS FOR ADDITIONAL INFORMATION.
 - DISPLAYS SUCH AS FLAGS AND POSTERS SHALL BE REMOVED AND STORED BY THE OWNER PRIOR TO THE START OF DEMOLITION. LARGER DISPLAYS AND OTHER WALL MOUNTED OBJECTS SHALL BE REMOVED AND STORED BY THE CONTRACTOR FOR REINSTALLATION.

- DEMO FIRST FLOOR KEYED NOTES**
- 01 EXISTING WALLS TO REMAIN. G.C. TO REMOVE WALL BASE. G.C. SHALL PATCH AND/OR REPAIR EXISTING WALL TO LIKE NEW CONDITION. G.C. TO PREPARE WALL TO RECEIVE NEW WALL BASE AND PAINT.
- 02 G.C. TO REMOVE EXISTING BLEACHERS. BLEACHERS ARE TO BE SALVAGED AND STORED FOR REUSE. G.C. TO REPLACE ANY MOUNTING HARDWARE THAT IS DAMAGED.
- 03 EXISTING FLOOR TO REMAIN. G.C. TO PREPARE EXISTING FLOOR FOR ENCAPSULATION. G.C. TO ENSURE FLOOR IS CLEAR OF DEBRI AND FLOOR MOUNTED ITEMS (TRIM, DOOR STOPS, ETC.) PRIOR TO ENCAPSULATION.
- 04 REMOVE EXISTING O.H. DOOR COMPLETE, INCLUDING THE FRAME, TRACKS, MOUNT HARDWARE, ETC.

- GENERAL CONSTRUCTION NOTES:**
- CONFLICTS BETWEEN SITE CONDITIONS AND DRAWINGS SHALL BE BROUGHT TO THE IMMEDIATE ATTENTION OF THE ARCHITECT.
 - ALL WORK SHALL BE ERECTED AND INSTALLED PLUMB, LEVEL, SQUARE AND TRUE AND IN PROPER ALIGNMENT, U.N.O.
 - ALL DIMENSIONS ARE TO FACE OF GYP BD. DIMENSIONS NOTED "HOLD" MUST BE ACCURATELY MAINTAINED, AND SHALL NOT VARY MORE THAN +/- 1/8" WITHOUT WRITTEN INSTRUCTION FROM ARCHITECT. "ALIGN" MEANS TO ACCURATELY LOCATE FINISHED FACES IN THE SAME PLANE. DIMENSIONS NOTED "CLEAR" ARE MINIMUM DIMENSIONS WHICH MUST BE MAINTAINED WITHOUT EXCEPTION. DIMENSIONS MARKED +/- MEAN A VARIANCE NOT GREATER THAN 1 INCH. VERIFY DIMENSIONS EXCEEDING TOLERANCE WITH THE ARCHITECT. ALL DIMENSIONS TO THE EXTERIOR WINDOWS WALL ARE TO THE FINISH FACE OF WALL BELOW SILL, U.N.O.
 - PATCH AT ALL NEW AND EXISTING PENETRATIONS AT FLOOR AND CEILING SLABS, WALLS AND SHAFTS. SEAL ABANDONED PENETRATIONS AT FLOOR, WALL AND SHAFTS TO MAINTAIN FIRE/SMOKE AND ACOUSTICAL RATINGS. CAP AND SEAL EXISTING STUB-INS IN SLAB AND PROVIDE SELF-LEVELING CONCRETE AS REQUIRED TO CREATE A LEVEL AND FLUSH SURFACE.
 - PROVIDE BLOCKING IN METAL STUD WALL FRAMING FOR SUPPORT OF CASEWORK, SHELF STANDARDS, AV DEVICES, FURNITURE, ETC. ALL CONCEALED LUMBER AND BLOCKING TO BE FIRE TREATED. COORDINATE BLOCKING REQUIREMENTS WITH FURNITURE AND AV INSTALLERS. WHERE BLOCKING OR ADDITIONAL STUDS ARE REQUIRED AT EXISTING WALLS, THEY ARE TO BE PATCHED AND REPAIRED.
 - ASBESTOS MATERIAL HAS BEEN IDENTIFIED IN THE 12X12 TILE MASTIC OF THE GYMNASIUM. SEE SPECIFICATIONS FOR ADDITIONAL INFORMATION.
 - ALL STORED OBJECTS ARE TO BE REINSTALLED BY THE CONTRACTOR AT THE COMPLETION OF CONSTRUCTION AND AFTER FINAL FINISHES HAVE BEEN APPLIED.
 - PRIME AND PAINT ALL WALL SURFACES, INCLUDING CONCRETE, G.W.B. AND BRICK. PRIME AND PAINT ALL EXPOSED TRIM, INCLUDING WOOD AND HOLLOW METAL. EXTEND WALL PAINT TO THE UNDERSIDE OF THE ROOF STRUCTURE AT THE STEEL TRUSS ANGLES. SEE FINISH SPECS FOR ADDITIONAL INFORMATION.
 - PROVIDE RECESSED COVER PLATES FOR EXISTING FLOOR OUTLETS. COVER PLATES SHALL BE INSTALLED FLUSH AND LEVEL WITH NEW FLOOR FINISH, WITH NO PROJECTION OR DEPRESSION THAT COULD CREATE A TRIPPING HAZARD. VERIFY IN FIELD SIZE AND LOCATIONS.

- FIRST FLOOR KEYED NOTES**
- 01 G.C. TO PAINT AND INSTALL NEW WALL BASE ON EXISTING WALLS. SEE FINISH SPECS.
- 02 G.C. TO INSTALL SAVED BLEACHERS IN THEIR ORIGINAL LOCATION.
- 03 G.C. TO APPLY A CLEAR, LIQUID ENCAPSULANT OVER THE EXISTING FLOOR PRIOR TO INSTALLING NEW GYM FLOORING. REFER TO FINISH SCHEDULE AND SPECIFICATIONS.
- 04 INSTALL NEW TRANSITION STRIP AT DOOR FRAME. PROVIDE NEW FINISH ACCORDING TO DETAIL 3/A122. REFER TO FINISH LEGEND ON THIS SHEET. G.C. TO ENSURE ALL DOORS PROPERLY FUNCTION WITH NEW ENCAPSULATED FLOOR. G.C. TO REPAIR/REPLACE ANY DOORS THAT NO LONGER FUNCTION U.N.O.
- 05 REMOVE EXISTING THRESHOLD AND REINSTALL AFTER FLOOR ENCAPSULATION AND NEW FLOORING IS INSTALLED.
- 06 INSTALL NEW H.M. DOOR, FRAME & HARDWARE. OUTSIDE FINISH TO MATCH EXISTING. REFER TO FINISH LEGEND FOR INTERIOR FINISH. SEE DETAILS ON SHEET A-602.
- 07 INSTALL NEW EXIT SIGNAGE TO EXISTING POWER.
- 08 INSTALL NEW TRANSITION STRIP AT DOOR FRAME. PROVIDE NEW FINISH ON INTERIOR SIDE ONLY. EXTERIOR EXISTING FINISH TO REMAIN. REFER TO FINISH LEGEND ON THIS SHEET. G.C. TO ENSURE ALL DOORS PROPERLY FUNCTION WITH NEW ENCAPSULATED FLOOR. G.C. TO REPAIR/REPLACE ANY DOORS THAT NO LONGER FUNCTION U.N.O.
- 09 12'-0" EMBLEM TO BE CENTERED IN BASKETBALL COURT. HIGHWAY PATROL EMBLEM IS FOR REFERENCE ONLY AND MAY NOT REPRESENT THE OFFICIAL DESIGN. THE CONTRACTOR SHALL COORDINATE WITH THE OWNER TO OBTAIN THE FINAL, APPROVED EMBLEM. THIS INCLUDES ALL GRAPHICS, COLORS, AND INSCRIPTIONS PRIOR TO INSTALLATION. SEE SPECS.

KEY MAP

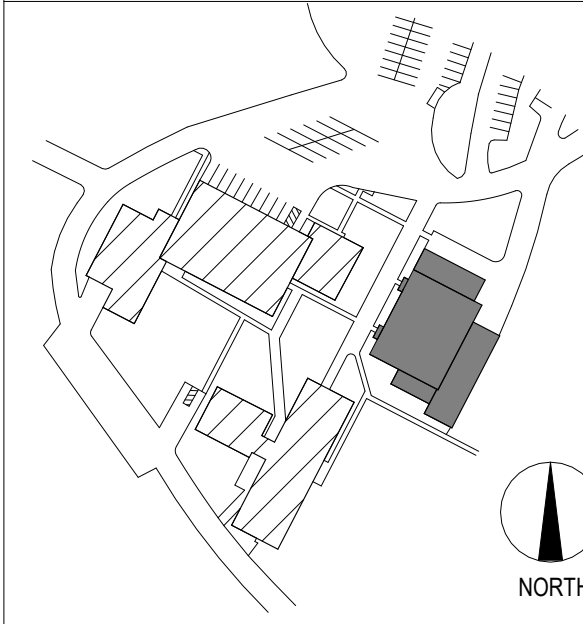

REVISIONS

No. Description Date

ISSUE DATE:12/16/25

DWG FILE #: 2404694
DRAWN BY: LAA
CHECKED BY: JVR
DESIGNED BY: RAR

SHEET TITLE:
PHYSICAL TRAINING DEMO
AND CONSTRUCTION PLAN
ALTERNATE #2

SHEET NUMBER:

A-122
SHEET 32 OF 148
12/16/25

DOOR AND FRAME SCHEDULE FLOOR 1

DOOR NUMBER	LOCATION	DOOR				FRAME				FIRE RATING	HARDWARE SETS	NOTES
		TYPE	WIDTH	NOMINAL HEIGHT	THICKNESS	TYPE	HEAD	DETAILS JAMB	SILL			
101A	DORM 101	WD-1	3'-0"	6'-8"	1 3/4"	EXIST	N/A	N/A	N/A		07.03	1
101B	RESTROOM 101B	WD-1	2'-0"	6'-8"	1 3/4"	EXIST	N/A	N/A	N/A		06.01	1 & 2
102	LAUNDRY ROOM 102	WD-1	2'-6"	6'-8"	1 3/4"	EXIST	N/A	N/A	N/A		05.01	1 & 2
103A	DORM 103	WD-1	3'-0"	6'-8"	1 3/4"	EXIST	N/A	N/A	N/A		07.03	1
103B	RESTROOM 101B	WD-1	2'-0"	6'-8"	1 3/4"	EXIST	N/A	N/A	N/A		06.01	1 & 2
104A	SINGLE BEDROOM 104A	WD-1	3'-0"	6'-8"	1 3/4"	TYP-2	4/A602	5/A602		3/4 HR	07.04	
104B	PRIVATE BATH 104B	WD-1	3'-0"	6'-8"	1 3/4"	TYP-2	4/A602	5/A602			06.01	2
104C	SINGLE BEDROOM 104	WD-2	3'-0"	6'-8"	1 3/4"	TYP-2	4/A602	5/A602			06.01	3
104D	CLOSET 104	WD-2 (PR)	3'-4"	6'-8"	1 3/4"	TYP-2	4/A602	5/A602			04.02	3
104E	CLOSET 104	WD-2 (PR)	3'-4"	6'-8"	1 3/4"	TYP-2	4/A602	5/A602			04.02	3
105A	DORM 105	WD-1	3'-0"	6'-8"	1 3/4"	EXIST	N/A	N/A		3/4 HR	07.04	1
105B	RESTROOM 105B	WD-1	2'-0"	6'-8"	1 3/4"	EXIST	N/A	N/A	N/A		06.01	1 & 2
107A	DORM 107	WD-1	3'-0"	6'-8"	1 3/4"	EXIST	N/A	N/A	N/A	3/4 HR	07.04	1
107B	RESTROOM 105B	WD-1	2'-0"	6'-8"	1 3/4"	EXIST	N/A	N/A	N/A		06.01	1 & 2
109A	DORM 109	WD-1	3'-0"	6'-8"	1 3/4"	EXIST	N/A	N/A	N/A	3/4 HR	07.04	1
109B	RESTROOM 109B	WD-1	2'-0"	6'-8"	1 3/4"	EXIST	N/A	N/A	N/A		06.01	1 & 2
110	STORAGE 110	WD-1	3'-0"	6'-8"	1 3/4"	EXIST	N/A	N/A	N/A	3/4 HR	09.05	1
111A	DORM 111	WD-1	3'-0"	6'-8"	1 3/4"	EXIST	N/A	N/A	N/A	3/4 HR	07.04	1
111B	RESTROOM 109B	WD-1	2'-0"	6'-8"	1 3/4"	EXIST	N/A	N/A	N/A		06.01	1 & 2
112A	VESTIBULE 112	AL-1 (PR)	6'-0"	7'-0"	1 3/4"	GLZ-A	10/A602	12/A602	9/A602		01.02	4
112B	VESTIBULE 112	AL-1 (PR)	6'-0"	7'-0"	1 3/4"	GLZ-B	12/A602 SIM	14/A602			04.01	
113	KITCHENETTE 113	WD-1	3'-0"	6'-8"	1 3/4"	EXIST	N/A	N/A	N/A		08.02	1
114	STORAGE 114	WD-1	3'-0"	6'-8"	1 3/4"	EXIST	N/A	N/A	N/A		09.02	1
115	UNISEX RESTROOM 115	WD-1	3'-0"	6'-8"	1 3/4"	EXIST	N/A	N/A	N/A		06.02	1 & 2
116	JANITOR CLOSET 116	WD-1	3'-0"	6'-8"	1 3/4"	EXIST	N/A	N/A	N/A		09.01	1 & 2
117	OFFICE 117	WD-1	3'-0"	6'-8"	1 3/4"	TYP-2	4/A602	5/A602			07.01	
118	OFFICE 118	WD-1	3'-0"	6'-8"	1 3/4"	TYP-2	4/A602	5/A602			07.01	
119	CONFERENCE ROOM 119	WD-1	3'-0"	6'-8"	1 3/4"	TYP-2	4/A602	5/A602			08.01	
120A	OFFICE 120	WD-1	3'-0"	6'-8"	1 3/4"	TYP-2	4/A602	5/A602			07.01	
120B	RESTROOM 120B	WD-1	3'-0"	6'-8"	1 3/4"	TYP-2	4/A602	5/A602			06.01	2
121	CONFERENCE ROOM 121	WD-1	3'-0"	6'-8"	1 3/4"	TYP-2	4/A602	5/A602			08.01	
122A	OFFICE 122	WD-1	3'-0"	6'-8"	1 3/4"	TYP-2	4/A602	5/A602			07.01	
122B	RESTROOM 120B	WD-1	3'-0"	6'-8"	1 3/4"	TYP-2	4/A602	5/A602			06.01	2
123A	OFFICE 123	WD-1	3'-0"	6'-8"	1 3/4"	TYP-2	4/A602	5/A602			07.01	
123B	RESTROOM 123B	WD-1	3'-0"	6'-8"	1 3/4"	TYP-2	4/A602	5/A602			06.01	2
124	STORAGE 124	WD-1	3'-0"	6'-8"	1 3/4"	EXIST	N/A	N/A	N/A	3/4 HR	09.06	1
125A	OFFICE 125	WD-1	3'-0"	6'-8"	1 3/4"	TYP-2	4/A602	5/A602		3/4 HR	07.04	
125B	RESTROOM 125B	WD-1	3'-0"	6'-8"	1 3/4"	TYP-2	4/A602	5/A602			06.01	2
126A	OFFICE 126	WD-1	3'-0"	6'-8"	1 3/4"	TYP-2	4/A602	5/A602		3/4 HR	07.04	
126B	RESTROOM 126B	WD-1	3'-0"	6'-8"	1 3/4"	TYP-2	4/A602	5/A602			06.01	2
127	CLASSROOM 127	WD-1	3'-0"	6'-8"	1 3/4"	TYP-2	4/A602	5/A602		3/4 HR	08.03	
128A	OFFICE 128	WD-1	3'-0"	6'-8"	1 3/4"	TYP-2	4/A602	5/A602		3/4 HR	07.04	
128B	RESTROOM 126B	WD-1	3'-0"	6'-8"	1 3/4"	TYP-2	4/A602	5/A602			06.01	2
129A	MECHANICAL ROOM 129	HM-1 (PR)	8'-0"	7'-0"	1 3/4"	TYP-1	SIM, 3/A602	7/A602	8/A602		05.04	
129B	MECHANICAL ROOM 129	EXIST	3'-0"	6'-8"	1 3/4"	EXIST	N/A	N/A	N/A		00.01	1
129C	MECHANICAL ROOM 129	EXIST	5'-0"	7'-0"	1 3/4"	EXIST	N/A	N/A	N/A		00.01	1
129D	STAIR	EXIST	3'-0"	6'-8"	1 3/4"	EXIST	N/A	N/A	N/A	3/4 HR	00.01	1
129F	MECHANICAL ROOM 129	EXIST	3'-0"	6'-8"	1 3/4"	EXIST	N/A	N/A	N/A		00.01	1
130A	CORRIDOR 130	HM-2	3'-0"	7'-0"	1 3/4"	TYP-1	3/A602	6/A602	8/A602	3/4 HR	01.01	4
130B	STAIR	EXIST	3'-0"	6'-8"	1 3/4"	EXIST	N/A	N/A	N/A	3/4 HR	00.01	1
130C	CORRIDOR 130	HM-2	3'-0"	6'-8"	1 3/4"	TYP-2	4/A602	5/A602		3/4 HR	05.02A	
133A	CORRIDOR 133	EXIST	3'-0"	7'-0"	1 3/4"	EXIST	N/A	N/A	N/A	3/4 HR	00.02	1 & 4
133B	STAIR	EXIST	3'-0"	6'-8"	1 3/4"	EXIST	N/A	N/A	N/A	3/4 HR	00.01	1
133C	CORRIDOR 133	HM-2	3'-0"	6'-8"	1 3/4"	TYP-2	4/A602	5/A602		3/4 HR	05.02A	

GENERAL NOTE: REFER TO SHEET A-602 FOR DOOR AND FRAME TYPES.

- NOTES:
- COORDINATE HARDWARE WITH OPENINGS ON EXIST. H.M. FRAMES
 - UNDERCUT DOOR 1"
 - 12" X 6" LOUVER
 - ACCESS/CARD READER, PROVIDE BY & INSTALLED BY OWNER, CONDUIT BY G.C.

STOREFRONT SCHEDULE

FRAME TYPE	LOCATION	ELEVATION	FINISH				GLAZING			FRAME			NOTES
			WIDTH (R.O.)	HEIGHT	FINISH	COLOR	THICK	TYPE	HEADER	JAMB	SILL		
GLZ-A	112-VESTIBULE	1/A-601	11'-8 1/2"	8'-0 1/2"	PRE-FINISHED ALUM.	ANODIZED ALUM.	1"	TEMPERED, INSULATED GLAZING	10/A602	12/A602 SIM.	12/A602		
GLZ-B	112-VESTIBULE	2/A-601	12'-2 5/8"	8'-5"	PRE-FINISHED ALUM.	ANODIZED ALUM.	1"	TEMPERED, INSULATED GLAZING	12/A602 SIM.	14/A602	12/A602		
GLZ-C	239-CORRIDOR	3/A-601	10'-8"	5'-5"	PRE-FINISHED ALUM.	ANODIZED ALUM.	1"	TEMPERED, INSULATED GLAZING	10/A602	11/A602 SIM.	11/A602		
GLZ-D	239-CORRIDOR	4/A-601	5'-2"	7'-4"	PRE-FINISHED ALUM.	ANODIZED ALUM.	1"	TEMPERED, INSULATED GLAZING	10/A602 SIM.	13/A602	12/A602		

GENERAL NOTES:

- 1" INSULATED GLAZING ASSEMBLIES SHALL BE PROVIDED WHICH MEETS OR EXCEEDS THE REQUIRED U-FACTOR AND SOLAR HEAT GAIN COEFFICIENT INDICATED IN THE PROJECT SPECIFIC ENVELOPE COMPLIANCE CERTIFICATE.
- G.C. TO VERIFY OPENING SIZES IN THE FIELD TO ENSURE PROPER FIT FOR NEW STOREFRONT SYSTEM AND ANY ASSOCIATED CLEARANCES (REFER TO HEADER, JAMB, AND SILL DETAILS).

DOOR AND FRAME SCHEDULE FLOOR 2

DOOR NUMBER	LOCATION	DOOR				FRAME				FIRE RATING	HARDWARE SETS	NOTES
		TYPE	WIDTH	HEIGHT	THICKNESS	TYPE	HEAD	DETAILS JAMB	SILL			
201A	DORM 201	WD-1	3'-0"	6'-8"	1 3/4"	EXIST	N/A	N/A	N/A		07.03	1
201B	RESTROOM 201B	WD-1	2'-0"	6'-8"	1 3/4"	EXIST	N/A	N/A	N/A		06.01	1 & 2
202A	DORM 202	WD-1	3'-0"	6'-8"	1 3/4"	EXIST	N/A	N/A	N/A		07.03	1
202B	RESTROOM 202B	WD-1	2'-0"	6'-8"	1 3/4"	EXIST	N/A	N/A	N/A		06.01	1 & 2
203A	DORM 203	WD-1	3'-0"	6'-8"	1 3/4"	EXIST	N/A	N/A	N/A		07.03	1
203B	RESTROOM 203B	WD-1	2'-0"	6'-8"	1 3/4"	EXIST	N/A	N/A	N/A		06.01	1 & 2
204A	DORM 204	WD-1	3'-0"	6'-8"	1 3/4"	EXIST	N/A	N/A	N/A		07.03	1
204B	RESTROOM 202B	WD-1	2'-0"	6'-8"	1 3/4"	EXIST	N/A	N/A	N/A		06.01	1 & 2
205A	DORM 205	WD-1	3'-0"	6'-8"	1 3/4"	EXIST	N/A	N/A	N/A	3/4 HR	07.03	1
205B	RESTROOM 203B	WD-1	2'-0"	6'-8"	1 3/4"	EXIST	N/A	N/A	N/A		06.01	1 & 2
206A	DORM 206	WD-1	3'-0"	6'-8"	1 3/4"	EXIST	N/A	N/A	N/A	3/4 HR	07.03	1
206B	RESTROOM 206B	WD-1	2'-0"	6'-8"	1 3/4"	EXIST	N/A	N/A	N/A		06.01	1 & 2
207A	DORM 207	WD-1	3'-0"	6'-8"	1 3/4"	EXIST	N/A	N/A	N/A	3/4 HR	07.03	1
207B	RESTROOM 207B	WD-1	2'-0"	6'-8"	1 3/4"	EXIST	N/A	N/A	N/A		06.01	1 & 2
208A	DORM 208	WD-1	3'-0"	6'-8"	1 3/4"	EXIST	N/A	N/A	N/A	3/4 HR	07.03	1
208B	RESTROOM 206B	WD-1	2'-0"	6'-8"	1 3/4"	EXIST	N/A	N/A	N/A		06.01	1 & 2
209A	DORM 209	WD-1	3'-0"	6'-8"	1 3/4"	EXIST	N/A	N/A	N/A	3/4 HR	07.03	1
209B	RESTROOM 207B	WD-1	2'-0"	6'-8"	1 3/4"	EXIST	N/A	N/A	N/A		06.01	1 & 2
210A	DORM 210	WD-1	3'-0"	6'-8"	1 3/4"	EXIST	N/A	N/A	N/A		07.03	1
210B	RESTROOM 210B	WD-1	2'-0"	6'-8"	1 3/4"	EXIST	N/A	N/A	N/A		06.01	1 & 2
211A	DORM 211	WD-1	3'-0"	6'-8"	1 3/4"	EXIST	N/A	N/A	N/A		07.03	1
211B	RESTROOM 211B	WD-1	2'-0"	6'-8"	1 3/4"	EXIST	N/A	N/A	N/A		06.01	1 & 2
212A	DORM 212	WD-1	3'-0"	6'-8"	1 3/4"	EXIST	N/A	N/A	N/A		07.03	1
212B	RESTROOM 210B	WD-1	2'-0"	6'-8"	1 3/4"	EXIST	N/A	N/A	N/A		06.01	1 & 2
213A	DORM 213	WD-1	3'-0"	6'-8"	1 3/4"	EXIST	N/A	N/A	N/A		07.03	1
213B	RESTROOM 211B	WD-1	2'-0"	6'-8"	1 3/4"	EXIST	N/A	N/A	N/A		06.01	1 & 2
214A	DORM 214	WD-1	3'-0"	6'-8"	1 3/4"	EXIST	N/A	N/A	N/A		07.03	1
214B	RESTROOM 214B	WD-1	2'-0"	6'-8"	1 3/4"	EXIST	N/A	N/A	N/A		06.01	1 & 2
215A	PRIVATE DORM 215	WD-1	3'-0"	6'-8"	1 3/4"	TYP-2	4/A602	5/A602			07.02	
215B	PRIVATE RESTROOM 215B	WD-1	3'-0"	6'-8"	1 3/4"	TYP-2	4/A602	5/A602			06.01	2
216A	DORM 216	WD-1	3'-0"	6'-8"	1 3/4"	EXIST	N/A	N/A	N/A		07.03	1
216B	RESTROOM 214B	WD-1	2'-0"	6'-8"	1 3/4"	EXIST	N/A	N/A	N/A		06.01	1 & 2
217A	DORM 217	WD-1	3'-0"	6'-8"	1 3/4"	EXIST	N/A	N/A	N/A		07.03	1
217B	RESTROOM 217B	WD-1	2'-0"	6'-8"	1 3/4"	EXIST	N/A	N/A	N/A		06.01	1 & 2
218A	DORM 218	WD-1	3'-0"	6'-8"	1 3/4"	EXIST	N/A	N/A	N/A		07.03	1
218B	RESTROOM 218B	WD-1	2'-0"	6'-8"	1 3/4"	EXIST	N/A	N/A	N/A		06.01	1 & 2
219A	DORM 219	WD-1	3'-0"	6'-8"	1 3/4"	EXIST	N/A	N/A	N/A		07.03	1
219B	RESTROOM 217B	WD-1	2'-0"	6'-8"	1 3/4"	EXIST	N/A	N/A	N/A		06.01	1 & 2
220A	DORM 220	WD-1	3'-0"	6'-8"	1 3/4"	EXIST	N/A	N/A	N/A		07.03	1
220B	RESTROOM 218B	WD-1	2'-0"	6'-8"	1 3/4"	EXIST	N/A	N/A	N/A		06.01	1 & 2
221A	DORM 221	WD-1	3'-0"	6'-8"	1 3/4"	EXIST	N/A	N/A	N/A		07.03	1
221B	RESTROOM 221'B	WD-1	2'-0"	6'-8"	1 3/4"	EXIST	N/A	N/A	N/A		06.01	1 & 2
222A	DORM 222	WD-1	3'-0"	6'-8"	1 3/4"	EXIST	N/A	N/A	N/A		07.03	1
222B	RESTROOM 222B	WD-1	2'-0"	6'-8"	1 3/4"	EXIST	N/A	N/A	N/A		06.01	1 & 2
223A	DORM 223	WD-1	3'-0"	6'-8"	1 3/4"	EXIST	N/A	N/A	N/A		07.03	1
223B	RESTROOM 221B	WD-1	2'-0"	6'-8"	1 3/4"	EXIST	N/A	N/A	N/A		06.01	1 & 2
224A	DORM 224	WD-1	3'-0"	6'-8"	1 3/4"	EXIST	N/A	N/A	N/A		07.03	1
224B	RESTROOM 222B	WD-1	2'-0"	6'-8"	1 3/4"	EXIST	N/A	N/A	N/A		06.01	1 & 2
225A	DORM 225	WD-1	3'-0"	6'-8"	1 3/4"	EXIST	N/A	N/A	N/A		07.03	1
225B	RESTROOM 225B	WD-1	2'-0"	6'-8"	1 3/4"	EXIST	N/A	N/A	N/A		06.01	1 & 2
226A	ACCESSIBLE DORM 226	WD-1	3'-0"	6'-8"	1 3/4"	EXIST	N/A	N/A	N/A		07.02	1
226B	ACCESSIBLE RESTROOM 226B	WD-1	3'-0"	6'-8"	1 3/4"	EXIST	N/A	N/A	N/A		06.01	1 & 2
227A	DORM 227	WD-1	3'-0"	6'-8"	1 3/4"	EXIST	N/A	N/A	N/A		07.03	1
227B	RESTROOM 225B	WD-1	2'-0"	6'-8"	1 3/4"	EXIST	N/A	N/A	N/A		06.01	1 & 2
228A	DORM 228	WD-1	3'-0"	6'-8"	1 3/4"	EXIST	N/A	N/A	N/A		07.03	1
228B	RESTROOM 228B	WD-1	2'-0"	6'-8"	1 3/4"	EXIST	N/A	N/A	N/A		06.01	1 & 2
229A	DORM 229	WD-1	3'-0"	6'-8"	1 3/4"	EXIST	N/A	N/A	N/A		07.03	1
229B	RESTROOM 229B	WD-1	2'-0"	6'-8"	1 3/4"	EXIST	N/A	N/A	N/A		06.01	1 & 2
230A	DORM 230	WD-1	3'-0"	6'-8"	1 3/4"	EXIST	N/A	N/A	N/A		07.03	1
230B	RESTROOM 228B	WD-1	2'-0"	6'-8"	1 3/4"	EXIST	N/A	N/A	N/A		06.01	1 & 2
231A	DORM 231	WD-1	3'-0"	6'-8"	1 3/4"	EXIST	N/A	N/A	N/A		07.03	1
231B	RESTROOM 229B	WD-1	2'-0"	6'-8"	1 3/4"	EXIST	N/A	N/A	N/A		06.01	1 & 2
232A	LIVING ROOM 232	WD-1	3'-0"	6'-8"	1 3/4"	TYP-2	4/A602	5/A602			07.03	
232B	RESTROOM 232B	WD-1	3'-0"	6'-8"	1 3/4"	TYP-2	4/A602	5/A602			06.01	2
232C	BEDROOM 232	WD-1	3'-0"	6'-8"	1 3/4"	TYP-2	4/A602	5/A602			06.01	
233A	STAIR	EXIST	3'-0"	6'-8"	1 3/4"	EXIST	N/A	N/A	N/A	3/4 HR	00.01	1
233B	CORRIDOR 240	HM-2	3'-0"	6'-8"	1 3/4"	TYP-2	4/A602	5/A602		3/4 HR	05.02	
234	UNISEX RESTROOM 234	WD-2	3'-0"	6'-8"	1 3/4"	TYP-2	4/A602	5/A602				3
235A	STAIR	EXIST	3'-0"	6'-8"	1 3/4"	EXIST	N/A	N/A	N/A	3/4 HR	00.01	
235B	CORRIDOR 240	HM-2	3'-0"	6'-8"	1 3/4"	TYP-2	4/A602	5/A602		3/4 HR	05.02	1
236	JANITOR CLOSET 236	WD-1	3'-0"	6'-8"	1 3/4"	EXIST	N/A	N/A	N/A		09.03	1 & 2
237	CLEAN LINEN 237	WD-1	3'-0"	6'-8"	1 3/4"	EXIST	N/A	N/A	N/A		09.04	1 & 2
238	STORAGE 238	WD-1	3'-0"	6'-8"	1 3/4"	EXIST	N/A	N/A	N/A	3/4 HR	09.02	1
239A	CORRIDOR 239	AL-1	3'-0"	7'-0"	1 3/4"	GLZ-C	10/A602	11/A602	9/A602	3/4 HR	01.01	4
239B	CORRIDOR 239	AL-1	3'-0"	7'-0"	1 3/4"	GLZ-D	10/A602 SIM.	13/A602	9/A602	3/4 HR	01.01	4
239C	STAIR	EXIST	3'-0"	6'-8"	1 3/4"	EXIST	N/A	N/A	N/A	3/4 HR	00.01	
239D	CORRIDOR 239	HM-2	3'-0"	6'-8"	1 3/4"	TYP-2	4/A602	5/A602		3/4 HR	05.02A	


DOOR AND FRAME SCHEDULE FLOOR 3

DOOR NUMBER	LOCATION	DOOR				FRAME				FIRE RATING	HARDWARE SETS	NOTES	
		TYPE	WIDTH	HEIGHT	THICKNESS	TYPE	HEAD	JAMB	SILL				
301A	DORM 301	WD-1	3'-0"	6'-8"	1 3/4"	EXIST	N/A	N/A	N/A	07.03		1	
301B	RESTROOM 301B	WD-1	2'-0"	6'-8"	1 3/4"	EXIST	N/A	N/A	N/A	06.01		1 & 2	
302A	DORM 302	WD-1	3'-0"	6'-8"	1 3/4"	EXIST	N/A	N/A	N/A	07.03		1	
302B	RESTROOM 302B	WD-1	2'-0"	6'-8"	1 3/4"	EXIST	N/A	N/A	N/A	06.01		1 & 2	
303A	DORM 303	WD-1	3'-0"	6'-8"	1 3/4"	EXIST	N/A	N/A	N/A	07.03		1	
303B	RESTROOM 303B	WD-1	2'-0"	6'-8"	1 3/4"	EXIST	N/A	N/A	N/A	06.01		1 & 2	
304A	DORM 304	WD-1	3'-0"	6'-8"	1 3/4"	EXIST	N/A	N/A	N/A	07.03		1	
304B	RESTROOM 302B	WD-1	2'-0"	6'-8"	1 3/4"	EXIST	N/A	N/A	N/A	06.01		1 & 2	
305A	DORM 305	WD-1	3'-0"	6'-8"	1 3/4"	EXIST	N/A	N/A	N/A	07.03		1	
305B	RESTROOM 303B	WD-1	2'-0"	6'-8"	1 3/4"	EXIST	N/A	N/A	N/A	06.01		1 & 2	
306A	DORM 306	WD-1	3'-0"	6'-8"	1 3/4"	EXIST	N/A	N/A	N/A	07.03		1	
306B	RESTROOM 306B	WD-1	2'-0"	6'-8"	1 3/4"	EXIST	N/A	N/A	N/A	06.01		1 & 2	
307A	DORM 307	WD-1	3'-0"	6'-8"	1 3/4"	EXIST	N/A	N/A	N/A	07.03		1	
307B	RESTROOM 307B	WD-1	2'-0"	6'-8"	1 3/4"	EXIST	N/A	N/A	N/A	06.01		1 & 2	
308A	DORM 308	WD-1	3'-0"	6'-8"	1 3/4"	EXIST	N/A	N/A	N/A	07.03		1	
308B	RESTROOM 306B	WD-1	2'-0"	6'-8"	1 3/4"	EXIST	N/A	N/A	N/A	06.01		1 & 2	
309A	DORM 309	WD-1	3'-0"	6'-8"	1 3/4"	EXIST	N/A	N/A	N/A	07.03		1	
309B	RESTROOM 307B	WD-1	2'-0"	6'-8"	1 3/4"	EXIST	N/A	N/A	N/A	06.01		1 & 2	
310A	DORM 310	WD-1	3'-0"	6'-8"	1 3/4"	EXIST	N/A	N/A	N/A	07.03		1	
310B	RESTROOM 310B	WD-1	2'-0"	6'-8"	1 3/4"	EXIST	N/A	N/A	N/A	06.01		1 & 2	
311A	DORM 311	WD-1	3'-0"	6'-8"	1 3/4"	EXIST	N/A	N/A	N/A	07.03		1	
311B	RESTROOM 311B	WD-1	2'-0"	6'-8"	1 3/4"	EXIST	N/A	N/A	N/A	06.01		1 & 2	
312A	DORM 312	WD-1	3'-0"	6'-8"	1 3/4"	EXIST	N/A	N/A	N/A	07.03		1	
312B	RESTROOM 310B	WD-1	2'-0"	6'-8"	1 3/4"	EXIST	N/A	N/A	N/A	06.01		1 & 2	
313A	DORM 313	WD-1	3'-0"	6'-8"	1 3/4"	EXIST	N/A	N/A	N/A	07.03		1	
313B	RESTROOM 311B	WD-1	2'-0"	6'-8"	1 3/4"	EXIST	N/A	N/A	N/A	06.01		1 & 2	
314A	DORM 314	WD-1	3'-0"	6'-8"	1 3/4"	EXIST	N/A	N/A	N/A	07.03		1	
314B	RESTROOM 314B	WD-1	2'-0"	6'-8"	1 3/4"	EXIST	N/A	N/A	N/A	06.01		1 & 2	
315A	ACCESSIBLE DORM 315	WD-1	3'-0"	6'-8"	1 3/4"	TYP-2	4/A602	5/A602		07.02			
315B	ACCESSIBLE RESTROOM 315B	WD-1	3'-0"	6'-8"	1 3/4"	TYP-2	4/A602	5/A602		06.01		2	
316A	DORM 316	WD-1	3'-0"	6'-8"	1 3/4"	EXIST	N/A	N/A	N/A	07.03		1	
316B	RESTROOM 314B	WD-1	2'-0"	6'-8"	1 3/4"	EXIST	N/A	N/A	N/A	06.01		1 & 2	
317A	DORM 317	WD-1	3'-0"	6'-8"	1 3/4"	EXIST	N/A	N/A	N/A	07.03		1	
317B	RESTROOM 317B	WD-1	2'-0"	6'-8"	1 3/4"	EXIST	N/A	N/A	N/A	06.01		1 & 2	
318A	DORM 318	WD-1	3'-0"	6'-8"	1 3/4"	EXIST	N/A	N/A	N/A	07.03		1	
318B	RESTROOM 318B	WD-1	2'-0"	6'-8"	1 3/4"	EXIST	N/A	N/A	N/A	06.01		1 & 2	
319A	DORM 319	WD-1	3'-0"	6'-8"	1 3/4"	EXIST	N/A	N/A	N/A	07.03		1	
319B	RESTROOM 317B	WD-1	2'-0"	6'-8"	1 3/4"	EXIST	N/A	N/A	N/A	06.01		1 & 2	
320A	DORM 320	WD-1	3'-0"	6'-8"	1 3/4"	EXIST	N/A	N/A	N/A	07.03		1	
320B	RESTROOM 318B	WD-1	2'-0"	6'-8"	1 3/4"	EXIST	N/A	N/A	N/A	06.01		1 & 2	
321A	DORM 321	WD-1	3'-0"	6'-8"	1 3/4"	EXIST	N/A	N/A	N/A	07.03		1	
321B	RESTROOM 321B	WD-1	2'-0"	6'-8"	1 3/4"	EXIST	N/A	N/A	N/A	06.01		1 & 2	
322A	DORM 322	WD-1	3'-0"	6'-8"	1 3/4"	EXIST	N/A	N/A	N/A	07.03		1	
322B	RESTROOM 322B	WD-1	2'-0"	6'-8"	1 3/4"	EXIST	N/A	N/A	N/A	06.01		1 & 2	
323A	DORM 323	WD-1	3'-0"	6'-8"	1 3/4"	EXIST	N/A	N/A	N/A	07.03		1	
323B	RESTROOM 321B	WD-1	2'-0"	6'-8"	1 3/4"	EXIST	N/A	N/A	N/A	06.01		1 & 2	
324A	DORM 324	WD-1	3'-0"	6'-8"	1 3/4"	EXIST	N/A	N/A	N/A	07.03		1	
324B	RESTROOM 322B	WD-1	2'-0"	6'-8"	1 3/4"	EXIST	N/A	N/A	N/A	06.01		1 & 2	
325A	DORM 325	WD-1	3'-0"	6'-8"	1 3/4"	EXIST	N/A	N/A	N/A	07.03		1	
325B	RESTROOM 325B	WD-1	2'-0"	6'-8"	1 3/4"	EXIST	N/A	N/A	N/A	06.01		1 & 2	
326A	ACCESSIBLE DORM 326	WD-1	3'-0"	6'-8"	1 3/4"	EXIST	N/A	N/A	N/A	07.02		1	
326B	ACCESSIBLE RESTROOM 326B	WD-1	3'-0"	6'-8"	1 3/4"	TYP-2	4/A602	5/A602		06.01		2	
327A	DORM 327	WD-1	3'-0"	6'-8"	1 3/4"	EXIST	N/A	N/A	N/A	07.03		1	
327B	RESTROOM 325B	WD-1	2'-0"	6'-8"	1 3/4"	EXIST	N/A	N/A	N/A	06.01		1 & 2	
328A	DORM 328	WD-1	3'-0"	6'-8"	1 3/4"	EXIST	N/A	N/A	N/A	07.03		1	
328B	RESTROOM 328B	WD-1	2'-0"	6'-8"	1 3/4"	EXIST	N/A	N/A	N/A	06.01		1 & 2	
329A	DORM 329	WD-1	3'-0"	6'-8"	1 3/4"	EXIST	N/A	N/A	N/A	07.03		1	
329B	RESTROOM 329B	WD-1	2'-0"	6'-8"	1 3/4"	EXIST	N/A	N/A	N/A	06.01		1 & 2	
330A	DORM 330	WD-1	3'-0"	6'-8"	1 3/4"	EXIST	N/A	N/A	N/A	07.03		1	
330B	RESTROOM 328B	WD-1	2'-0"	6'-8"	1 3/4"	EXIST	N/A	N/A	N/A	06.01		1 & 2	
331A	DORM 331	WD-1	3'-0"	6'-8"	1 3/4"	EXIST	N/A	N/A	N/A	07.03		1	
331B	RESTROOM 329B	WD-1	2'-0"	6'-8"	1 3/4"	EXIST	N/A	N/A	N/A	06.01		1 & 2	
332A	LIVING ROOM 332	WD-1	3'-0"	6'-8"	1 3/4"	TYP-2	4/A602	5/A602		07.03			
332B	RESTROOM 332B	WD-1	3'-0"	6'-8"	1 3/4"	TYP-2	4/A602	5/A602		06.01		2	
332C	BEDROOM 332C	WD-2	3'-0"	6'-8"	1 3/4"	TYP-2	4/A602	5/A602		06.01		3	
332D	BEDROOM 332D	WD-2	3'-0"	6'-8"	1 3/4"	TYP-2	4/A602	5/A602		06.01		3	
333A	STAIR	EXIST	3'-0"	6'-8"	1 3/4"	EXIST	N/A	N/A	N/A		3/4 HR	00.01	1
333B	CORRIDOR 341	HM-2	3'-0"	6'-8"	1 3/4"	TYP-2	4/A602	5/A602			3/4 HR	05.02	
334	UNIXEST RESTROOM 334A	WD-2	3'-0"	6'-8"	1 3/4"	TYP-2	4/A602	5/A602				06.02	
335A	STAIR	EXIST	3'-0"	6'-8"	1 3/4"	EXIST	N/A	N/A	N/A		3/4 HR	00.01	1
335B	CORRIDOR 341	HM-2	3'-0"	6'-8"	1 3/4"	TYP-2	4/A602	5/A602			3/4 HR	05.02	
336A	JANITOR CLOSET 336A	WD-1	3'-0"	6'-8"	1 3/4"	EXIST	N/A	N/A	N/A			09.03	1 & 2
336B	STORAGE 336B	WD-1	3'-0"	6'-8"	1 3/4"	TYP-2	4/A602	5/A602				09.02	
337	CLEAN LINEN 337	WD-1	3'-0"	6'-8"	1 3/4"	EXIST	N/A	N/A	N/A			09.04	1 & 2
338A	STAIR	EXIST	3'-0"	6'-8"	1 3/4"	EXIST	N/A	N/A	N/A		3/4 HR		1
338B	CORRIDOR 340	HM-2	3'-0"	6'-8"	1 3/4"	TYP-2	4/A602	5/A602			3/4 HR	05.02	
339	STORAGE 339	WD-1	3'-0"	6'-8"	1 3/4"	EXIST	N/A	N/A	N/A		3/4 HR	09.02	1


GENERAL NOTE: REFER TO SHEET A-602 FOR DOOR AND FRAME TYPES.

NOTES:


- COORDINATE HARDWARE WITH OPENINGS ON EXIST. H.M. FRAMES
- UNDERCUT DOOR 1"
- 12" X 6" LOUVER
- ACCESS/CARD READER, PROVIDE BY & INSTALLED BY OWNER, CONDUIT BY G.C.

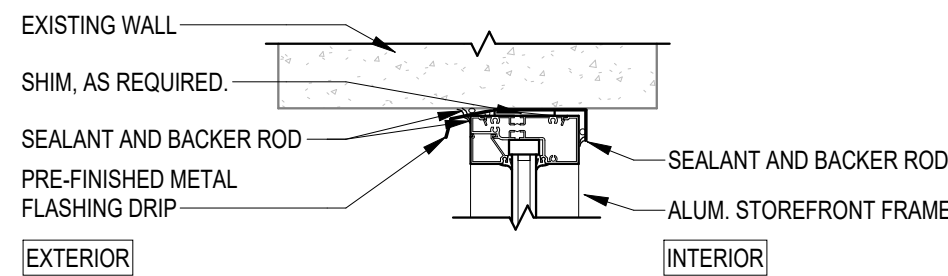


10 WINDOW HEAD
A-602 SCALE: 1 1/2" = 1'-0"

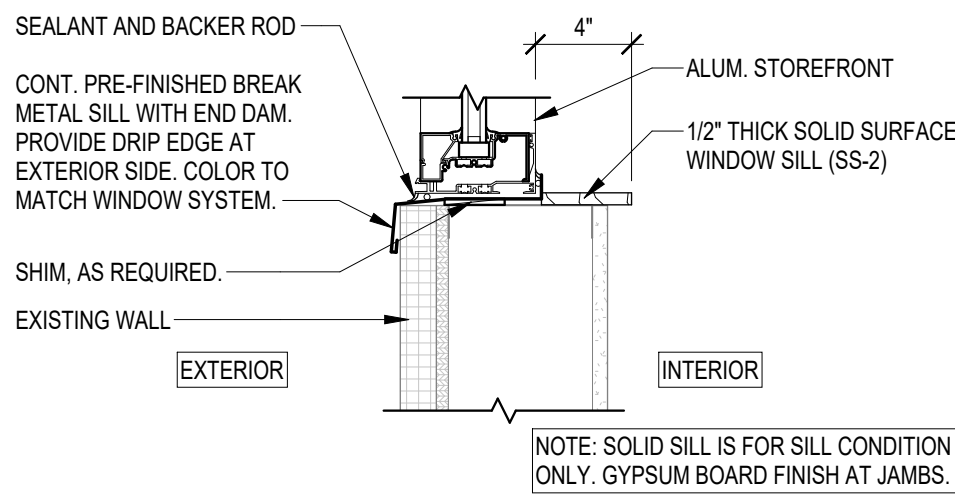


11 WINDOW SILL
A-602 SCALE: 1 1/2" = 1'-0"

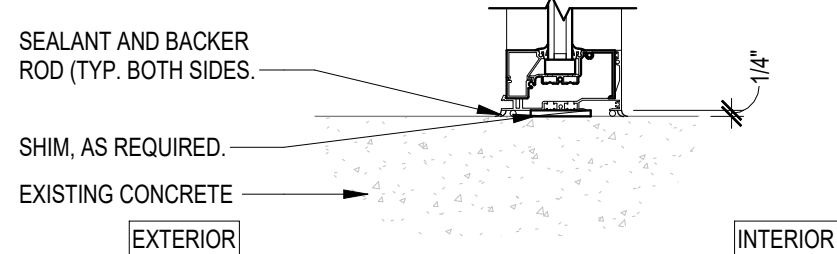


12 WINDOW SILL
A-602 SCALE: 1 1/2" = 1'-0"

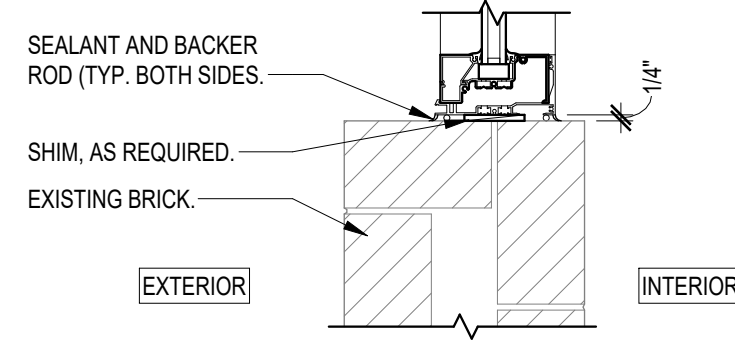


13 WINDOW JAMB
A-602 SCALE: 1 1/2" = 1'-0"

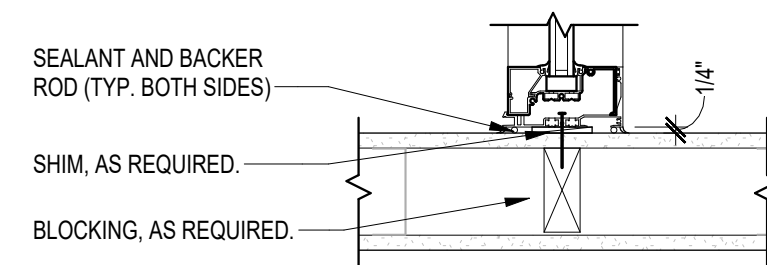


14 WINDOW JAMB
A-602 SCALE: 1 1/2" = 1'-0"

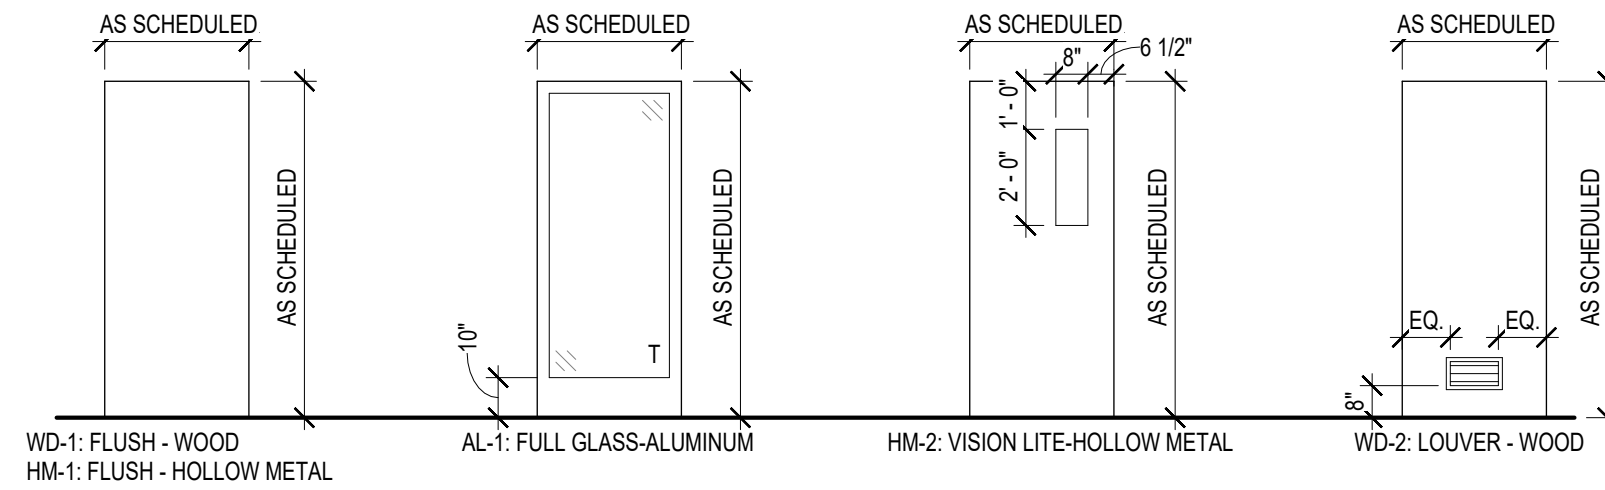


1 DOOR TYPES
A-602 SCALE: 1/4" = 1'-0"

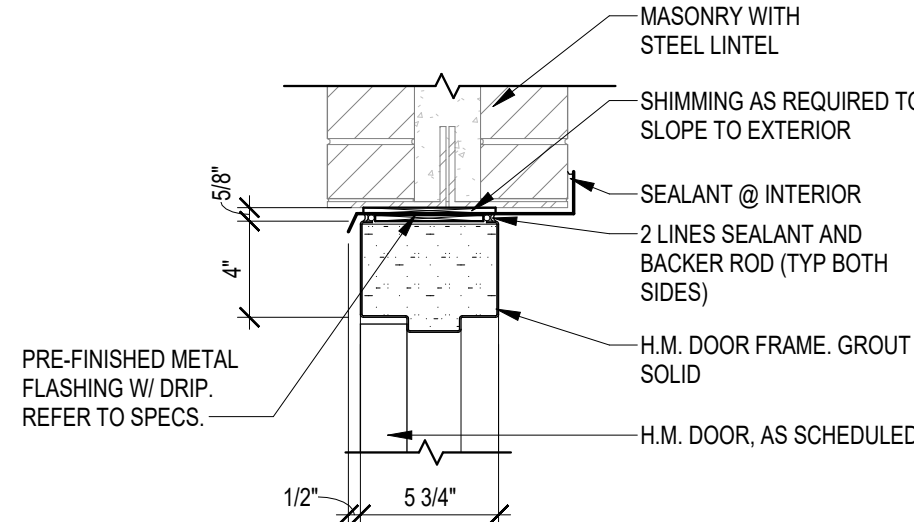


3 DOOR HEAD - HM DOOR @ BRICK
A-602 SCALE: 1 1/2" = 1'-0"

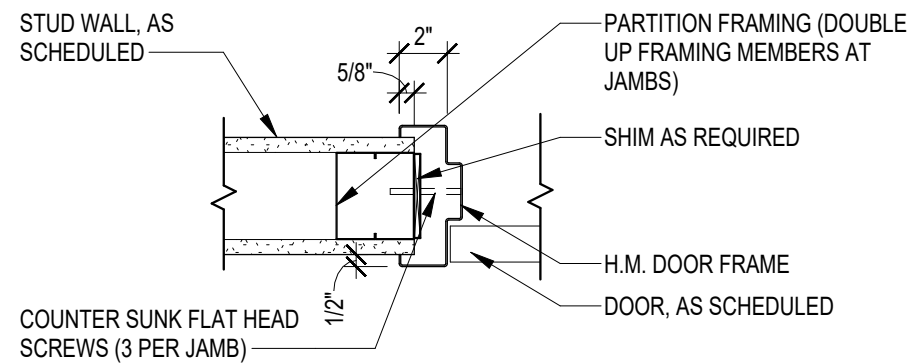


5 DOOR JAMB - HM DOOR @ GWB
A-602 SCALE: 1 1/2" = 1'-0"

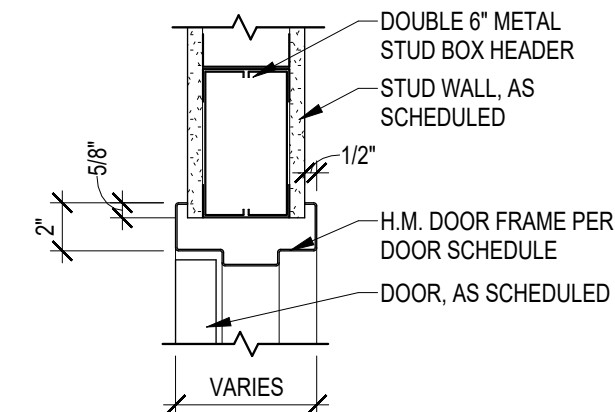


4 DOOR HEAD - HM DOOR @ GWB
A-602 SCALE: 1 1/2" = 1'-0"

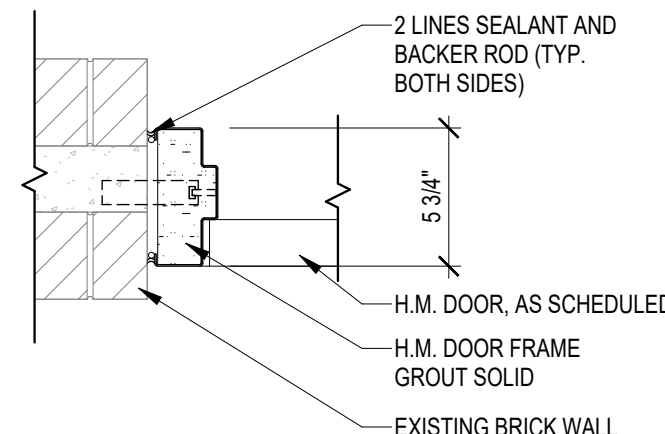

6 DOOR JAMB - HM DOOR @ BRICK
A-602 SCALE: 1 1/2" = 1'-0"

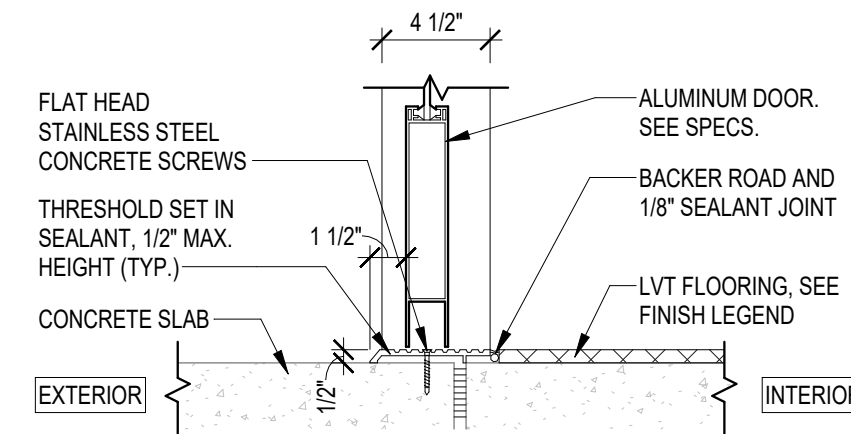

9 DOOR SILL - ALUMINUM DOOR
A-602 SCALE: 1 1/2" = 1'-0"

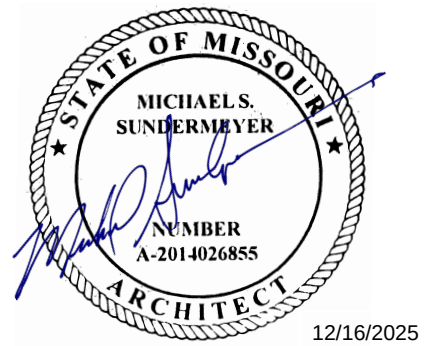

REVISIONS

No.	Description	Date
-----	-------------	------

ISSUE DATE:12/16/25

DWG FILE #: 2404694
DRAWN BY: LAA
CHECKED BY: JVR
DESIGNED BY: RAR

SHEET TITLE:
DORM DOOR SCHEDULE AND
DETAILS

SHEET NUMBER: